=P1.WN-U1　　极1中性母线直流分压器

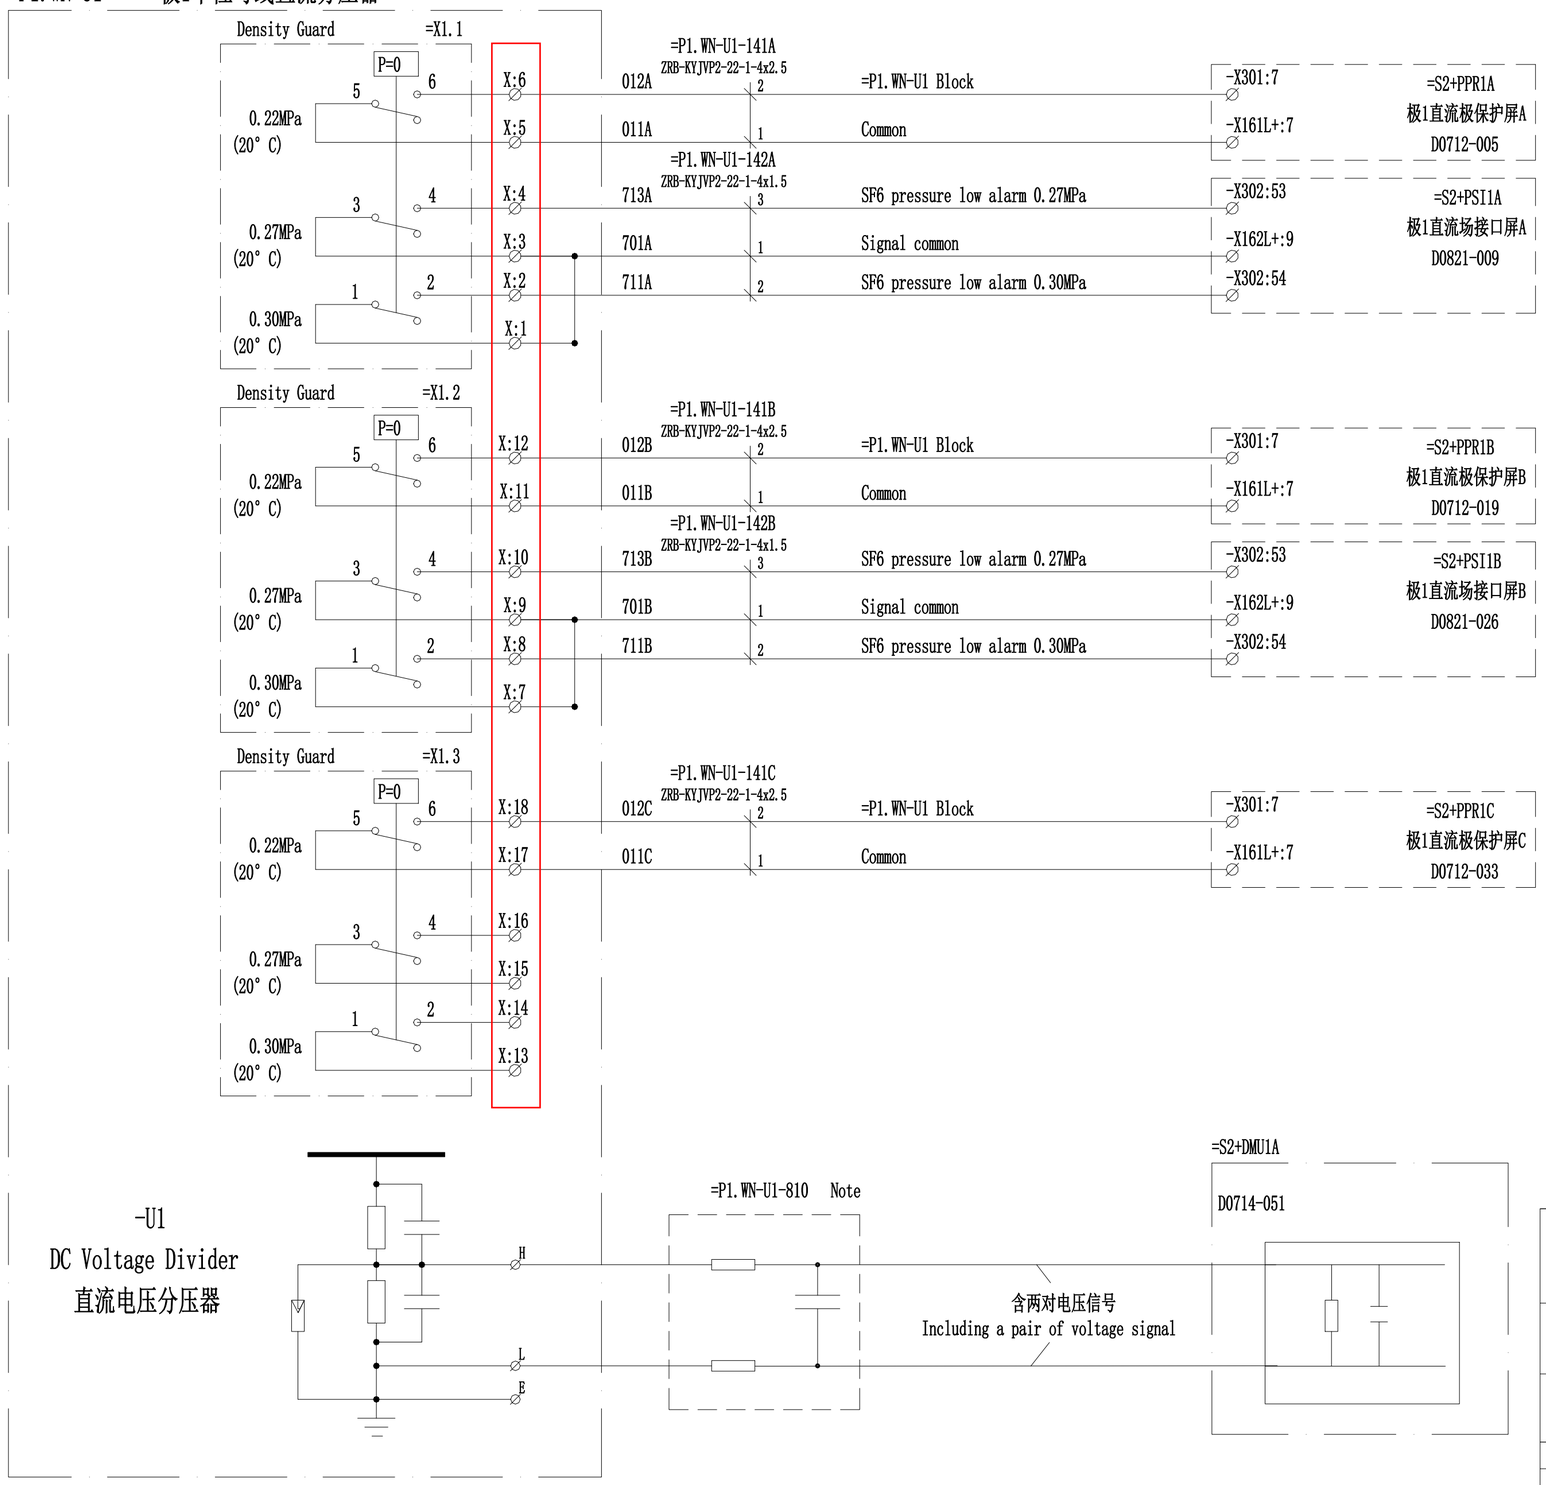

注：该同轴电缆由厂家提供，虚线框内为同轴电缆的等效电路图。

Note: The coaxial cable is provided by the manufacturer and the dotted line frame shows the equivalent circuit of the coaxial cable.

巴基斯坦默蒂亚里—拉合尔±660kV直流输电工程

±660kV HVDC Project from Matiari to Lahore in Pakistan

NATIONAL TRANSMISSION & DESPATCH COMPANY (NTDC) LIMITED PAKISTAN

CONTRACTOR 国家电网 STATE GRID 中国电力技术装备有限公司 CHINA ELECTRIC POWER EQUIPMENT AND TECHNOLOGY CO.,LTD.

SUBCONTRACTOR East China Electric Power Design Institute Co.,Ltd.

拉合尔±660kV换流站

±660kV Lahore Converter Station

设计阶段 PHASE: 施工图 Detail Design

M L H V D C - E N G - E C I - D D - P C - 0 7 4 1 - 0 9 1 A

	姓名 Name	日期 Date
设计 Designed	徐亮亮	2020.2.25
校核 Checked	徐勇	2020.2.25
审核 Reviewed	王重雄	2020.2.25
批准 Approved	李佑祥	2020.2.25

=P1.WN-U1极1直流分压器接线图

Schematic diagram (=P1.WN-U1)

比例 Scale

图号 DWG NO. 30-B003701S-D0714-091

版本 REV. A

297X420