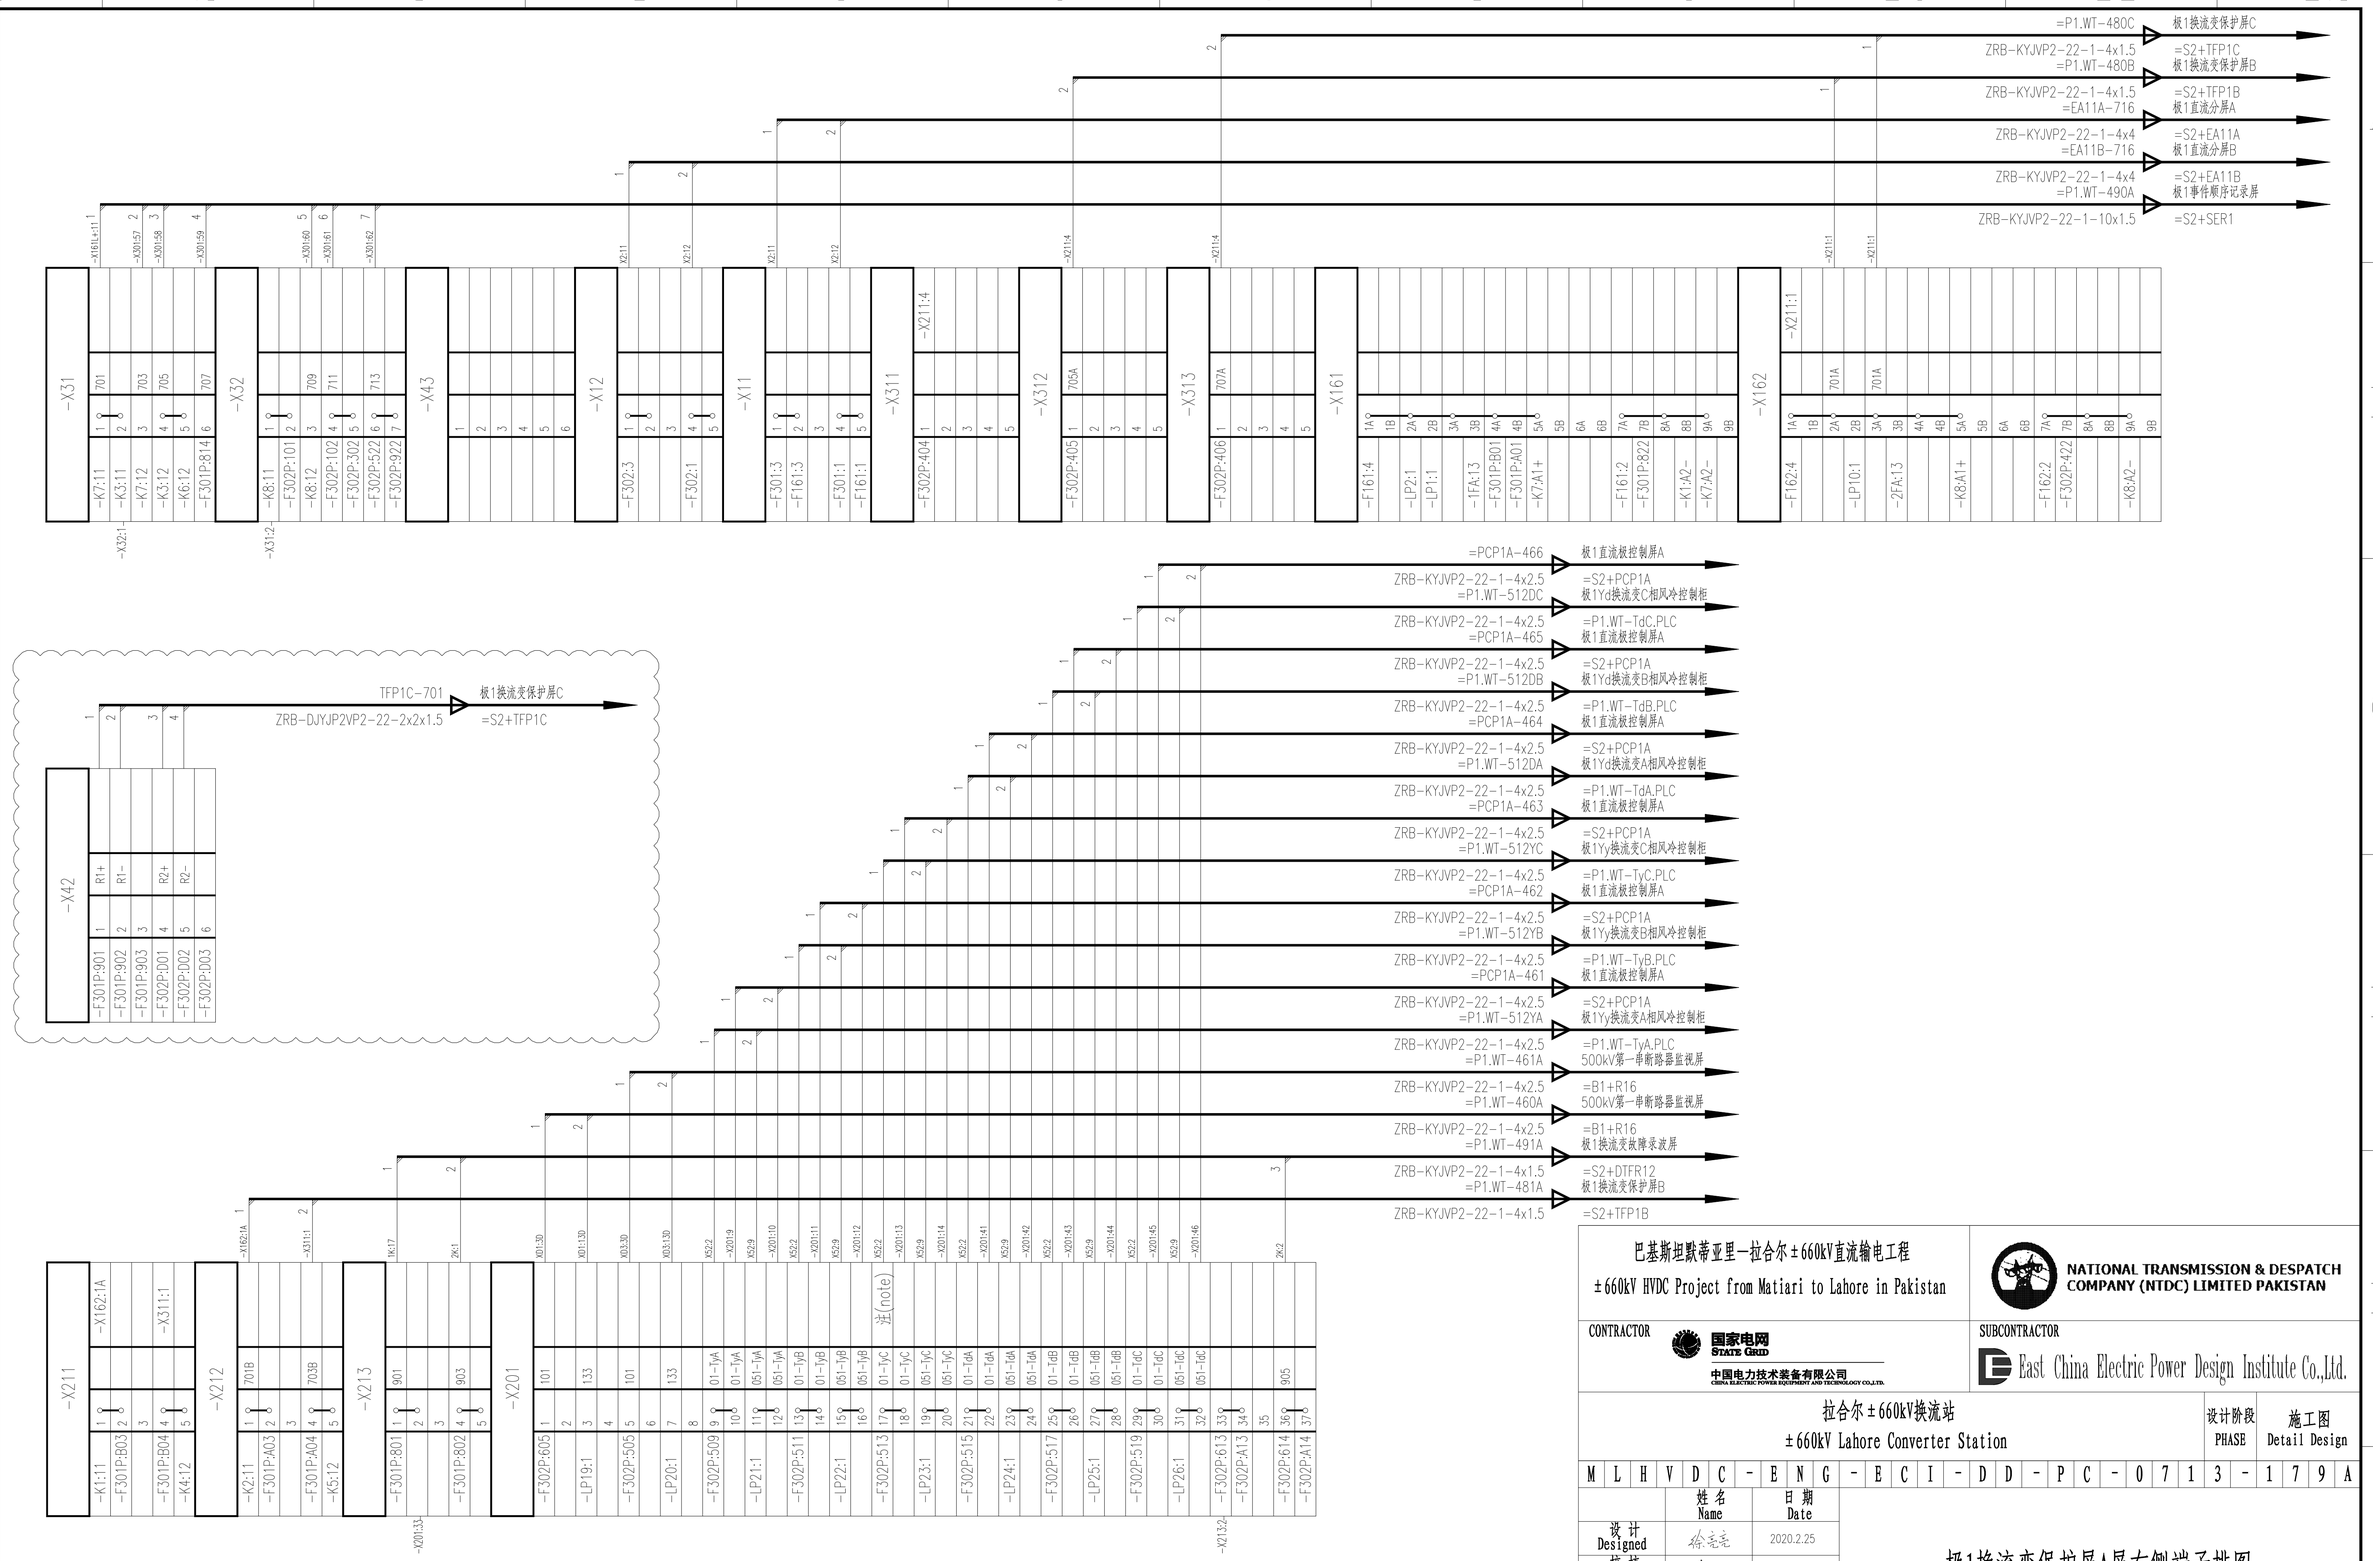


注：增加端子9-10、11-12、13-14、15-16、17-18、19-20、21-22、23-24、25-26、27-28、29-30、31-32之间的短接片。

Note: The connection piece needs to be increased between terminals 9-10、11-12、13-14、15-16、17-18、19-20、21-22、23-24、25-26、27-28、29-30、31-32.

巴基斯坦默蒂亚里—拉合尔±660kV直流输电工程

±660kV HVDC Project from Matiari to Lahore in Pakistan

NATIONAL TRANSMISSION & DESPATCH COMPANY (NTDC) LIMITED PAKISTAN

CONTRACTOR 国家电网 STATE GRID 中国电力技术装备有限公司 CHINA ELECTRIC POWER EQUIPMENT AND TECHNOLOGY CO.,LTD.

SUBCONTRACTOR East China Electric Power Design Institute Co.,Ltd.

拉合尔±660kV换流站

±660kV Lahore Converter Station

设计阶段 PHASE: 施工图 Detail Design

M L H V D C - E N G - E C I - D D - P C - 0 7 1 3 - 1 7 9 A

| | 姓名 Name | 日期 Date |
|---|---|---|
| 设计 Designed | 徐亮亮 | 2020.2.25 |
| 校核 Checked | 徐勇 | 2020.2.25 |
| 审核 Reviewed | 王建伟 | 2020.2.25 |
| 批准 Approved | 李佑准 | 2020.2.25 |

# 极1换流变保护屏A屏右侧端子排图
# Right terminal diagram(=S2+TFP1A)

比例 Scale: 图号 DWG NO.: 30-B003701S-D0713-179 版本 REV.: A

420X594