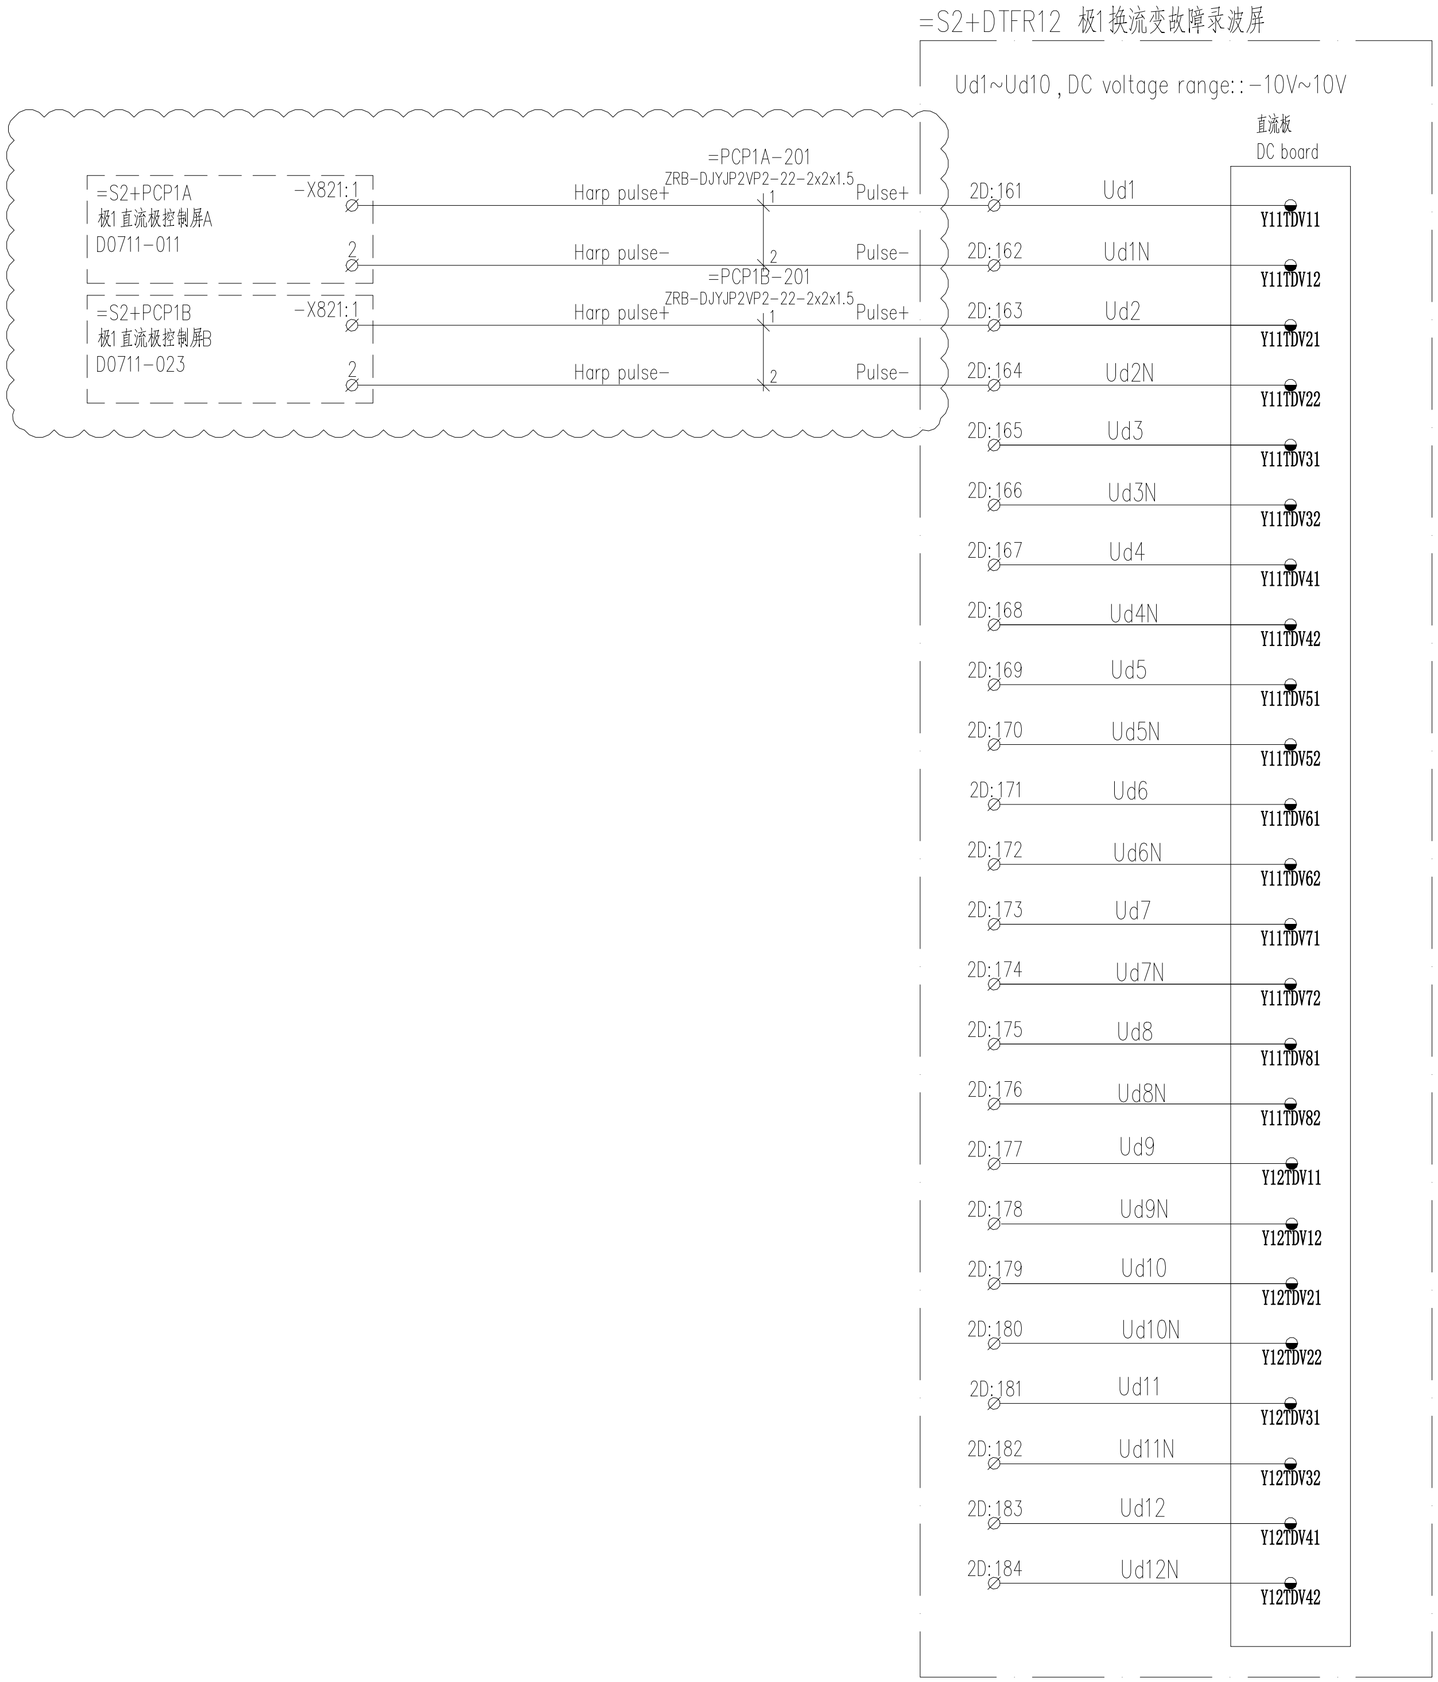

巴基斯坦默蒂亚里—拉合尔±660kV直流输电工程

±660kV HVDC Project from Matiari to Lahore in Pakistan

NATIONAL TRANSMISSION & DESPATCH COMPANY (NTDC) LIMITED PAKISTAN

CONTRACTOR 国家电网 STATE GRID 中国电力技术装备有限公司 CHINA ELECTRIC POWER EQUIPMENT AND TECHNOLOGY CO.,LTD.

SUBCONTRACTOR East China Electric Power Design Institute Co.,Ltd.

拉合尔±660kV换流站

±660kV Lahore Converter Station

设计阶段 PHASE: 施工图 Detail Design

M L H V D C - E N G - E C I - D D - P C - 0 8 1 0 - 0 1 8 A

	姓名 Name	日期 Date
设计 Designed	王建伟	2020.02.14
校核 Checked	徐勇	2020.02.18
审核 Reviewed	陈强	2020.02.24
批准 Approved	李钰雅	2020.02.27
比例 Scale		图号 DWG NO.

极1换流变故障录波器屏(DTFR12) 模拟量接线图11

Analog wiring diagram11(S2+DTFR12)

30-B003701S-D0801-018

版本 REV. A

297X420