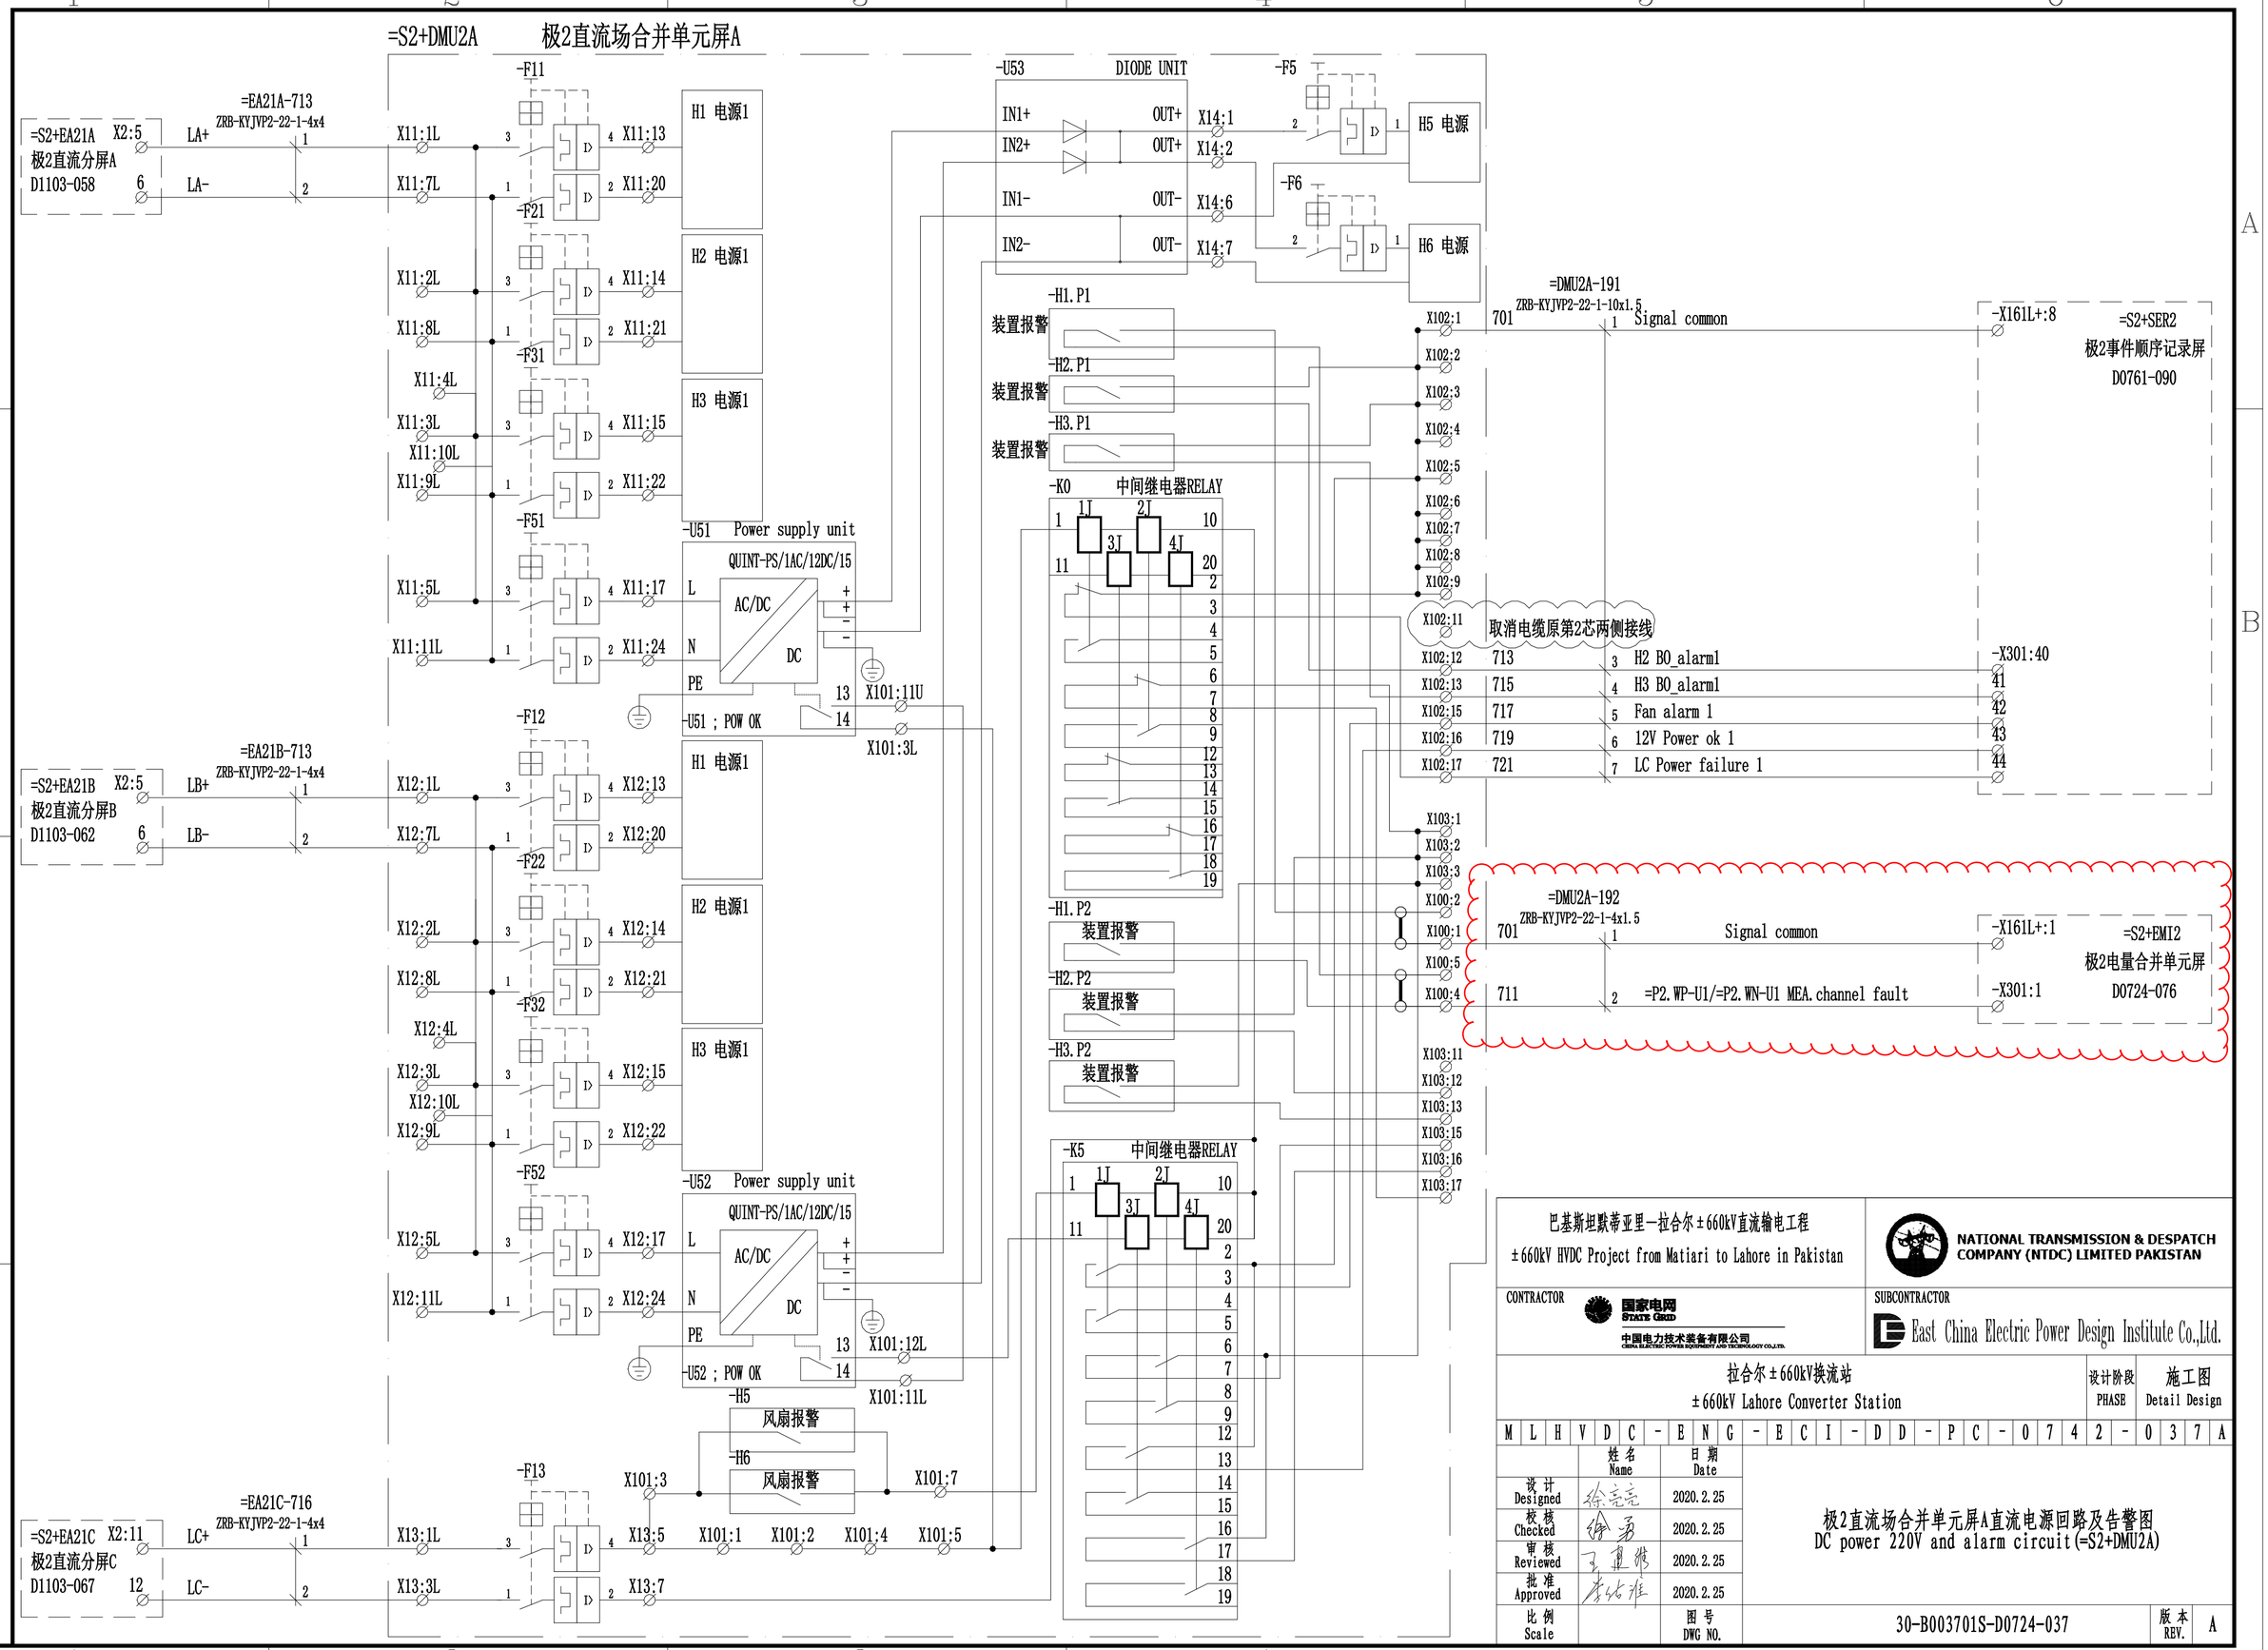
=S2+DMU2A 极2直流场合并单元屏A
=S2+EA21A X2:5 极2直流分屏A D1103-058
=EA21A-713 ZRB-KYJVP2-22-1-4x4
LA+
LA-
=S2+EA21B X2:5 极2直流分屏B D1103-062
=EA21B-713 ZRB-KYJVP2-22-1-4x4
LB+
LB-
=S2+EA21C X2:11 极2直流分屏C D1103-067
=EA21C-716 ZRB-KYJVP2-22-1-4x4
LC+
LC-
-F11
-F21
-F31
-F51
-F12
-F22
-F32
-F52
-F13
H1 电源1
H2 电源1
H3 电源1
-U51 Power supply unit
QUINT-PS/1AC/12DC/15
AC/DC
DC
-U51 ; POW OK
-U52 Power supply unit
-U52 ; POW OK
X101:11U
X101:3L
X101:12L
X101:11L
-H5
风扇报警
-H6
风扇报警
X101:3
X101:7
X101:1
X101:2
X101:4
X101:5
-U53 DIODE UNIT
IN1+
IN2+
IN1-
IN2-
OUT+
OUT-
-F5
-F6
H5 电源
H6 电源
-H1.P1
-H2.P1
-H3.P1
装置报警
-K0 中间继电器RELAY
-K5 中间继电器RELAY
=DMU2A-191 ZRB-KYJVP2-22-1-10x1.5
701 Signal common
713 H2 BO_alarm1
715 H3 BO_alarm1
717 Fan alarm 1
719 12V Power ok 1
721 LC Power failure 1
取消电缆原第2芯两侧接线
=S2+SER2 极2事件顺序记录屏 D0761-090
-X161L+:8
-X301:40
=DMU2A-192 ZRB-KYJVP2-22-1-4x1.5
701 Signal common
711 =P2.WP-U1/=P2.WN-U1 MEA.channel fault
=S2+EMI2 极2电量合并单元屏 D0724-076
-X161L+:1
-X301:1
巴基斯坦默蒂亚里—拉合尔±660kV直流输电工程
±660kV HVDC Project from Matiari to Lahore in Pakistan
NATIONAL TRANSMISSION & DESPATCH COMPANY (NTDC) LIMITED PAKISTAN
CONTRACTOR
国家电网 STATE GRID
中国电力技术装备有限公司
SUBCONTRACTOR
East China Electric Power Design Institute Co.,Ltd.
拉合尔±660kV换流站
±660kV Lahore Converter Station
设计阶段 PHASE
施工图 Detail Design
M L H V D C - E N G - E C I - D D - P C - 0 7 4 2 - 0 3 7 A
姓名 Name
日期 Date
设计 Designed
校核 Checked
审核 Reviewed
批准 Approved
2020.2.25
极2直流场合并单元屏A直流电源回路及告警图
DC power 220V and alarm circuit(=S2+DMU2A)
比例 Scale
图号 DWG NO.
30-B003701S-D0724-037
版本 REV.
A
297X420