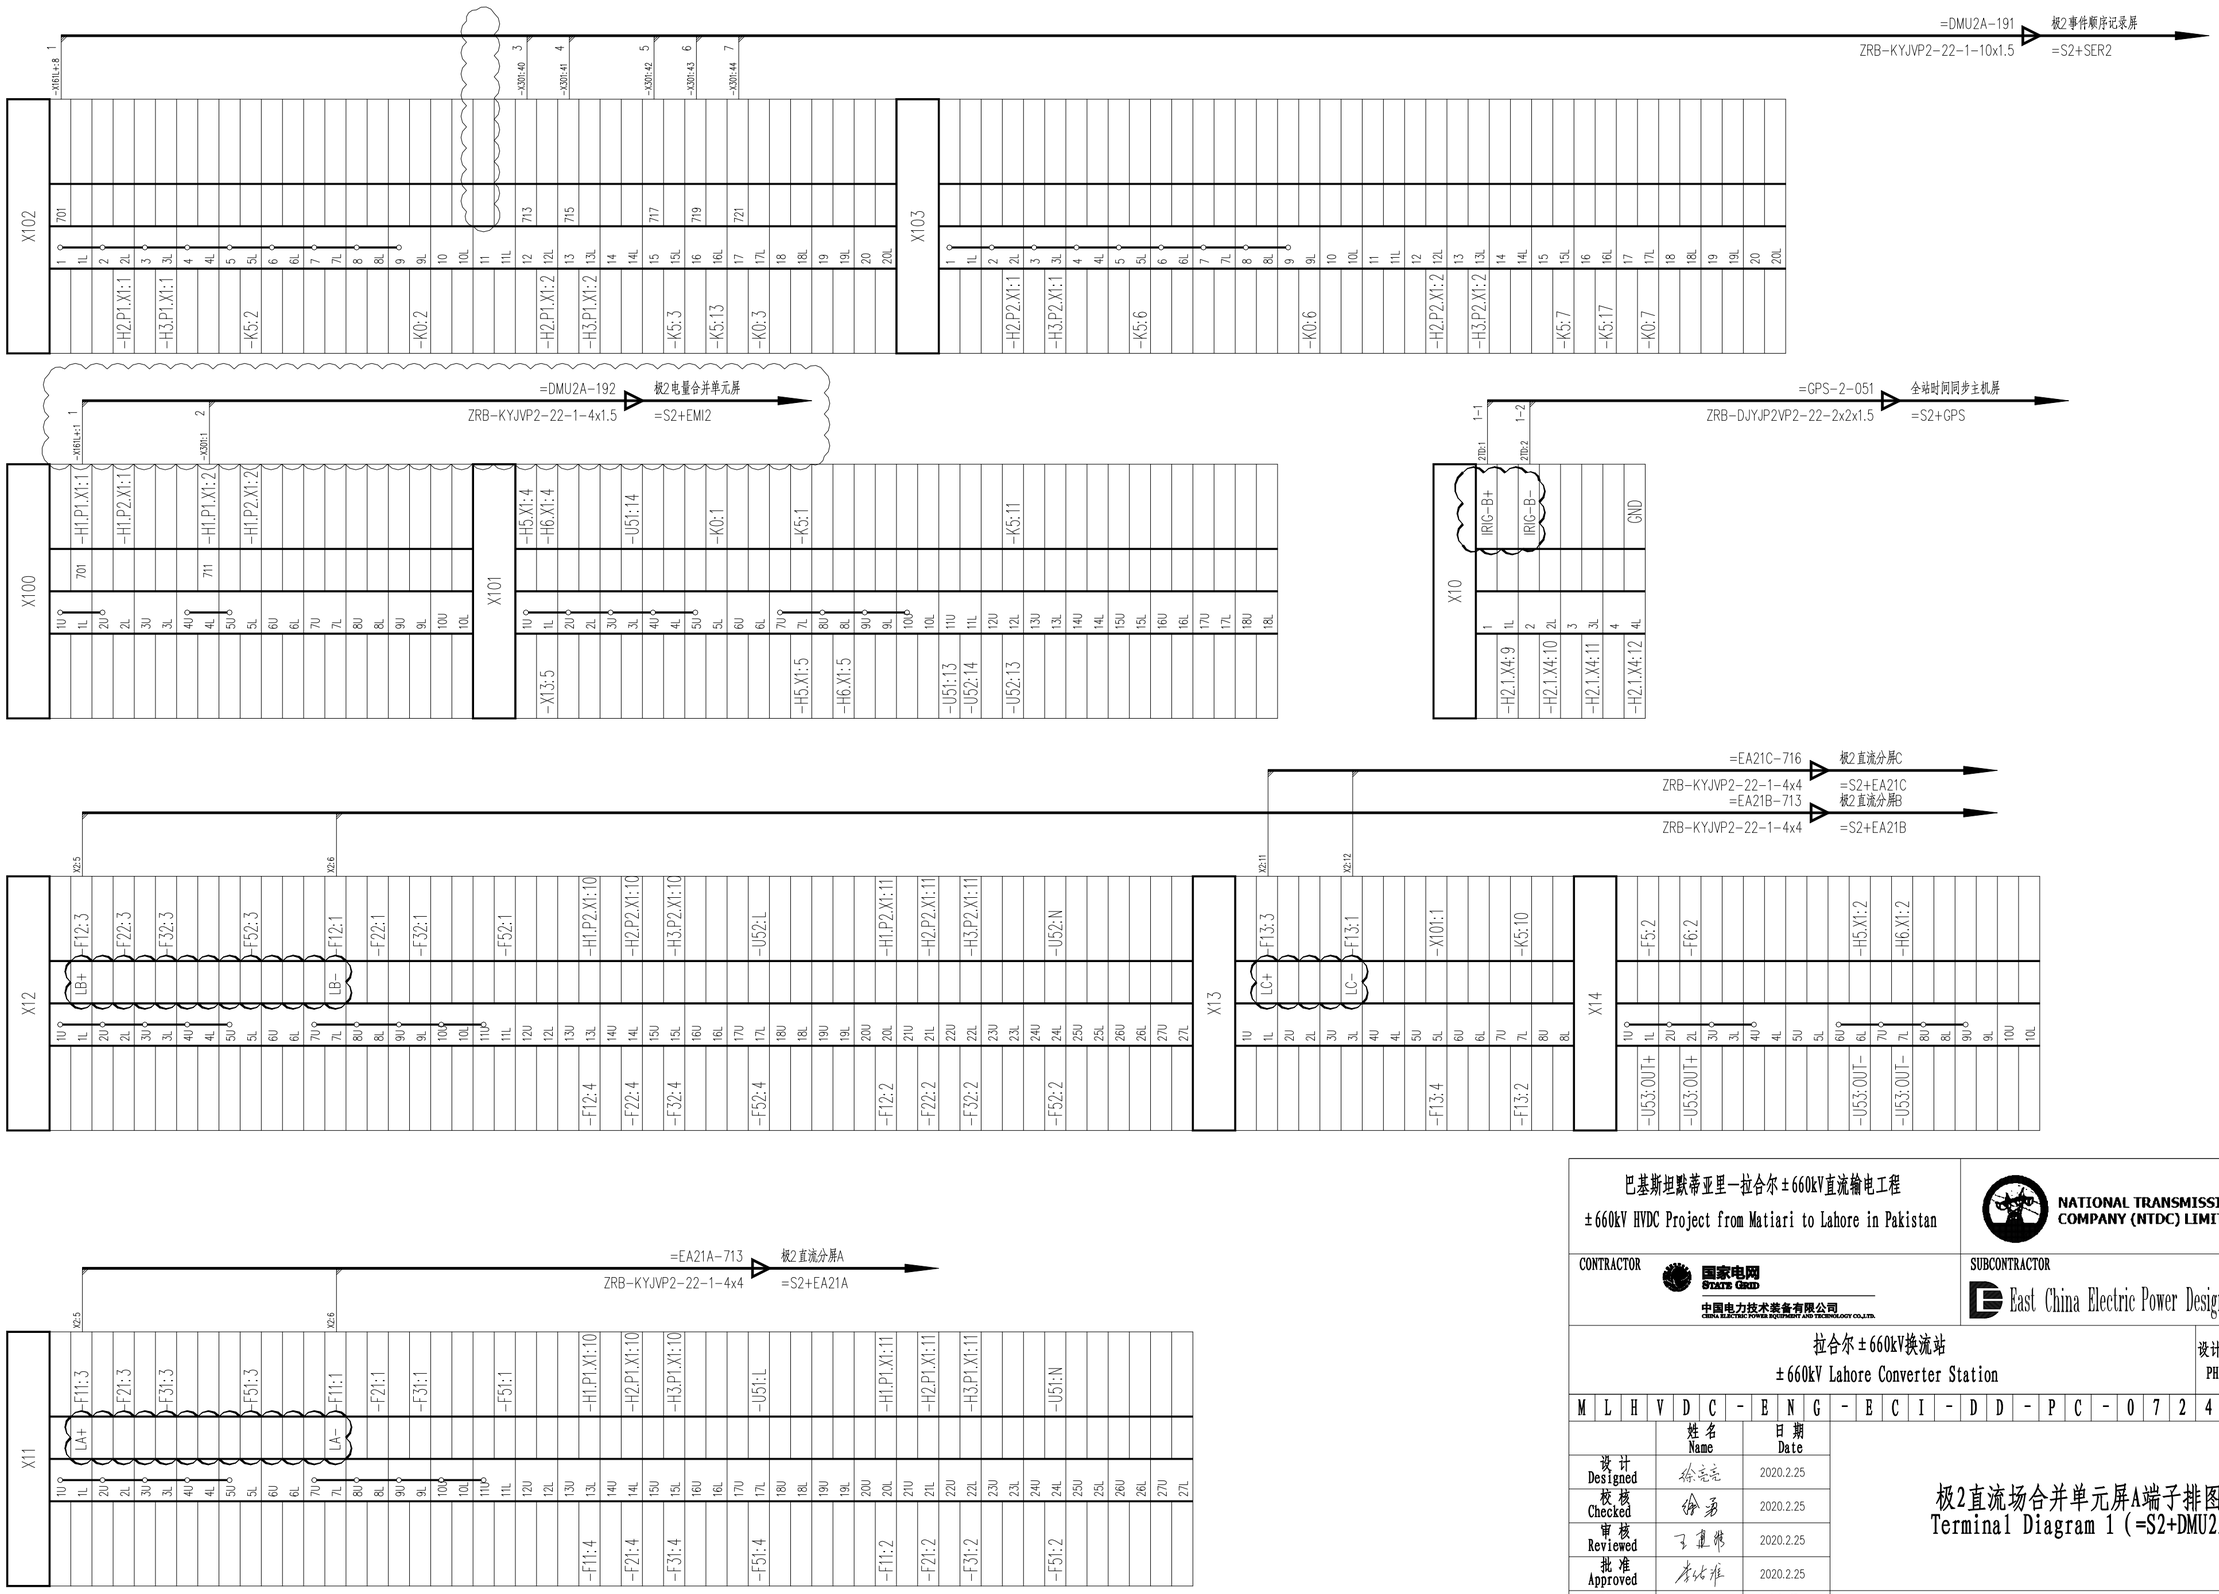

巴基斯坦默蒂亚里—拉合尔±660kV直流输电工程

±660kV HVDC Project from Matiari to Lahore in Pakistan

NATIONAL TRANSMISSION & DESPATCH COMPANY (NTDC) LIMITED PAKISTAN

CONTRACTOR 国家电网 STATE GRID 中国电力技术装备有限公司 CHINA ELECTRIC POWER EQUIPMENT AND TECHNOLOGY CO.,LTD.

SUBCONTRACTOR East China Electric Power Design Institute Co.,Ltd.

拉合尔±660kV换流站

±660kV Lahore Converter Station

设计阶段 PHASE: 施工图 Detail Design

MLHVDC-ENG-ECI-DD-PC-0724-098A

	姓名 Name	日期 Date
设计 Designed	徐亮亮	2020.2.25
校核 Checked	徐勇	2020.2.25
审核 Reviewed	王建锋	2020.2.25
批准 Approved	李佑雄	2020.2.25

极2直流场合并单元屏A端子排图一

Terminal Diagram 1 (=S2+DMU2A)

比例 Scale

图号 DWG NO.: 30-B003701S-D0724-098

版本 REV.: A

420X594