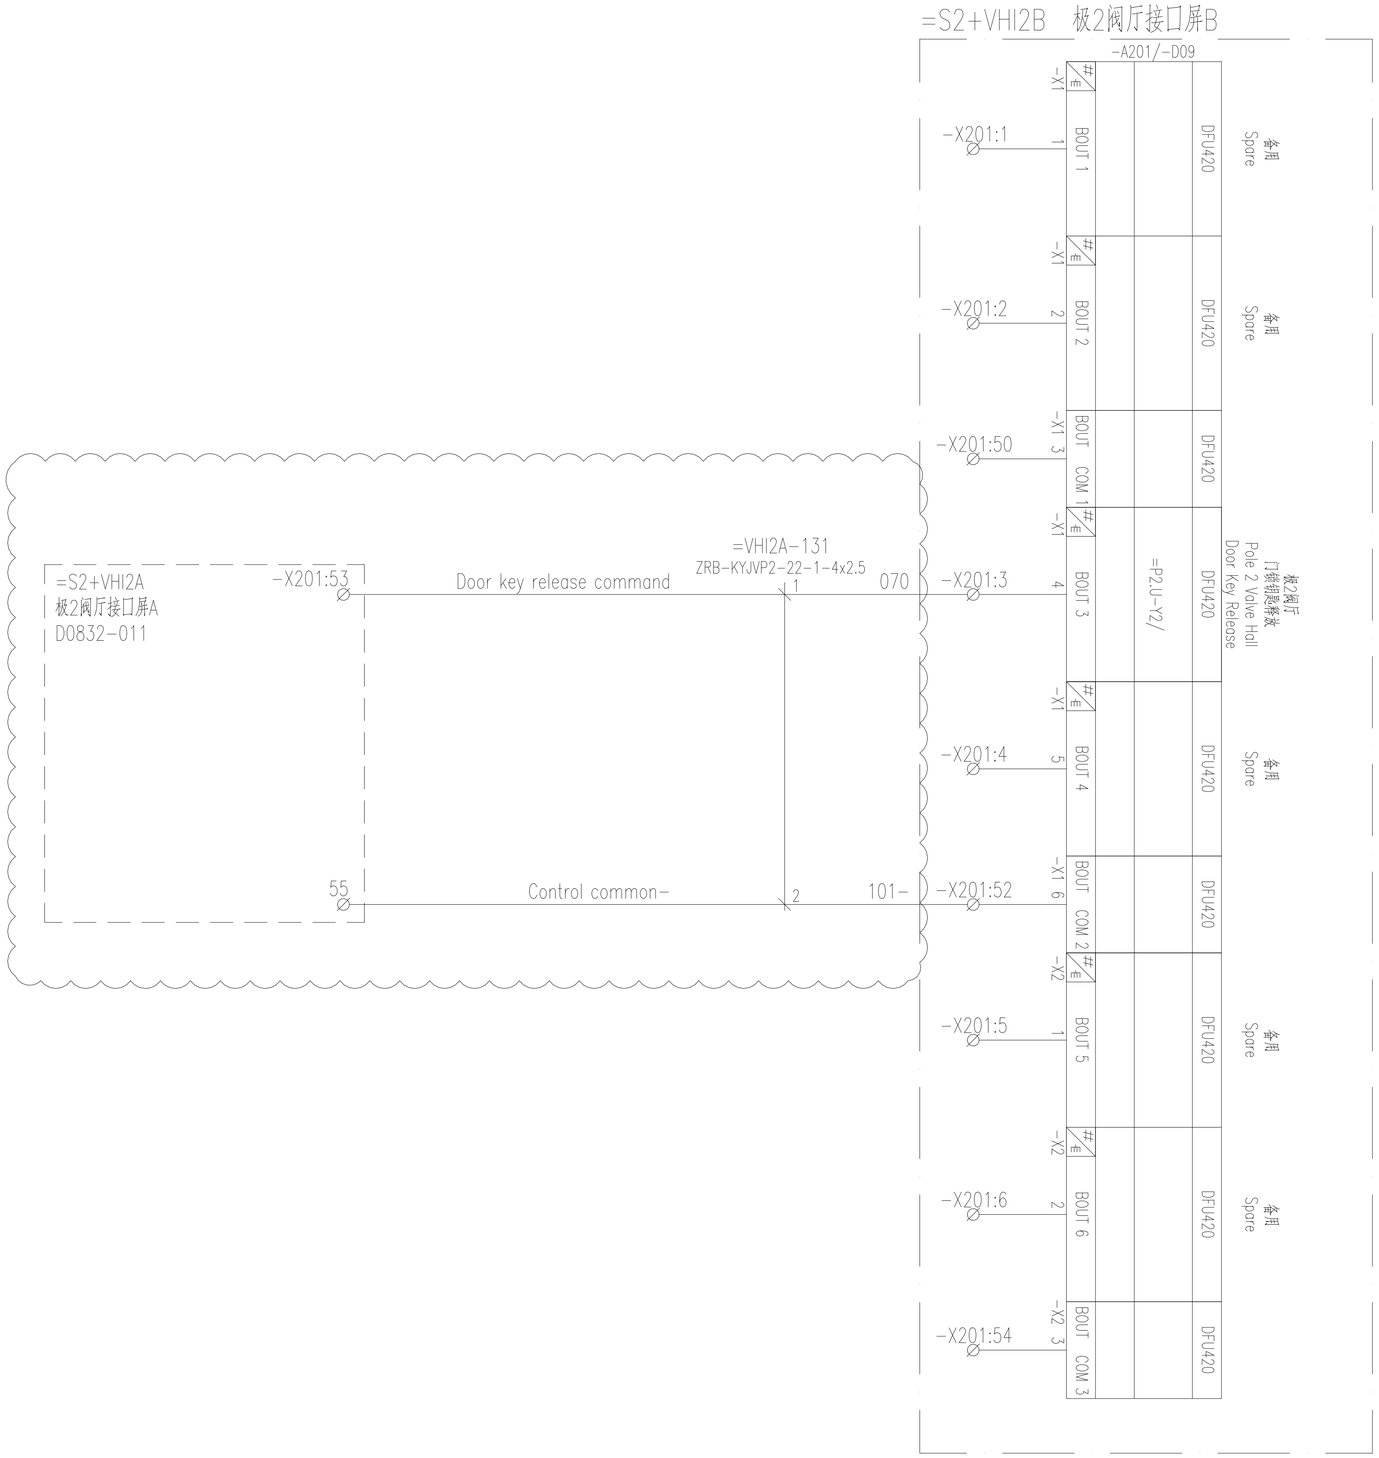


巴基斯坦默蒂亚里—拉合尔±660kV直流输电工程

±660kV HVDC Project from Matiari to Lahore in Pakistan

NATIONAL TRANSMISSION & DESPATCH COMPANY (NTDC) LIMITED PAKISTAN

CONTRACTOR 国家电网 STATE GRID 中国电力技术装备有限公司 CHINA ELECTRIC POWER EQUIPMENT AND TECHNOLOGY CO.,LTD.

SUBCONTRACTOR East China Electric Power Design Institute Co.,Ltd.

拉合尔±660kV换流站

±660kV Lahore Converter Station

设计阶段 PHASE: 施工图 Detail Design

M L H V D C - E N G - E C I - D D - P C - 0 8 2 3 - 0 3 0 A

| | 姓名 Name | 日期 Date |
|---|---|---|
| 设计 Designed | 陈波 | 2020.2.25 |
| 校核 Checked | 徐勇 | 2020.2.25 |
| 审核 Reviewed | 王建华 | 2020.2.25 |
| 批准 Approved | 李佑祥 | 2020.2.25 |

极2阀厅接口屏B B201开关量开出原理图一

A201 binary output 1(=S2+VHI2B)

比例 Scale

图号 DWG NO. 30-B003701S-D0832-030

版本 REV. A

297X420