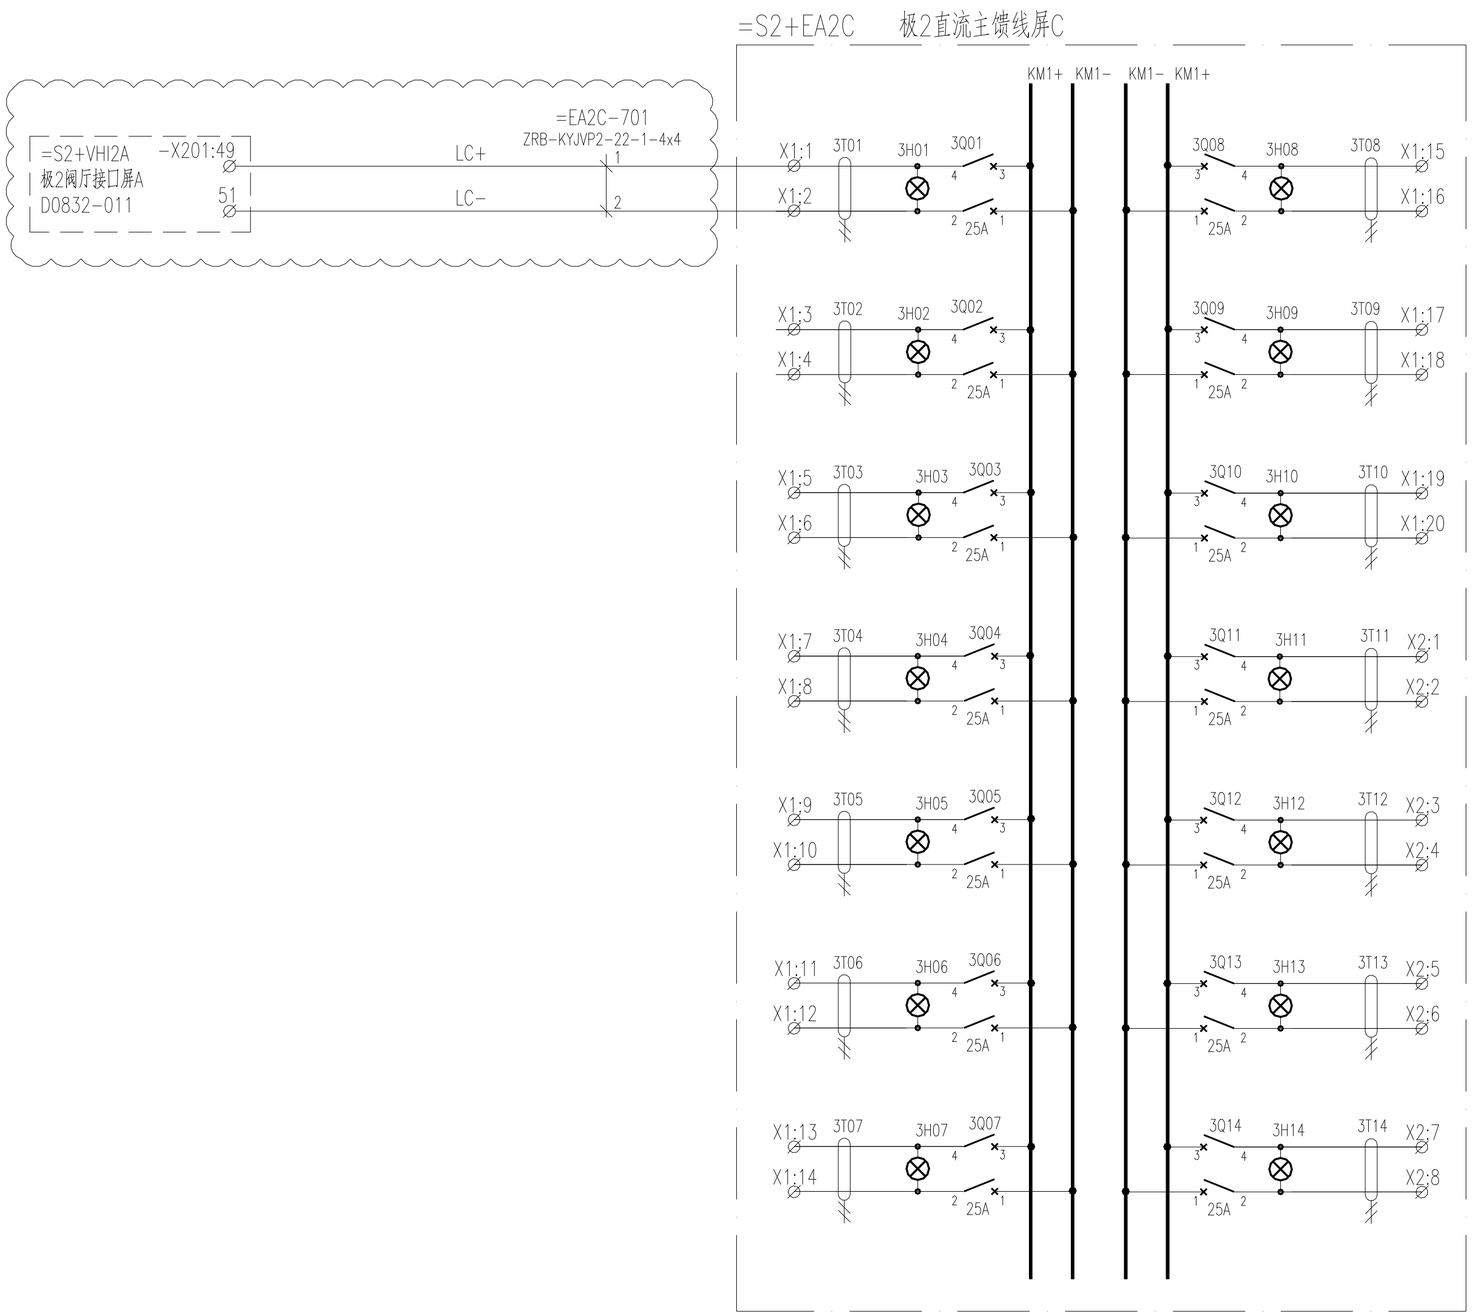

巴基斯坦默蒂亚里—拉合尔±660kV直流输电工程

±660kV HVDC Project from Matiari to Lahore in Pakistan

NATIONAL TRANSMISSION & DESPATCH COMPANY (NTDC) LIMITED PAKISTAN

CONTRACTOR 国家电网 STATE GRID 中国电力技术装备有限公司 CHINA ELECTRIC POWER EQUIPMENT AND TECHNOLOGY CO.,LTD.

SUBCONTRACTOR East China Electric Power Design Institute Co.,Ltd.

拉合尔±660kV换流站

±660kV Lahore Converter Station

设计阶段 PHASE: 施工图 Detail Design

M L H V D C - E N G - E C I - D D - P C - 1 1 3 0 - 0 5 4 A

	姓名 Name	日期 Date
设计 Designed	李坐坐	2020.2.24
校核 Checked	徐勇	2020.2.26
审核 Reviewed		
批准 Approved	王建伟	2020.2.28
比例 Scale		图号 DWG NO.

极2直流主馈线屏C馈线图（一）

DC feeder Circuit 1 of =S2+EA2C

30-B003701S-D1103-054

版本 REV. A

297X420