屏柜功能代号	馈线开关符号	馈线回路名称	开关型式	开关额定电流(A)	电缆型式及截面(mm)	电缆编号	备注
=P1-DPD1	3MCB	=P1.Z1.Z11-Q11.J 极1直流滤波器高压侧隔离开关机构箱 DC220V±	C65H-DC-2P-C25A+SD+OF	25	ZRB-KYJVP2-22-1-4x4	=P1-DPD1-701	
	4MCB	=P1.Z1.Z11-Q11.J 极1直流滤波器高压侧隔离开关机构箱 DC220V±				=P1-DPD1-702	
	5MCB	=P1.Z1.Z11-Q21.J 极1直流滤波器高压侧接地开关机构箱 DC220V±				=P1-DPD1-703	
	6MCB	=P1.Z1.Z11-Q21.J 极1直流滤波器高压侧接地开关机构箱 DC220V±				=P1-DPD1-704	
	7MCB	=P1.Z1.Z12-Q11.J 极1直流滤波器高压侧隔离开关机构箱 DC220V±				=P1-DPD1-705	
	8MCB	=P1.Z1.Z12-Q11.J 极1直流滤波器高压侧隔离开关机构箱 DC220V±				=P1-DPD1-706	
	9MCB	=P1.Z1.Z12-Q21.J 极1直流滤波器高压侧接地开关机构箱 DC220V±				=P1-DPD1-707	
	10MCB	=P1.Z1.Z12-Q21.J 极1直流滤波器高压侧接地开关机构箱 DC220V±				=P1-DPD1-708	
	11MCB	=P1.WP-Q11.J 极1极线隔离开关机构箱 DC220V±				=P1-DPD1-709	
	12MCB	=P1.WP-Q11.J 极1极线隔离开关机构箱 DC220V±				=P1-DPD1-710	
	13MCB	=P1.WP-Q12.J 极1极线隔离开关机构箱 DC220V±				=P1-DPD1-711	
	14MCB	=P1.WP-Q12.J 极1极线隔离开关机构箱 DC220V±				=P1-DPD1-712	
	15MCB	=P1.WP-Q21.J 极1极线接地开关机构箱 DC220V±				=P1-DPD1-713	
	16MCB	=P1.WP-Q21.J 极1极线接地开关机构箱 DC220V±				=P1-DPD1-714	
	17MCB	=P1.WP-Q22.J 极1极线接地开关机构箱 DC220V±				=P1-DPD1-715	
	18MCB	=P1.WP-Q22.J 极1极线接地开关机构箱 DC220V±				=P1-DPD1-716	
	19MCB						备用
	20MCB						备用
	21MCB						备用
	22MCB						备用
	23MCB	=P1.OLM.JB 极1在线监测就地柜 DC220V±				=P1-DPD1-721	
	24MCB						备用
	25MCB						备用
	26MCB						备用
	27MCB						备用
	28MCB						备用
	29MCB						备用
	30MCB						备用
	31MCB						备用
	32MCB						备用
	33MCB						备用
	34MCB		C65H-DC-2P-C40A+SD+OF	40			备用
	35MCB						备用
	36MCB						备用
	37MCB						备用
	38MCB						备用
	39MCB						备用
	40MCB						备用
	41MCB						备用
	42MCB						备用
	43MCB						备用
	44MCB						备用
	45MCB						备用
	46MCB						备用
	47MCB						备用
	48MCB						备用
	49MCB						备用

巴基斯坦默蒂亚里—拉合尔±660kV直流输电工程

±660kV HVDC Project from Matiari to Lahore in Pakistan

NATIONAL TRANSMISSION & DESPATCH COMPANY (NTDC) LIMITED PAKISTAN

CONTRACTOR 国家电网 STATE GRID 中国电力技术装备有限公司 CHINA ELECTRIC POWER EQUIPMENT AND TECHNOLOGY CO.,LTD.

SUBCONTRACTOR East China Electric Power Design Institute Co.,Ltd.

拉合尔±660kV换流站

±660kV Lahore Converter Station

设计阶段 PHASE: 施工图 Detail Design

M L H V D C - E N G - E C I - D D - P C - 1 1 3 0 - 0 7 4 A

	姓名 Name	日期 Date
设计 Designed	李莹莹	2020.2.24
校核 Checked	徐勇	2020.2.26
审核 Reviewed		
批准 Approved	王建伟	2020.2.28

极1直流电源配电箱1馈线表

DC feeder meter for =P1-DPD1

比例 Scale:

图号 DWG NO.: 30-B003701S-D1103-074

版本 REV.: A

297X420

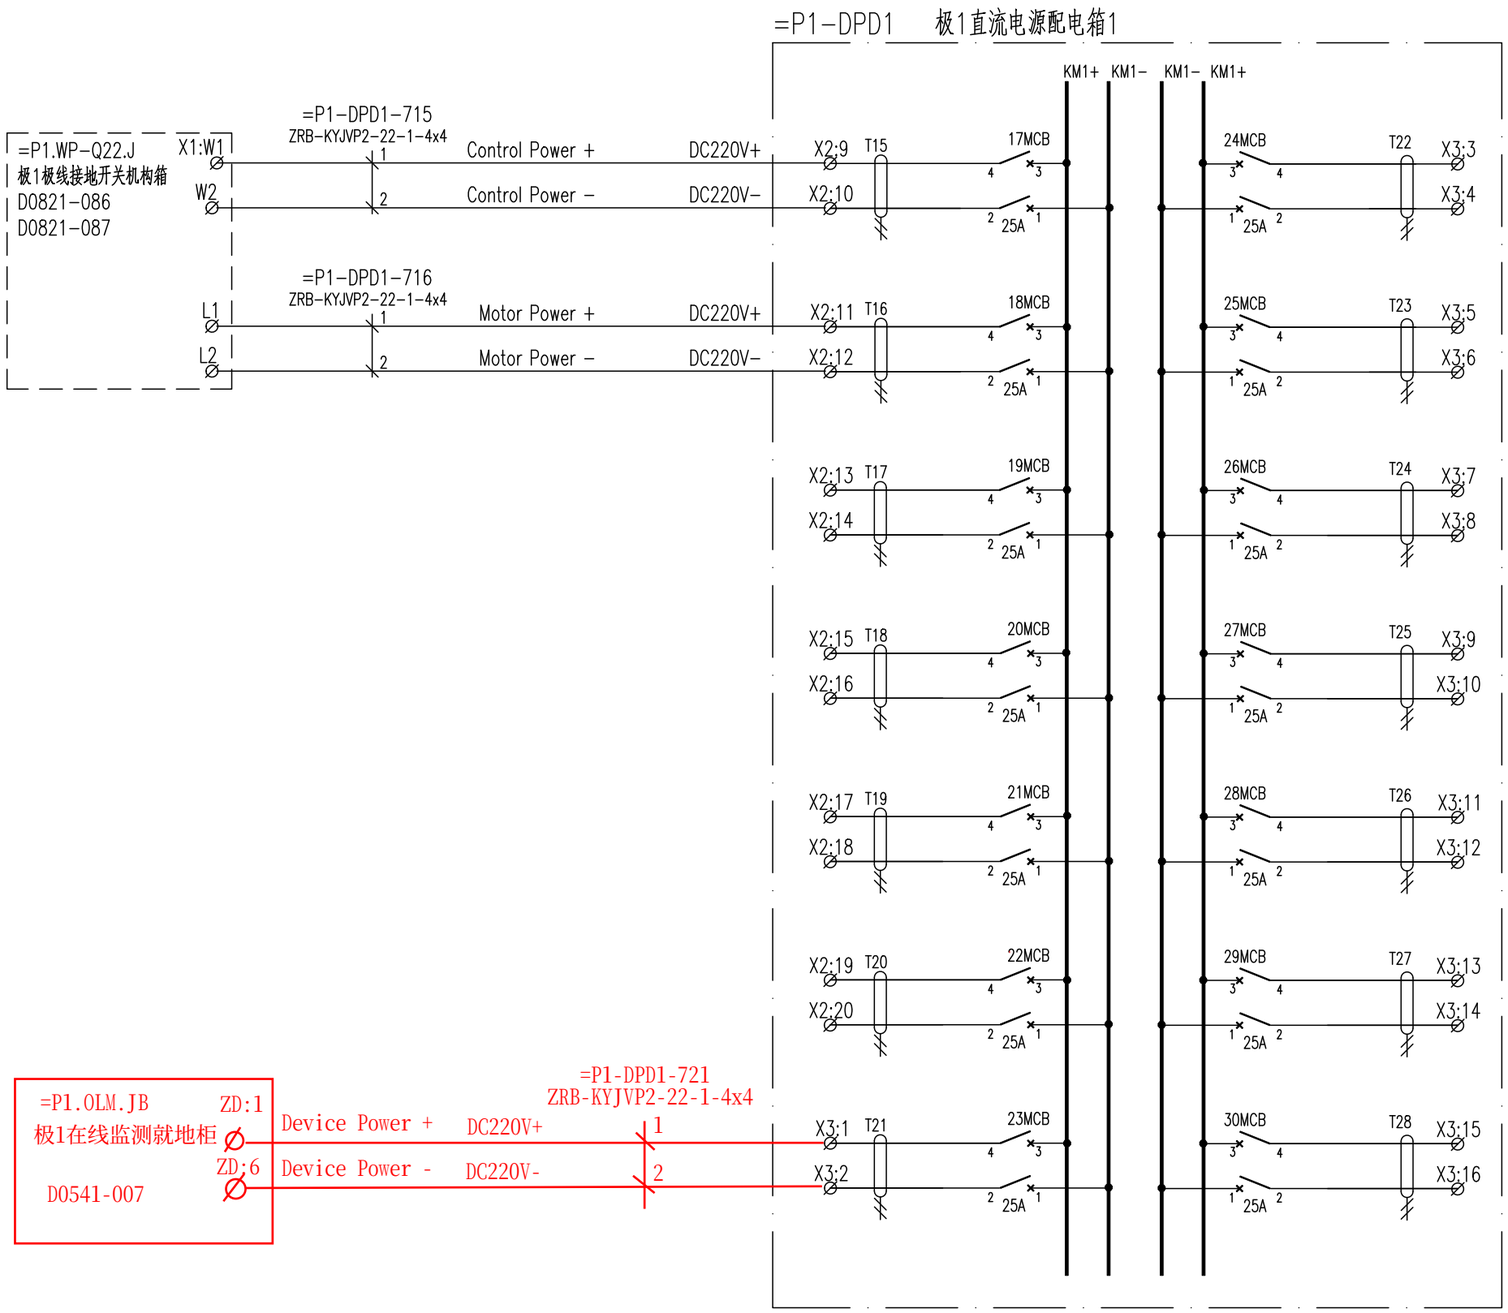

巴基斯坦默蒂亚里—拉合尔±660kV直流输电工程

±660kV HVDC Project from Matiari to Lahore in Pakistan

NATIONAL TRANSMISSION & DESPATCH COMPANY (NTDC) LIMITED PAKISTAN

CONTRACTOR 国家电网 STATE GRID 中国电力技术装备有限公司 CHINA ELECTRIC POWER EQUIPMENT AND TECHNOLOGY CO.,LTD.

SUBCONTRACTOR East China Electric Power Design Institute Co.,Ltd.

拉合尔±660kV换流站

±660kV Lahore Converter Station

设计阶段 PHASE: 施工图 Detail Design

M L H V D C - E N G - E C I - D D - P C - 1 1 3 0 - 0 7 6 A

	姓名 Name	日期 Date
设计 Designed	李莹莹	2020.2.24
校核 Checked	徐勇	2020.2.26
审核 Reviewed		
批准 Approved	王建华	2020.2.28
比例 Scale		图号 DWG NO.

=P1-DPD1馈线图（二）

DC feeder Circuit 2 of =P1-DPD1

30-B003701S-D1103-076

版本 REV. A

297X420

屏柜功能代号	馈线开关符号	馈线回路名称	开关型式	开关额定电流(A)	电缆型式及截面(mm)	电缆编号	备注
=P2-DPD1	3MCB	=P2.Z1.Z11-Q11.J 极2直流滤波器高压侧隔离开关机构箱 DC220V±	C65H-DC-2P-C25A+SD+OF	25	ZRB-KYJVP2-22-1-4x4	=P2-DPD1-701	
	4MCB	=P2.Z1.Z11-Q11.J 极2直流滤波器高压侧隔离开关机构箱 DC220V±				=P2-DPD1-702	
	5MCB	=P2.Z1.Z11-Q21.J 极2直流滤波器高压侧接地开关机构箱 DC220V±				=P2-DPD1-703	
	6MCB	=P2.Z1.Z11-Q21.J 极2直流滤波器高压侧接地开关机构箱 DC220V±				=P2-DPD1-704	
	7MCB	=P2.Z1.Z12-Q11.J 极2直流滤波器高压侧隔离开关机构箱 DC220V±				=P2-DPD1-705	
	8MCB	=P2.Z1.Z12-Q11.J 极2直流滤波器高压侧隔离开关机构箱 DC220V±				=P2-DPD1-706	
	9MCB	=P2.Z1.Z12-Q21.J 极2直流滤波器高压侧接地开关机构箱 DC220V±				=P2-DPD1-707	
	10MCB	=P2.Z1.Z12-Q21.J 极2直流滤波器高压侧接地开关机构箱 DC220V±				=P2-DPD1-708	
	11MCB	=P2.WP-Q11.J 极2极线隔离开关机构箱 DC220V±				=P2-DPD1-709	
	12MCB	=P2.WP-Q11.J 极2极线隔离开关机构箱 DC220V±				=P2-DPD1-710	
	13MCB	=P2.WP-Q12.J 极2极线隔离开关机构箱 DC220V±				=P2-DPD1-711	
	14MCB	=P2.WP-Q12.J 极2极线隔离开关机构箱 DC220V±				=P2-DPD1-712	
	15MCB	=P2.WP-Q21.J 极2极线接地开关机构箱 DC220V±				=P2-DPD1-713	
	16MCB	=P2.WP-Q21.J 极2极线接地开关机构箱 DC220V±				=P2-DPD1-714	
	17MCB	=P2.WP-Q22.J 极2极线接地开关机构箱 DC220V±				=P2-DPD1-715	
	18MCB	=P2.WP-Q22.J 极2极线接地开关机构箱 DC220V±				=P2-DPD1-716	
	19MCB						备用
	20MCB						备用
	21MCB						备用
	22MCB						备用
	23MCB	=P2.OLM.JB 极2在线监测就地柜 DC220V±				=P2-DPD1-721	
	24MCB						备用
	25MCB						备用
	26MCB						备用
	27MCB						备用
	28MCB						备用
	29MCB						备用
	30MCB						备用
	31MCB						备用
	32MCB						备用
	33MCB						备用
	34MCB		C65H-DC-2P-C40A+SD+OF	40			备用
	35MCB						备用
	36MCB						备用
	37MCB						备用
	38MCB						备用
	39MCB						备用
	40MCB						备用
	41MCB						备用
	42MCB						备用
	43MCB						备用
	44MCB						备用
	45MCB						备用
	46MCB						备用
	47MCB						备用
	48MCB						备用
	49MCB						备用

巴基斯坦默蒂亚里—拉合尔±660kV直流输电工程

±660kV HVDC Project from Matiari to Lahore in Pakistan

NATIONAL TRANSMISSION & DESPATCH COMPANY (NTDC) LIMITED PAKISTAN

CONTRACTOR 国家电网 STATE GRID 中国电力技术装备有限公司 CHINA ELECTRIC POWER EQUIPMENT AND TECHNOLOGY CO.,LTD.

SUBCONTRACTOR East China Electric Power Design Institute Co.,Ltd.

拉合尔±660kV换流站

±660kV Lahore Converter Station

设计阶段 PHASE: 施工图 Detail Design

M L H V D C - E N G - E C I - D D - P C - 1 1 3 0 - 0 8 4 A

	姓名 Name	日期 Date
设计 Designed	李莹莹	2020.2.24
校核 Checked	徐勇	2020.2.26
审核 Reviewed		
批准 Approved	王建伟	2020.2.28

极2直流电源配电箱1馈线表

DC feeder meter for =P2-DPD1

比例 Scale:

图号 DWG NO.: 30-B003701S-D1103-084

版本 REV.: A

297X420

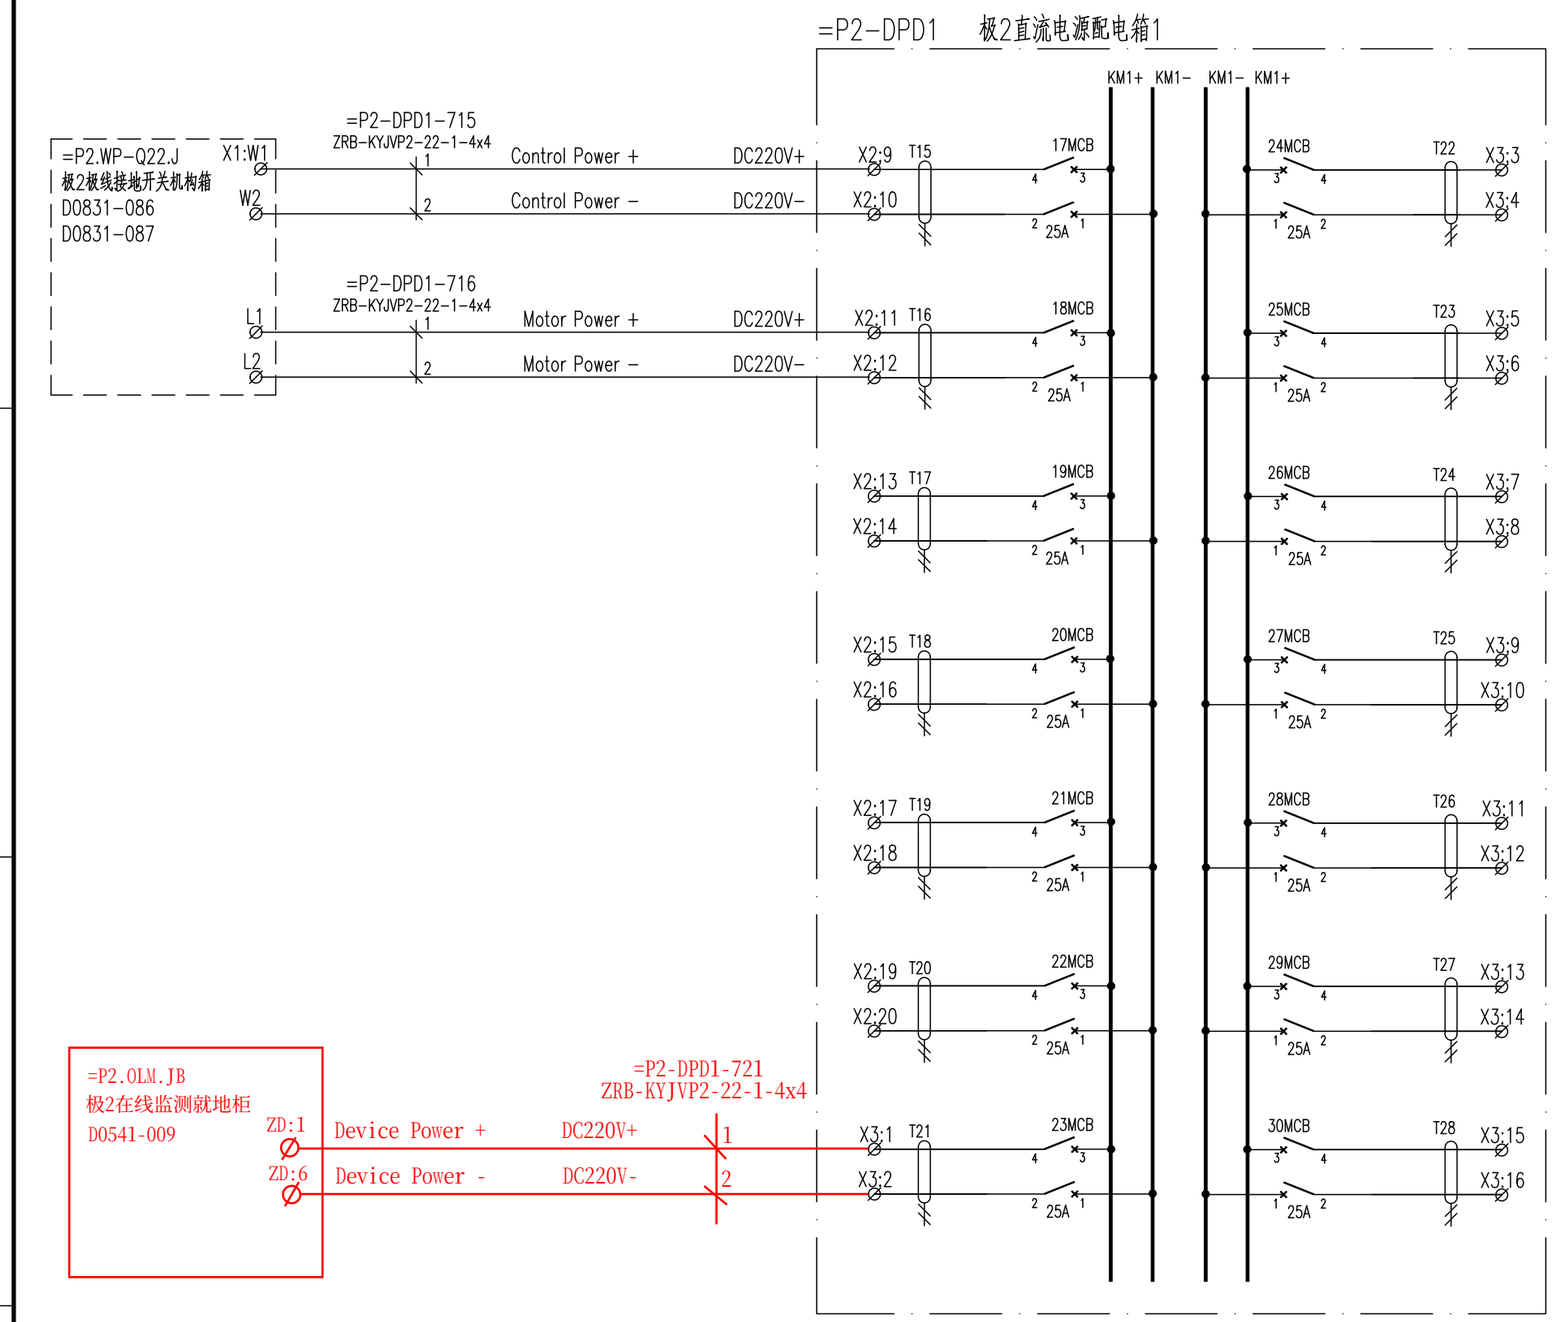

巴基斯坦默蒂亚里—拉合尔±660kV直流输电工程

±660kV HVDC Project from Matiari to Lahore in Pakistan

NATIONAL TRANSMISSION & DESPATCH COMPANY (NTDC) LIMITED PAKISTAN

CONTRACTOR 国家电网 STATE GRID 中国电力技术装备有限公司 CHINA ELECTRIC POWER EQUIPMENT AND TECHNOLOGY CO.,LTD.

SUBCONTRACTOR East China Electric Power Design Institute Co.,Ltd.

拉合尔±660kV换流站

±660kV Lahore Converter Station

设计阶段 PHASE: 施工图 Detail Design

M L H V D C - E N G - E C I - D D - P C - 1 1 3 0 - 0 8 6 A

	姓名 Name	日期 Date
设计 Designed	李莹莹	2020.2.24
校核 Checked	徐勇	2020.2.26
审核 Reviewed		
批准 Approved	王建伟	2020.2.28
比例 Scale		图号 DWG NO.

=P2-DPD1馈线图（二）

DC feeder Circuit 2 of =P2-DPD1

30-B003701S-D1103-086

版本 REV. A

297X420

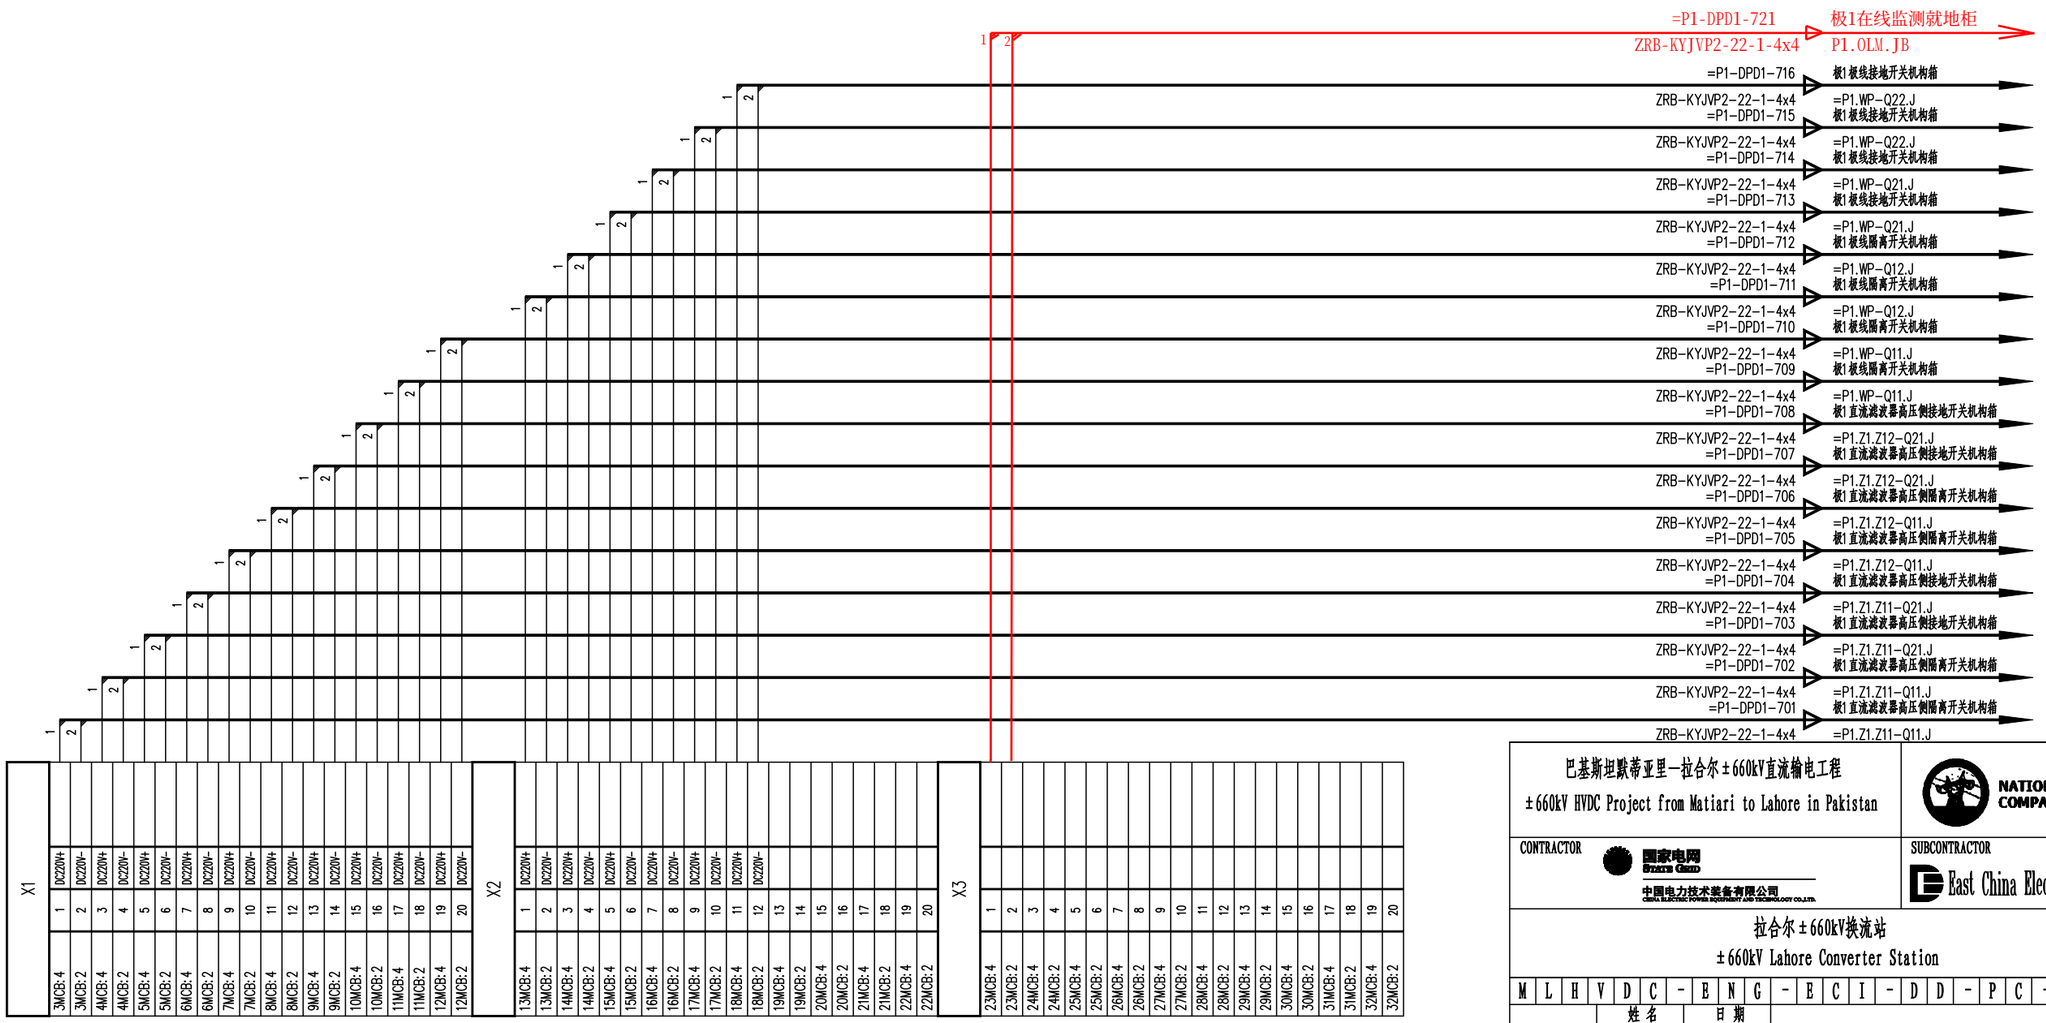

巴基斯坦默蒂亚里—拉合尔±660kV直流输电工程

±660kV HVDC Project from Matiari to Lahore in Pakistan

NATIONAL TRANSMISSION & DESPATCH COMPANY (NTDC) LIMITED PAKISTAN

CONTRACTOR 国家电网 STATE GRID 中国电力技术装备有限公司 CHINA ELECTRIC POWER EQUIPMENT AND TECHNOLOGY CO.,LTD.

SUBCONTRACTOR East China Electric Power Design Institute Co.,Ltd.

拉合尔±660kV换流站

±660kV Lahore Converter Station

设计阶段 PHASE: 施工图 Detail Design

M L H V D C - E N G - E C I - D D - P C - 1 1 0 3 - 1 0 9 A

	姓名 Name	日期 Date
设计 Designed	李坐坐	2020.2.24
校核 Checked	徐勇	2020.2.26
审核 Reviewed		
批准 Approved	王建鹏	2020.2.28

=P1-DPD1端子排图（一）

Terminal Diagram 1 =P1-DPD1

比例 Scale

图号 DWG NO. 30-B003701S-D1103-109

版本 REV. A

420X594

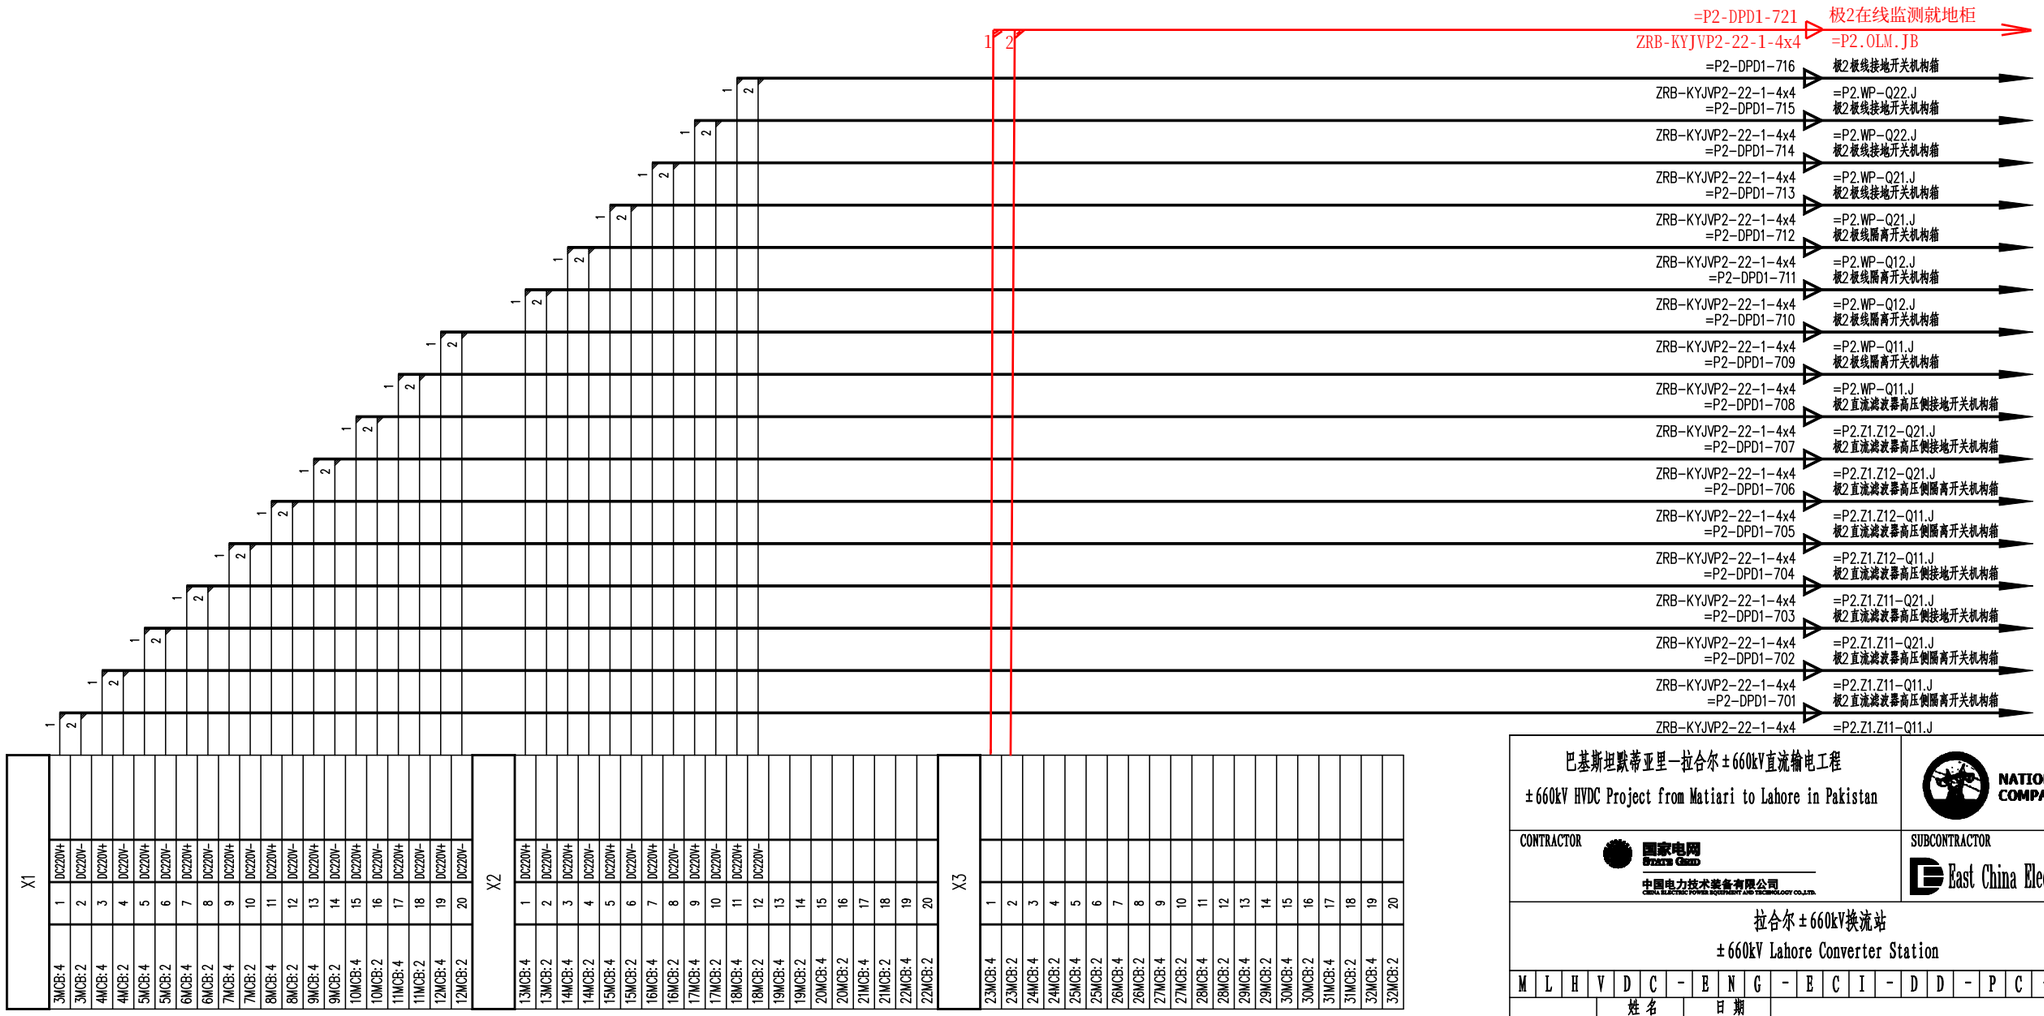

巴基斯坦默蒂亚里—拉合尔±660kV直流输电工程

±660kV HVDC Project from Matiari to Lahore in Pakistan

NATIONAL TRANSMISSION & DESPATCH COMPANY (NTDC) LIMITED PAKISTAN

CONTRACTOR 国家电网 STATE GRID 中国电力技术装备有限公司 CHINA ELECTRIC POWER EQUIPMENT AND TECHNOLOGY CO.,LTD.

SUBCONTRACTOR East China Electric Power Design Institute Co.,Ltd.

拉合尔±660kV换流站

±660kV Lahore Converter Station

设计阶段 PHASE: 施工图 Detail Design

M L H V D C - E N G - E C I - D D - P C - 1 1 0 3 - 1 1 3 A

	姓名 Name	日期 Date
设计 Designed	李坚坚	2020.2.24
校核 Checked	徐勇	2020.2.26
审核 Reviewed		
批准 Approved	王建彬	2020.2.28

=P2-DPD1端子排图（一）

Terminal Diagram 1 =P2-DPD1

比例 Scale

图号 DWG NO. 30-B003701S-D1103-113

版本 REV. A

420X594