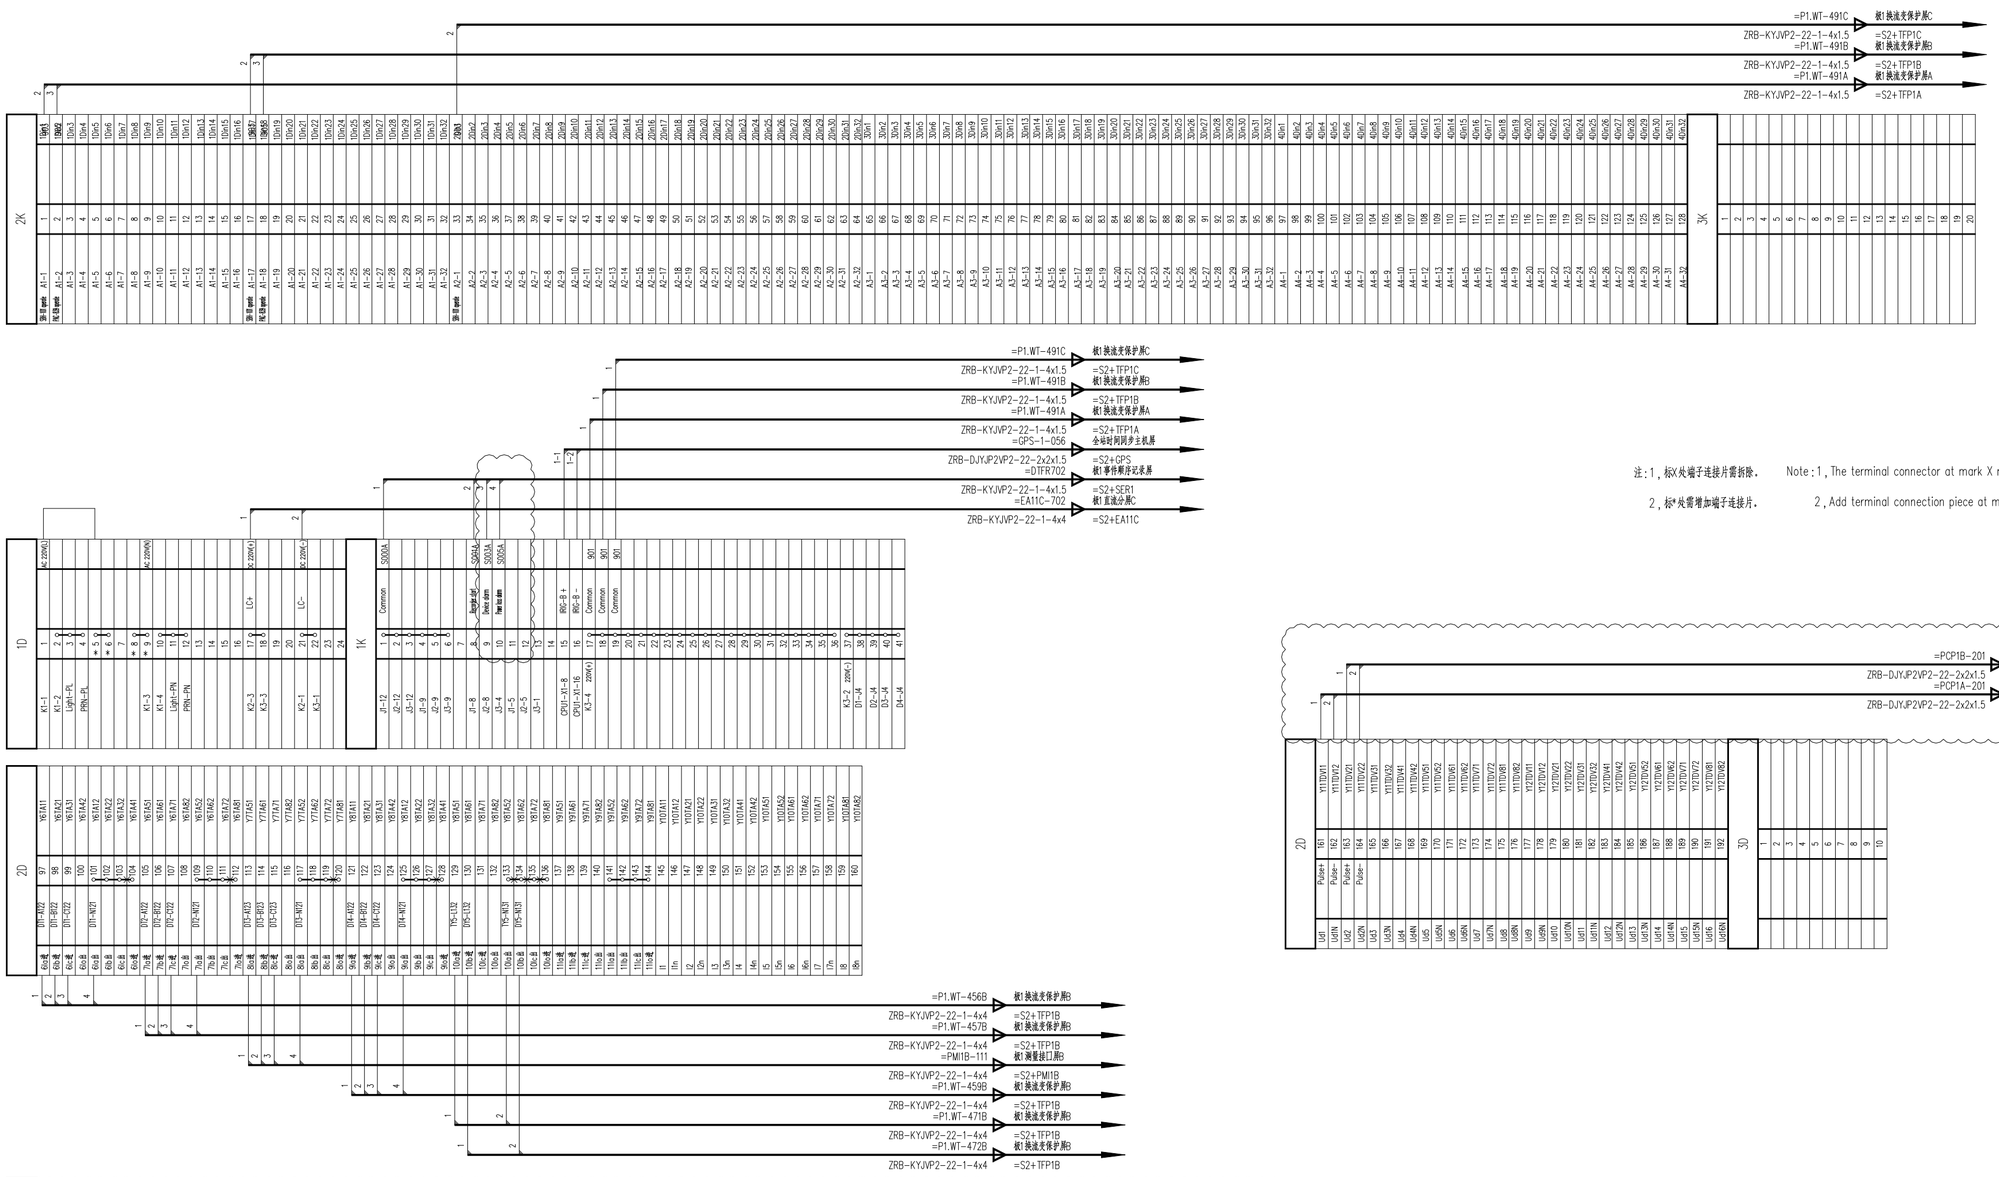


注：1，标X处端子连接片需拆除。

2，标*处需增加端子连接片。

Note：1，The terminal connector at mark X needs to be removed.

2，Add terminal connection piece at mark *.

巴基斯坦默蒂亚里—拉合尔±660kV直流输电工程

±660kV HVDC Project from Matiari to Lahore in Pakistan

NATIONAL TRANSMISSION & DESPATCH COMPANY (NTDC) LIMITED PAKISTAN

CONTRACTOR 国家电网 STATE GRID 中国电力技术装备有限公司 CHINA ELECTRIC EQUIPMENT GROUP CORPORATION

SUBCONTRACTOR East China Electric Power Design Institute Co.,Ltd.

拉合尔±660kV换流站

±660kV Lahore Converter Station

设计阶段 PHASE：施工图 Detail Design

MLHVDC-ENG-ECI-DD-PC-080 1-039 A

| | 姓名 Name | 日期 Date |
|---|---|---|
| 设计 Designed | 王建辉 | 2020.02.14 |
| 校核 Checked | 孙勇 | 2020.02.18 |
| 审核 Reviewed | 陈旭 | 2020.02.24 |
| 批准 Approved | 李钦雅 | 2020.02.27 |

极1换流变故障录波器屏端子排接线图（DTFR12）

Terminal block diagram(S2+DTFR12)

比例 Scale：

图号 DWG NO.：30-B003701S-D0801-039

版本 REV.：A

594X841