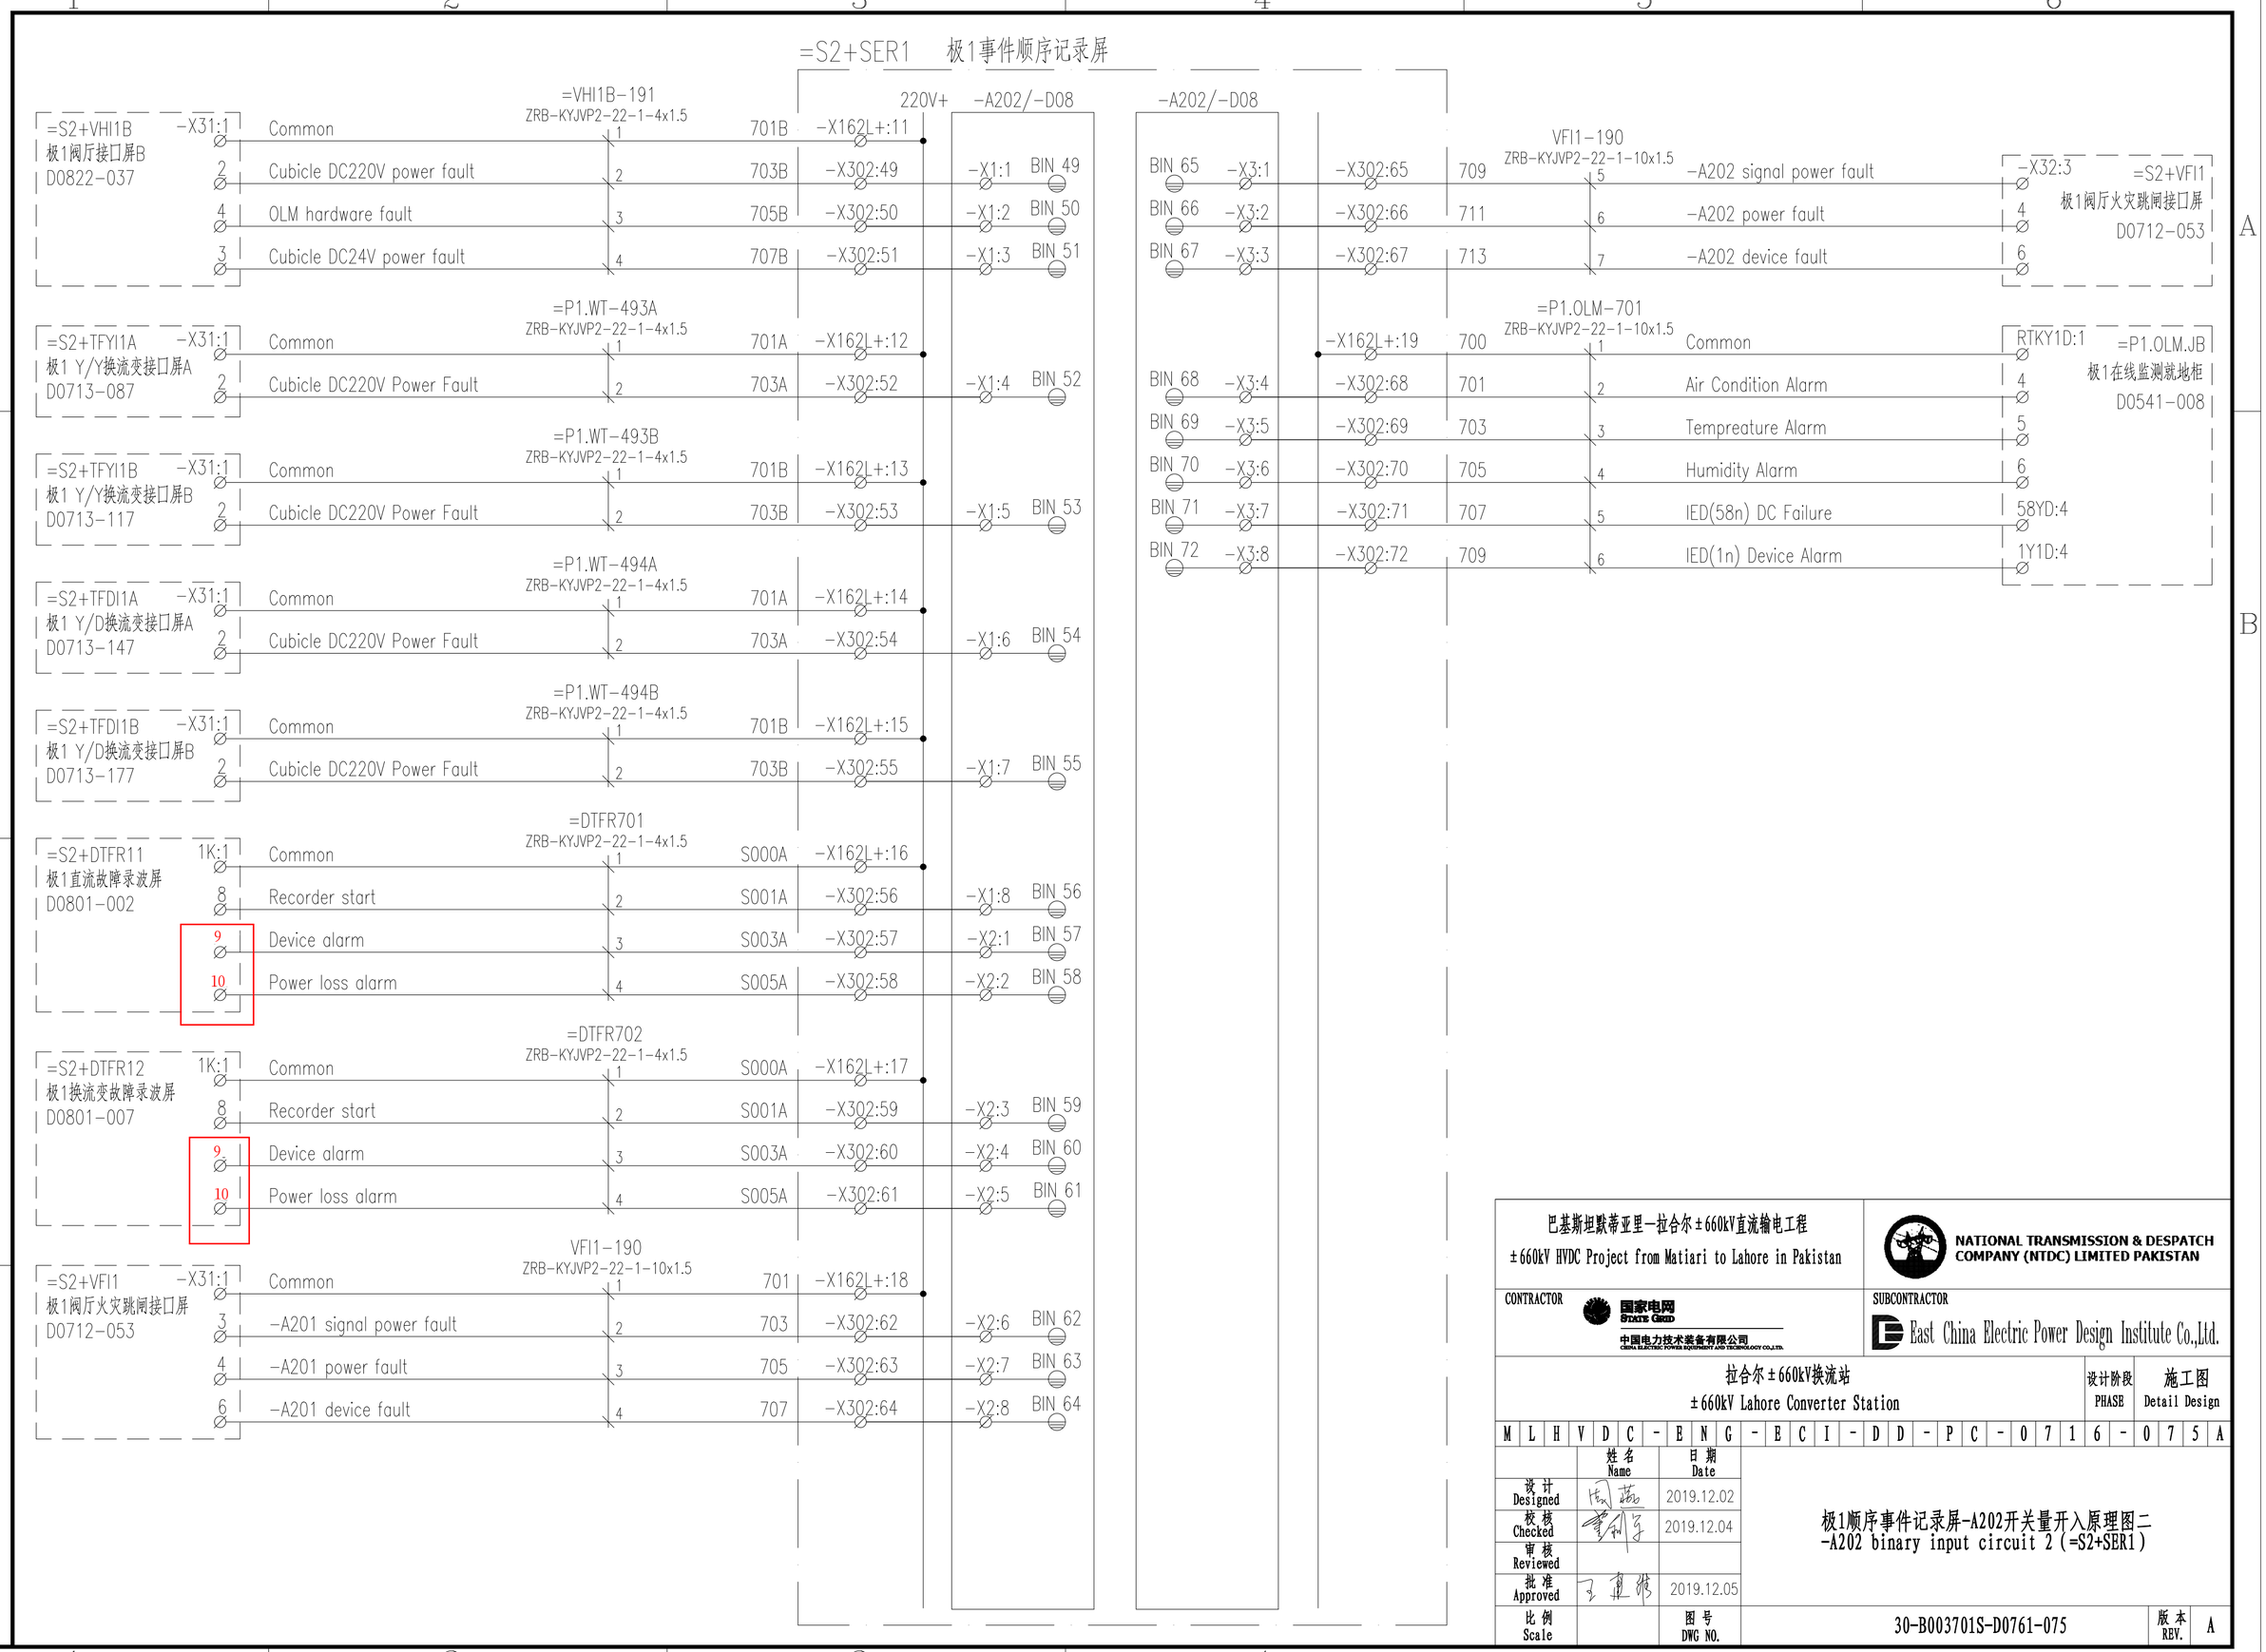

巴基斯坦默蒂亚里—拉合尔±660kV直流输电工程

±660kV HVDC Project from Matiari to Lahore in Pakistan

NATIONAL TRANSMISSION & DESPATCH COMPANY (NTDC) LIMITED PAKISTAN

CONTRACTOR 国家电网 STATE GRID 中国电力技术装备有限公司 CHINA ELECTRIC POWER EQUIPMENT AND TECHNOLOGY CO.,LTD.

SUBCONTRACTOR East China Electric Power Design Institute Co.,Ltd.

拉合尔±660kV换流站

±660kV Lahore Converter Station

设计阶段 PHASE: 施工图 Detail Design

M L H V D C - E N G - E C I - D D - P C - 0 7 1 6 - 0 7 5 A

	姓名 Name	日期 Date
设计 Designed	杨蕊	2019.12.02
校核 Checked	李利宇	2019.12.04
审核 Reviewed		
批准 Approved	王真雅	2019.12.05
比例 Scale		图号 DWG NO.

极1顺序事件记录屏-A202开关量开入原理图二

-A202 binary input circuit 2 (=S2+SER1)

30-B003701S-D0761-075

版本 REV. A

297X420

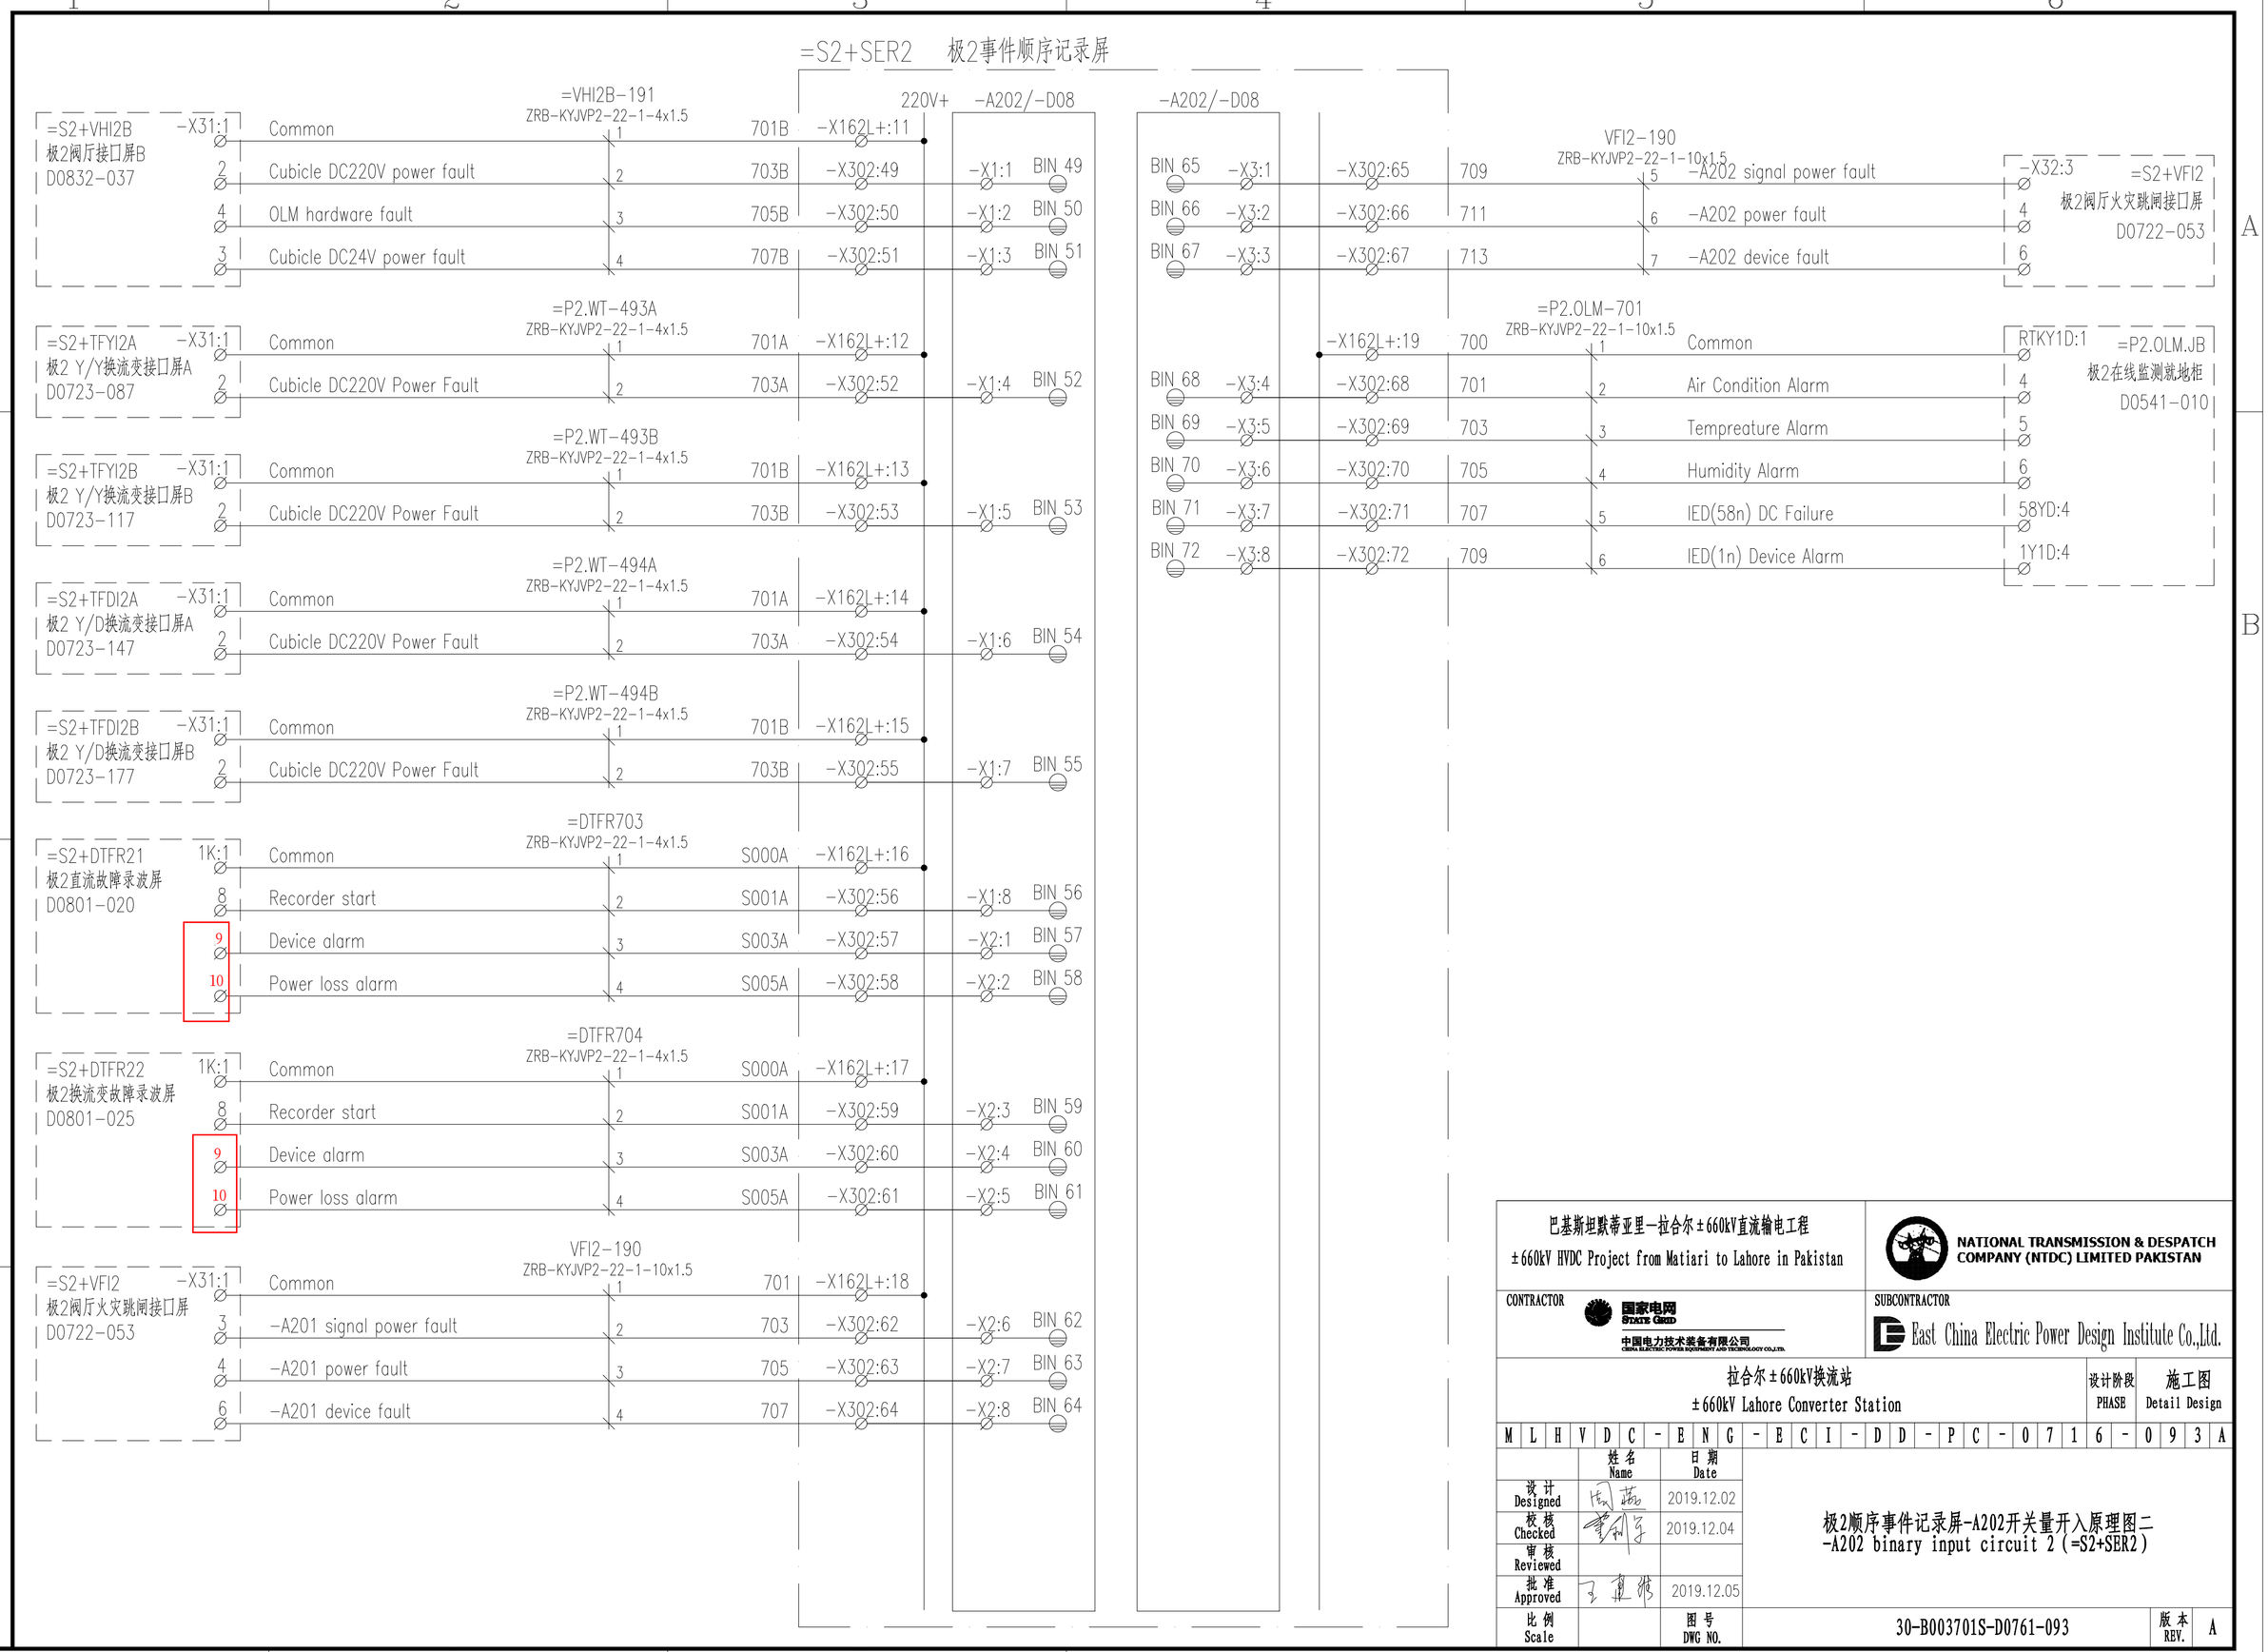

巴基斯坦默蒂亚里—拉合尔±660kV直流输电工程

±660kV HVDC Project from Matiari to Lahore in Pakistan

NATIONAL TRANSMISSION & DESPATCH COMPANY (NTDC) LIMITED PAKISTAN

CONTRACTOR 国家电网 STATE GRID 中国电力技术装备有限公司 CHINA ELECTRIC POWER EQUIPMENT AND TECHNOLOGY CO.,LTD.

SUBCONTRACTOR East China Electric Power Design Institute Co.,Ltd.

拉合尔±660kV换流站

±660kV Lahore Converter Station

设计阶段 PHASE: 施工图 Detail Design

M L H V D C - E N G - E C I - D D - P C - 0 7 1 6 - 0 9 3 A

	姓名 Name	日期 Date
设计 Designed	陈蕴	2019.12.02
校核 Checked	李利宇	2019.12.04
审核 Reviewed		
批准 Approved	王建华	2019.12.05
比例 Scale		图号 DWG NO.

极2顺序事件记录屏-A202开关量开入原理图二

-A202 binary input circuit 2 (=S2+SER2)

30-B003701S-D0761-093

版本 REV. A

297X420