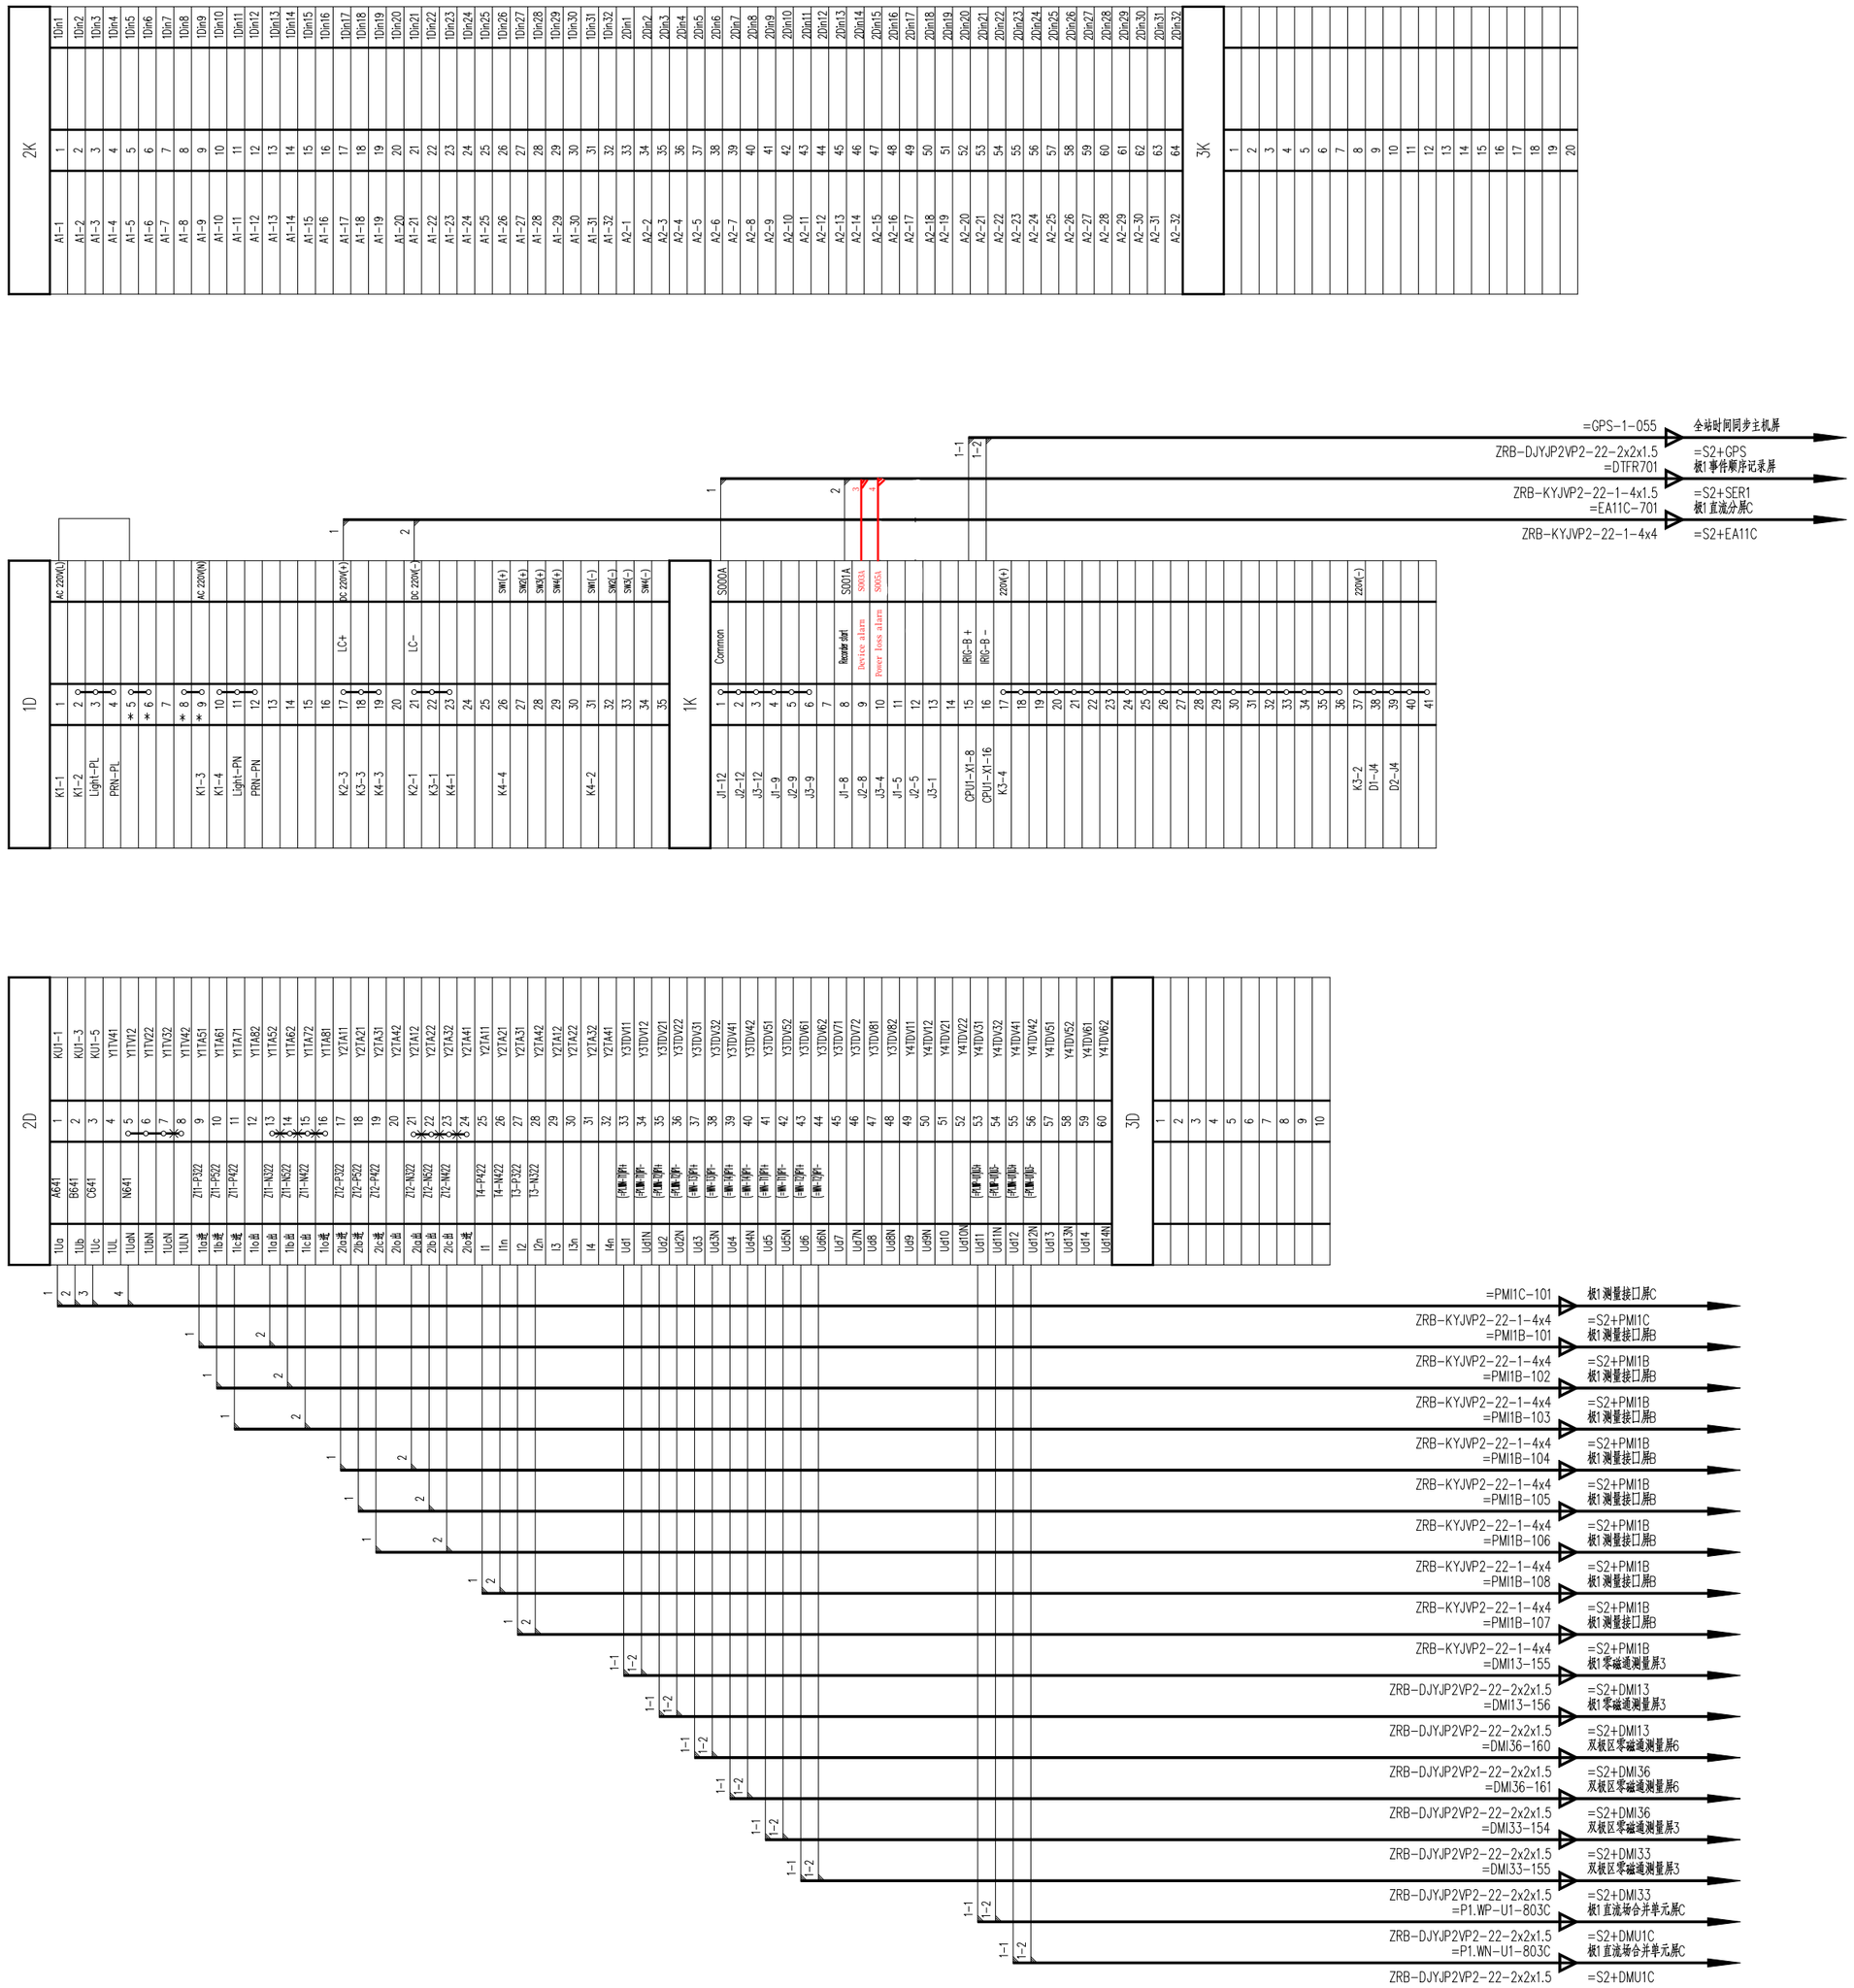

注:1,标X处端子连接片需拆除。

2,标*处需增加端子连接片。

Note:1,The terminal connector at mark X needs to be removed.

2,Add terminal connection piece at mark *.

巴基斯坦默蒂亚里—拉合尔±660kV直流输电工程

±660kV HVDC Project from Matiari to Lahore in Pakistan

NATIONAL TRANSMISSION & DESPATCH COMPANY (NTDC) LIMITED PAKISTAN

CONTRACTOR 国家电网 STATE GRID 中国电力技术装备有限公司 CHINA ELECTRIC POWER EQUIPMENT AND TECHNOLOGY CO.,LTD.

SUBCONTRACTOR East China Electric Power Design Institute Co.,Ltd.

拉合尔±660kV换流站

±660kV Lahore Converter Station

设计阶段 PHASE: 施工图 Detail Design

M L H V D C - E N G - E C I - D D - P C - 0 8 0 1 - 0 3 8 A

	姓名 Name	日期 Date
设计 Designed	王建辉	2020.02.14
校核 Checked	徐勇	2020.02.18
审核 Reviewed	陈旭	2020.02.24
批准 Approved	李钦淮	2020.02.27

极1直流故障录波器端子排接线图 (DTFR11)

Terminal block diagram(S2+DTFR11)

比例 Scale:

图号 DWG NO.: 30-B003701S-D0801-038

版本 REV.: A

594X841

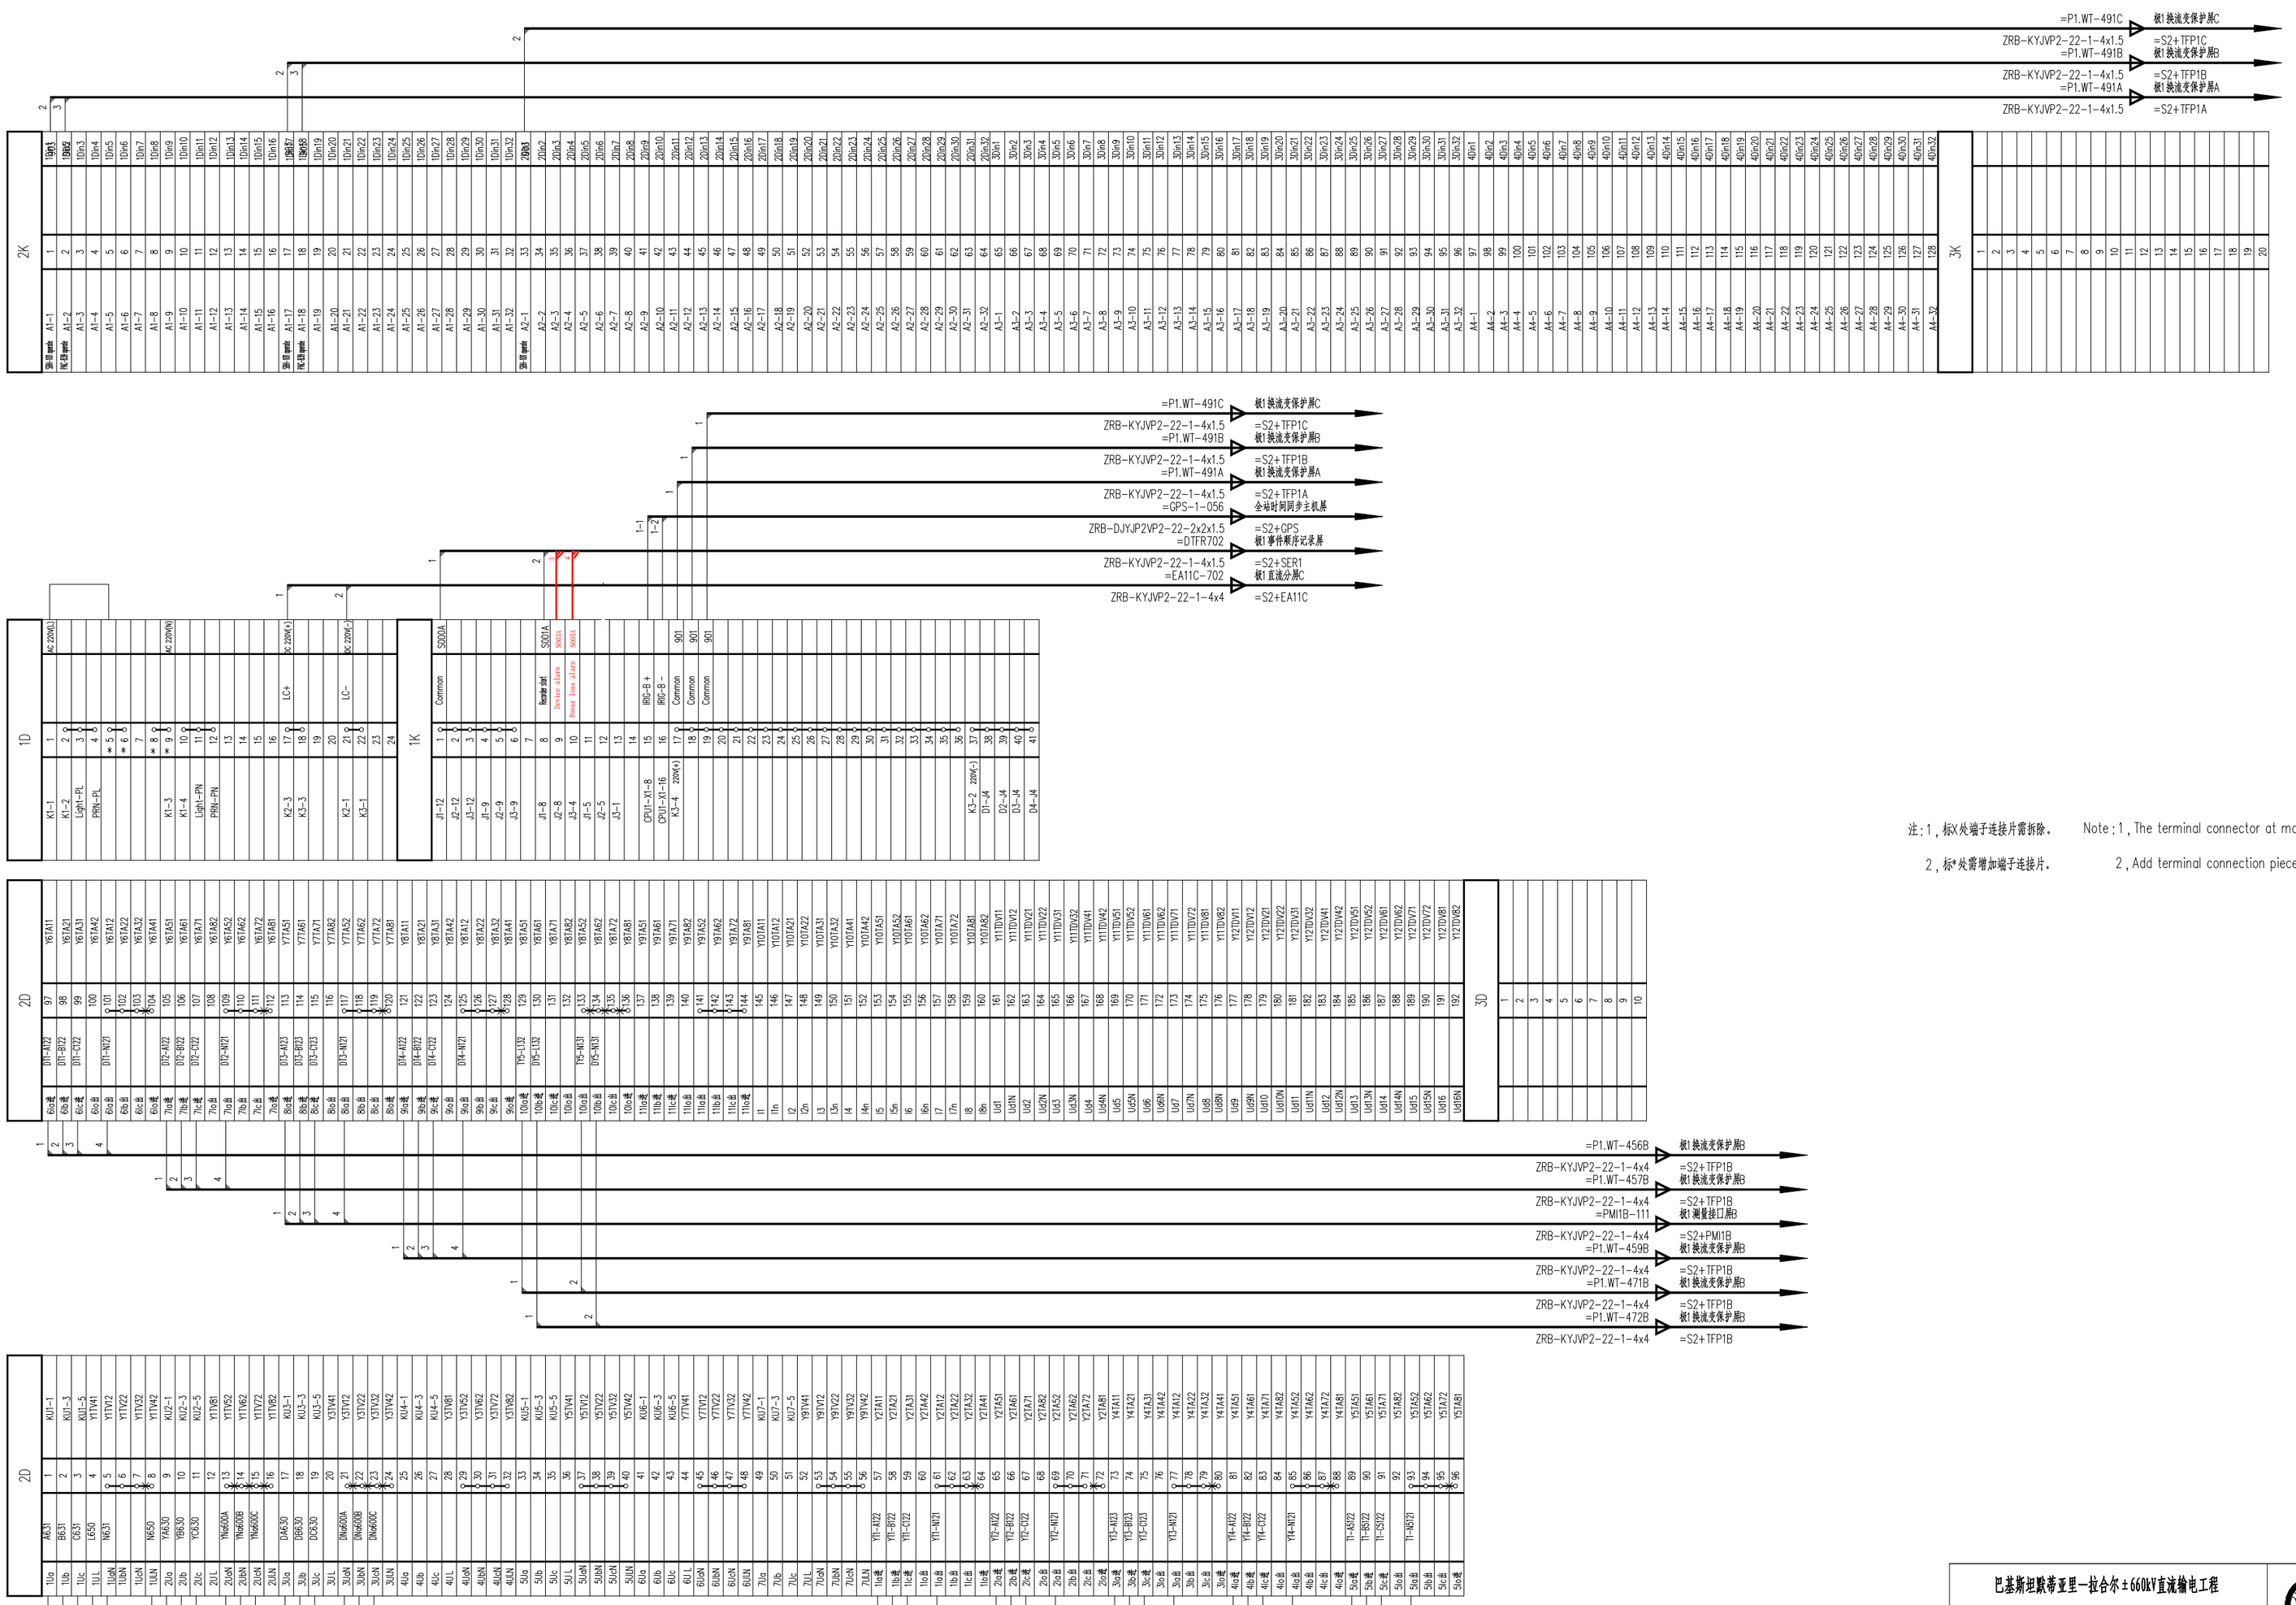

注：1，标X处端子连接片需拆除。 Note：1，The terminal connector at mark X needs to be removed.

2，标*处需增加端子连接片。 2，Add terminal connection piece at mark *.

巴基斯坦默蒂亚里—拉合尔±660kV直流输电工程

±660kV HVDC Project from Matiari to Lahore in Pakistan

NATIONAL TRANSMISSION & DESPATCH COMPANY (NTDC) LIMITED PAKISTAN

CONTRACTOR 国家电网 STATE GRID 中国电力技术装备有限公司 CHINA ELECTRIC POWER EQUIPMENT AND TECHNOLOGY CO.,LTD.

SUBCONTRACTOR East China Electric Power Design Institute Co.,Ltd.

拉合尔±660kV换流站

±660kV Lahore Converter Station

设计阶段 PHASE：施工图 Detail Design

M L H V D C - E N G - E C I - D D - P C - 0 8 0 1 - 0 3 9 A

	姓名 Name	日期 Date
设计 Designed	子建辉	2020.02.14
校核 Checked	徐勇	2020.02.18
审核 Reviewed	陈旭	2020.02.24
批准 Approved	李长胜	2020.02.27

极1换流变故障录波器屏端子排接线图（DTFR12）

Terminal block diagram(S2+DTFR12)

比例 Scale | 图号 DWG NO. 30-B003701S-D0801-039 | 版本 REV. A

594X841

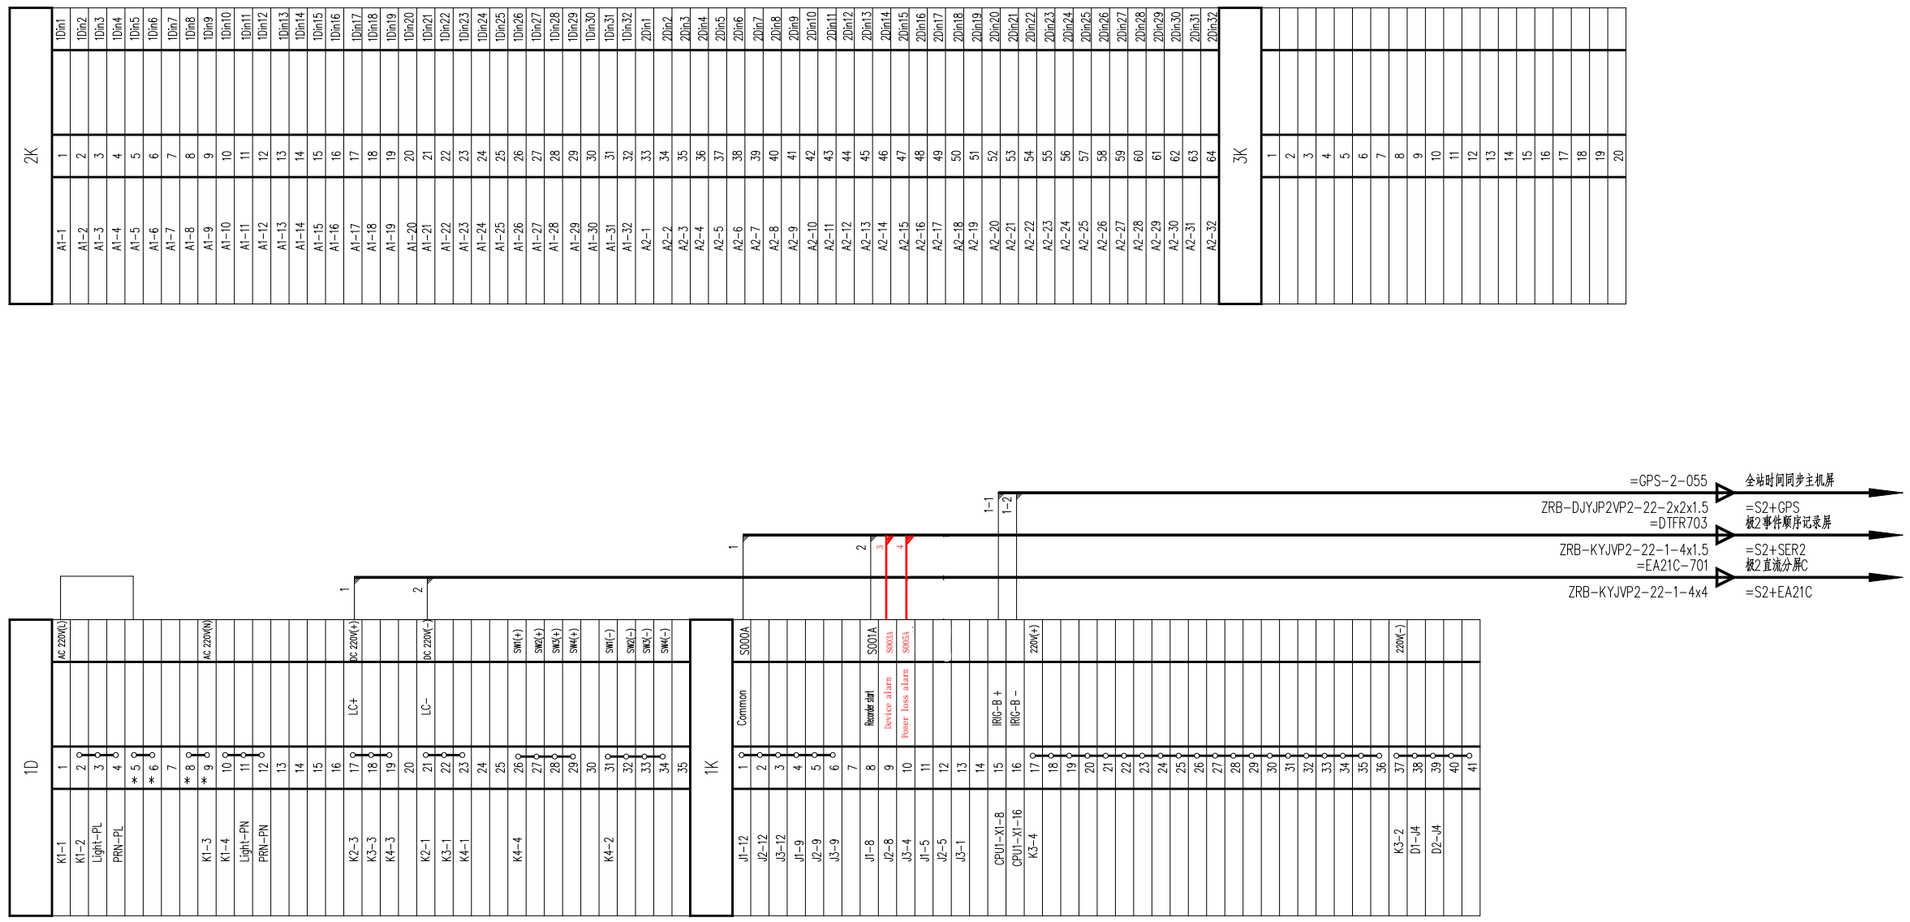

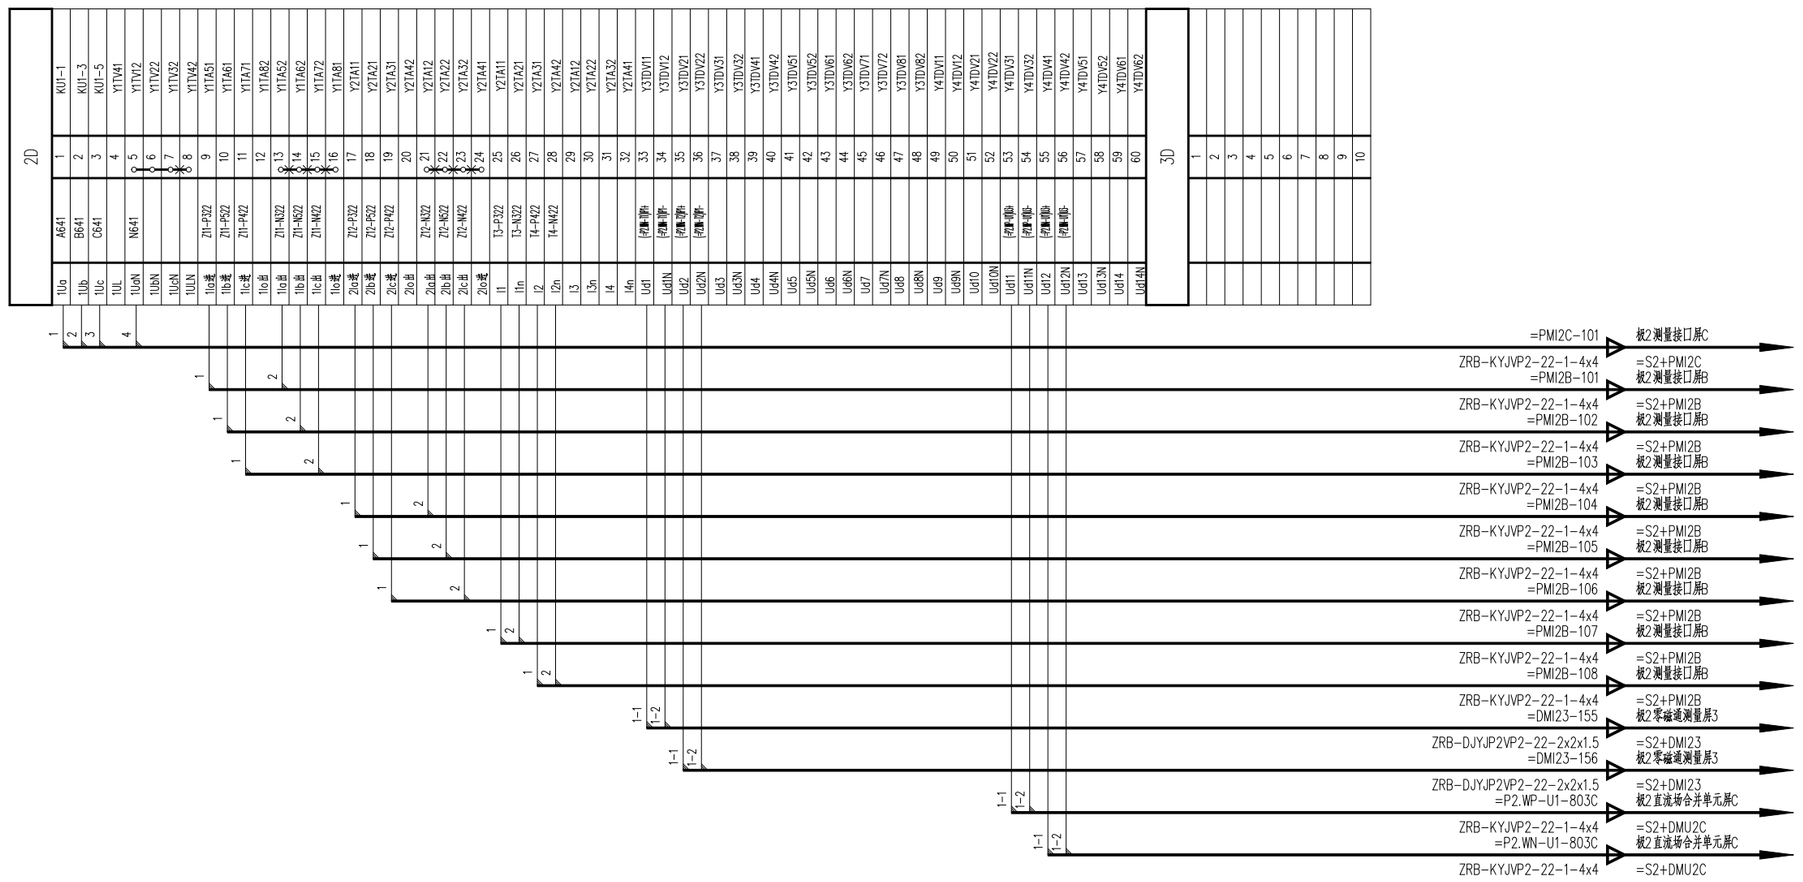

注：1，标X处端子连接片需拆除。

2，标*处需增加端子连接片。

Note：1，The terminal connector at mark X needs to be removed.

2，Add terminal connection piece at mark *.

巴基斯坦默蒂亚里—拉合尔±660kV直流输电工程

±660kV HVDC Project from Matiari to Lahore in Pakistan

NATIONAL TRANSMISSION & DESPATCH COMPANY (NTDC) LIMITED PAKISTAN

CONTRACTOR 国家电网 STATE GRID 中国电力技术装备有限公司 CHINA ELECTRIC POWER TECHNOLOGY EQUIPMENT CO.,LTD.

SUBCONTRACTOR East China Electric Power Design Institute Co.,Ltd.

拉合尔±660kV换流站

±660kV Lahore Converter Station

设计阶段 PHASE：施工图 Detail Design

M L H V D C - E N G - E C I - D D - P C - 0 8 0 1 - 0 4 0 A

	姓名 Name	日期 Date
设计 Designed	王建辉	2020.02.14
校核 Checked	徐勇	2020.02.18
审核 Reviewed	陈旭	2020.02.24
批准 Approved	李长胜	2020.02.27

极2直流故障录波器端子排接线图（DTFR21）

Terminal block diagram(S2+DTFR21)

比例 Scale：

图号 DWG NO.：30-B003701S-D0801-040

版本 REV.：A

594X841

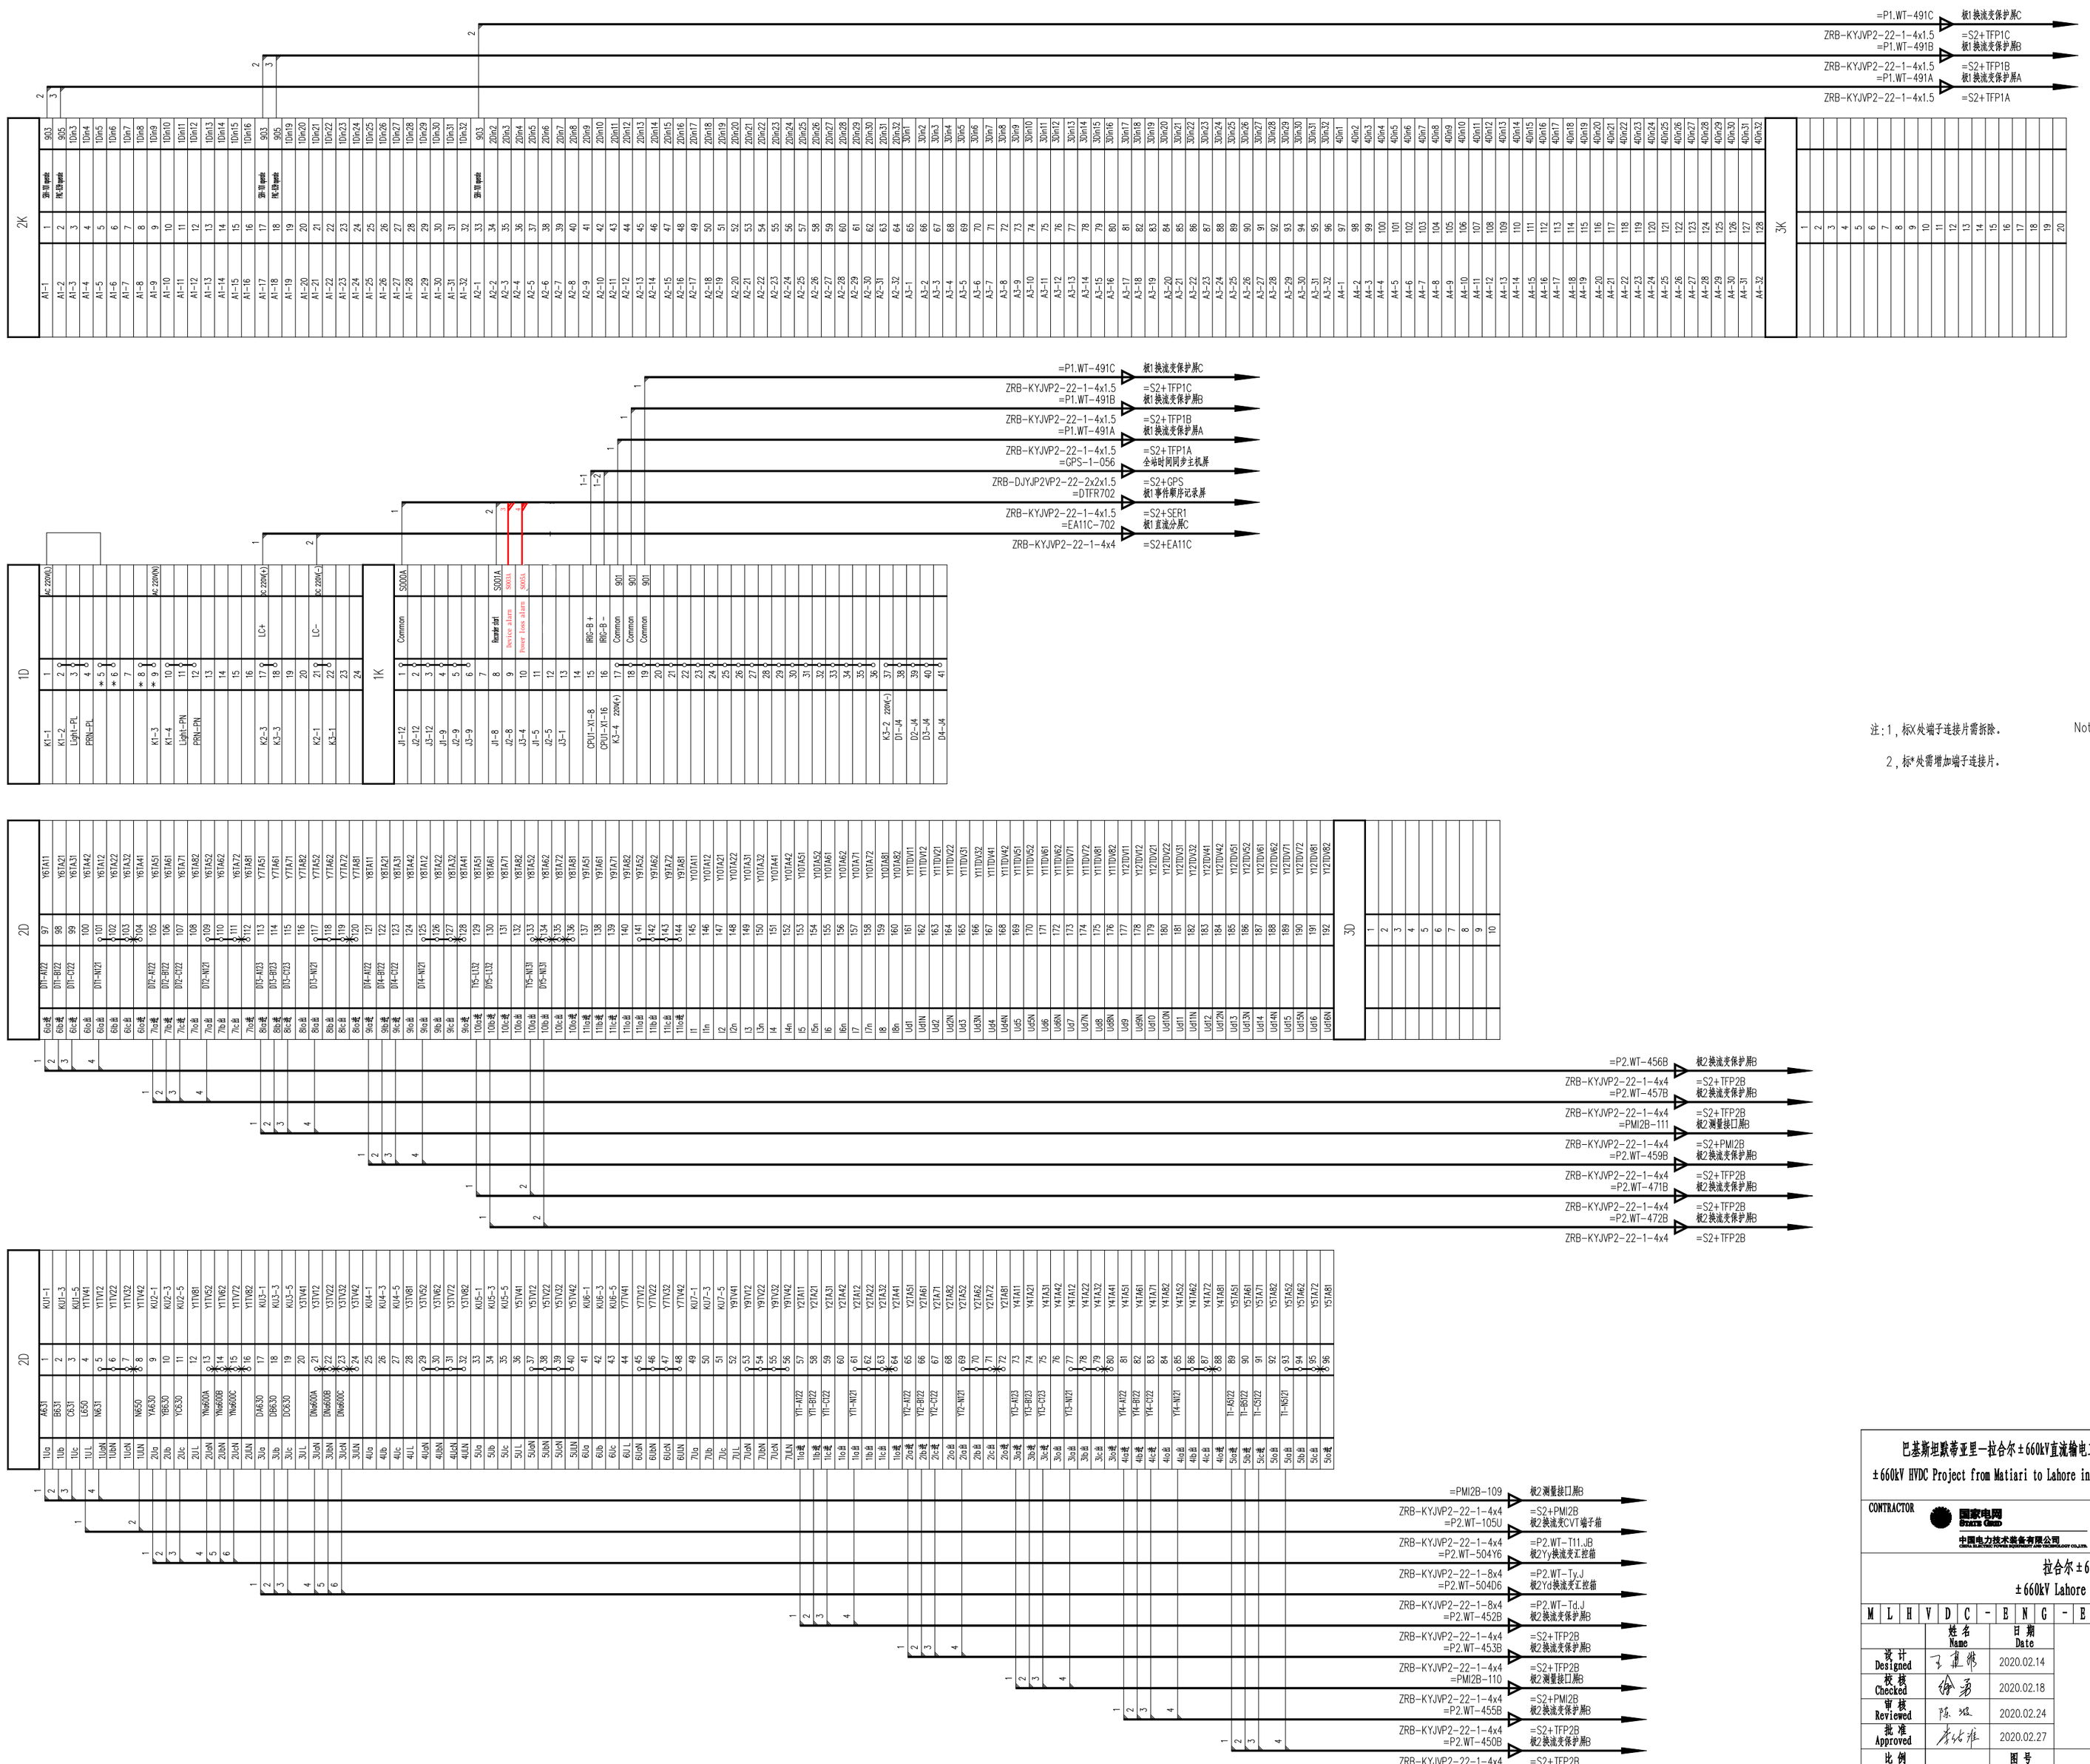

注:1,标X处端子连接片需拆除。

2,标*处需增加端子连接片。

Note:1,The terminal connector at mark X needs to be removed.

2,Add terminal connection piece at mark *.

巴基斯坦默蒂亚里—拉合尔±660kV直流输电工程

±660kV HVDC Project from Matiari to Lahore in Pakistan

NATIONAL TRANSMISSION & DESPATCH COMPANY (NTDC) LIMITED PAKISTAN

CONTRACTOR 国家电网 STATE GRID 中国电力技术装备有限公司 CHINA NATIONAL ELECTRIC EQUIPMENT AND TECHNOLOGY CO.,LTD.

SUBCONTRACTOR East China Electric Power Design Institute Co.,Ltd.

拉合尔±660kV换流站

±660kV Lahore Converter Station

设计阶段 PHASE: 施工图 Detail Design

M L H V D C - E N G - E C I - D D - P C - 0 8 0 1 - 0 4 1 A

	姓名 Name	日期 Date
设计 Designed	王建辉	2020.02.14
校核 Checked	徐勇	2020.02.18
审核 Reviewed	陈旭	2020.02.24
批准 Approved	李长雄	2020.02.27

极2换流变故障录波器端子排接线图 (DTFR22)

Terminal block diagram(S2+DTFR22)

比例 Scale:

图号 DWG NO.: 30-B003701S-D0801-041

版本 REV.: A

594X841