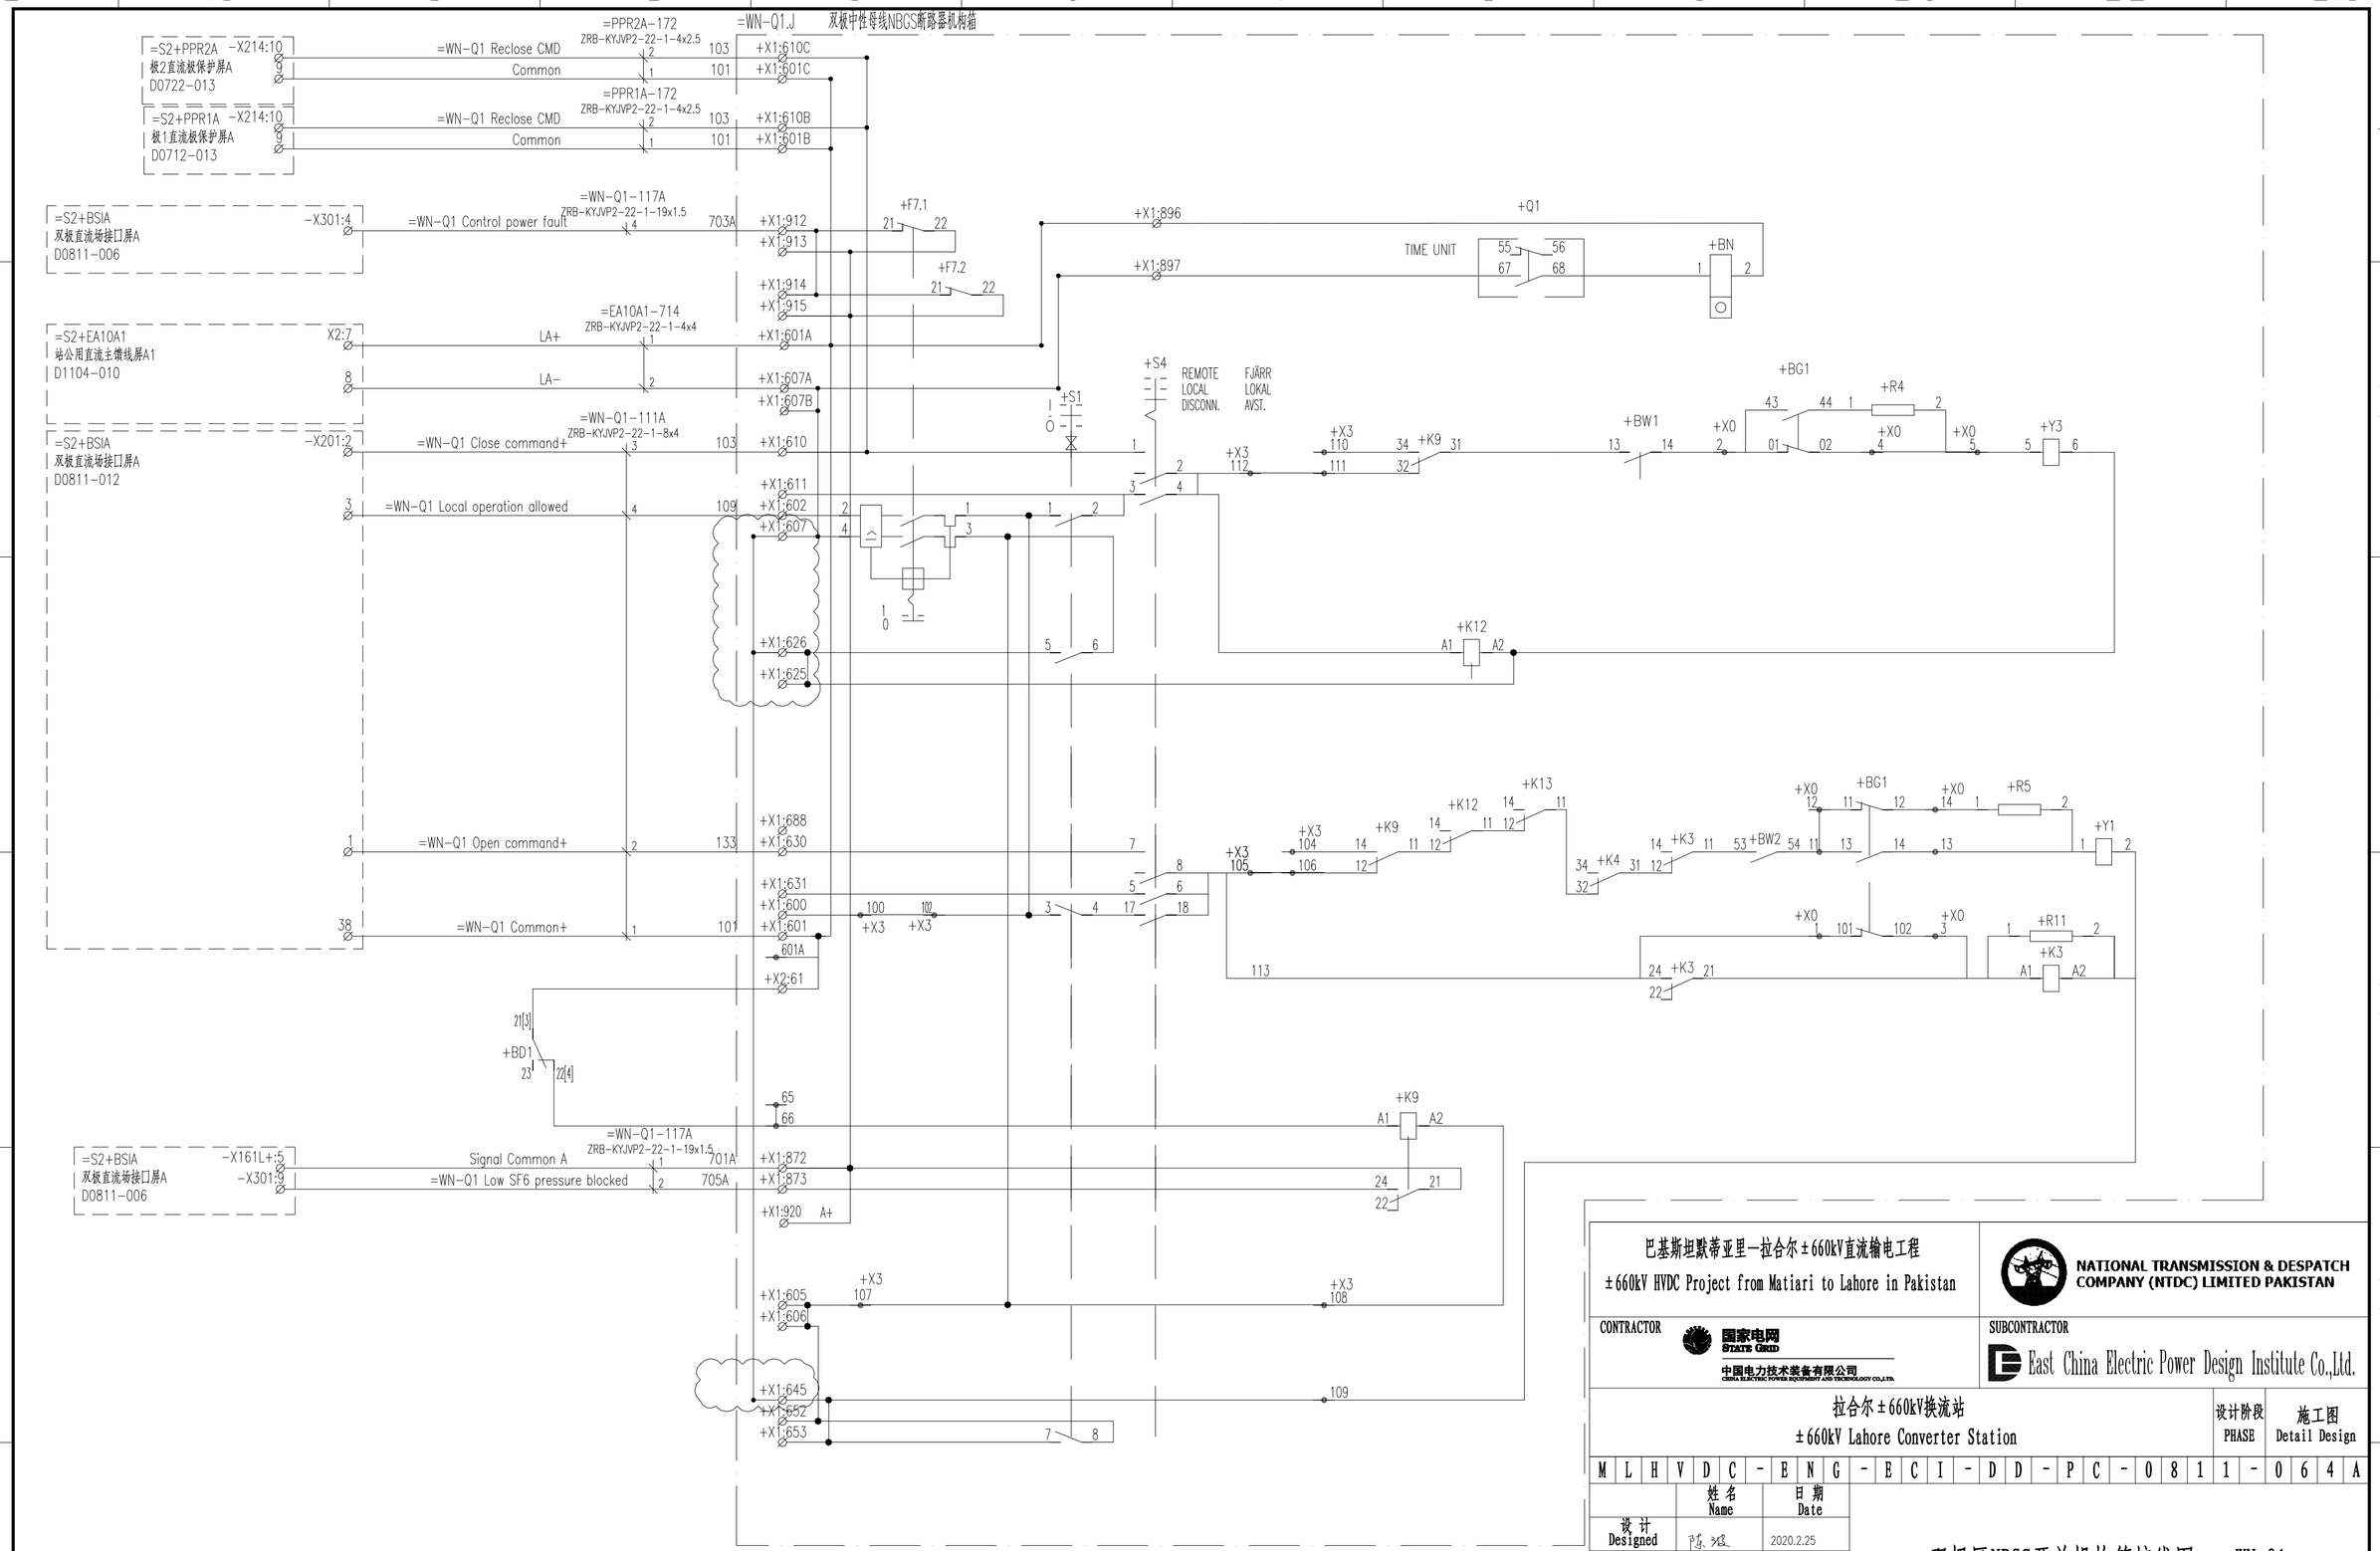

注：短接+X1:915，+X1:872

巴基斯坦默蒂亚里—拉合尔±660kV直流输电工程 ±660kV HVDC Project from Matiari to Lahore in Pakistan	NATIONAL TRANSMISSION & DESPATCH COMPANY (NTDC) LIMITED PAKISTAN
CONTRACTOR 国家电网 STATE GRID 中国电力技术装备有限公司 CHINA ELECTRIC POWER EQUIPMENT AND TECHNOLOGY CO.,LTD.	SUBCONTRACTOR East China Electric Power Design Institute Co.,Ltd.
拉合尔±660kV换流站 ±660kV Lahore Converter Station	设计阶段 PHASE: 施工图 Detail Design

M L H V D C - E N G - E C I - D D - P C - 0 8 1 1 - 0 6 4 A

	姓名 Name	日期 Date
设计 Designed	陈波	2020.2.25
校核 Checked	徐勇	2020.2.25
审核 Reviewed	王建辉	2020.2.25
批准 Approved	李佑雄	2020.2.25

双极区NBGS开关机构箱接线图一 =WN-Q1
Control and signal circuit 1 of WN-Q1

比例 Scale		图号 DWG NO.	30-B003701S-D0811-064	版本 REV.	A

420X594