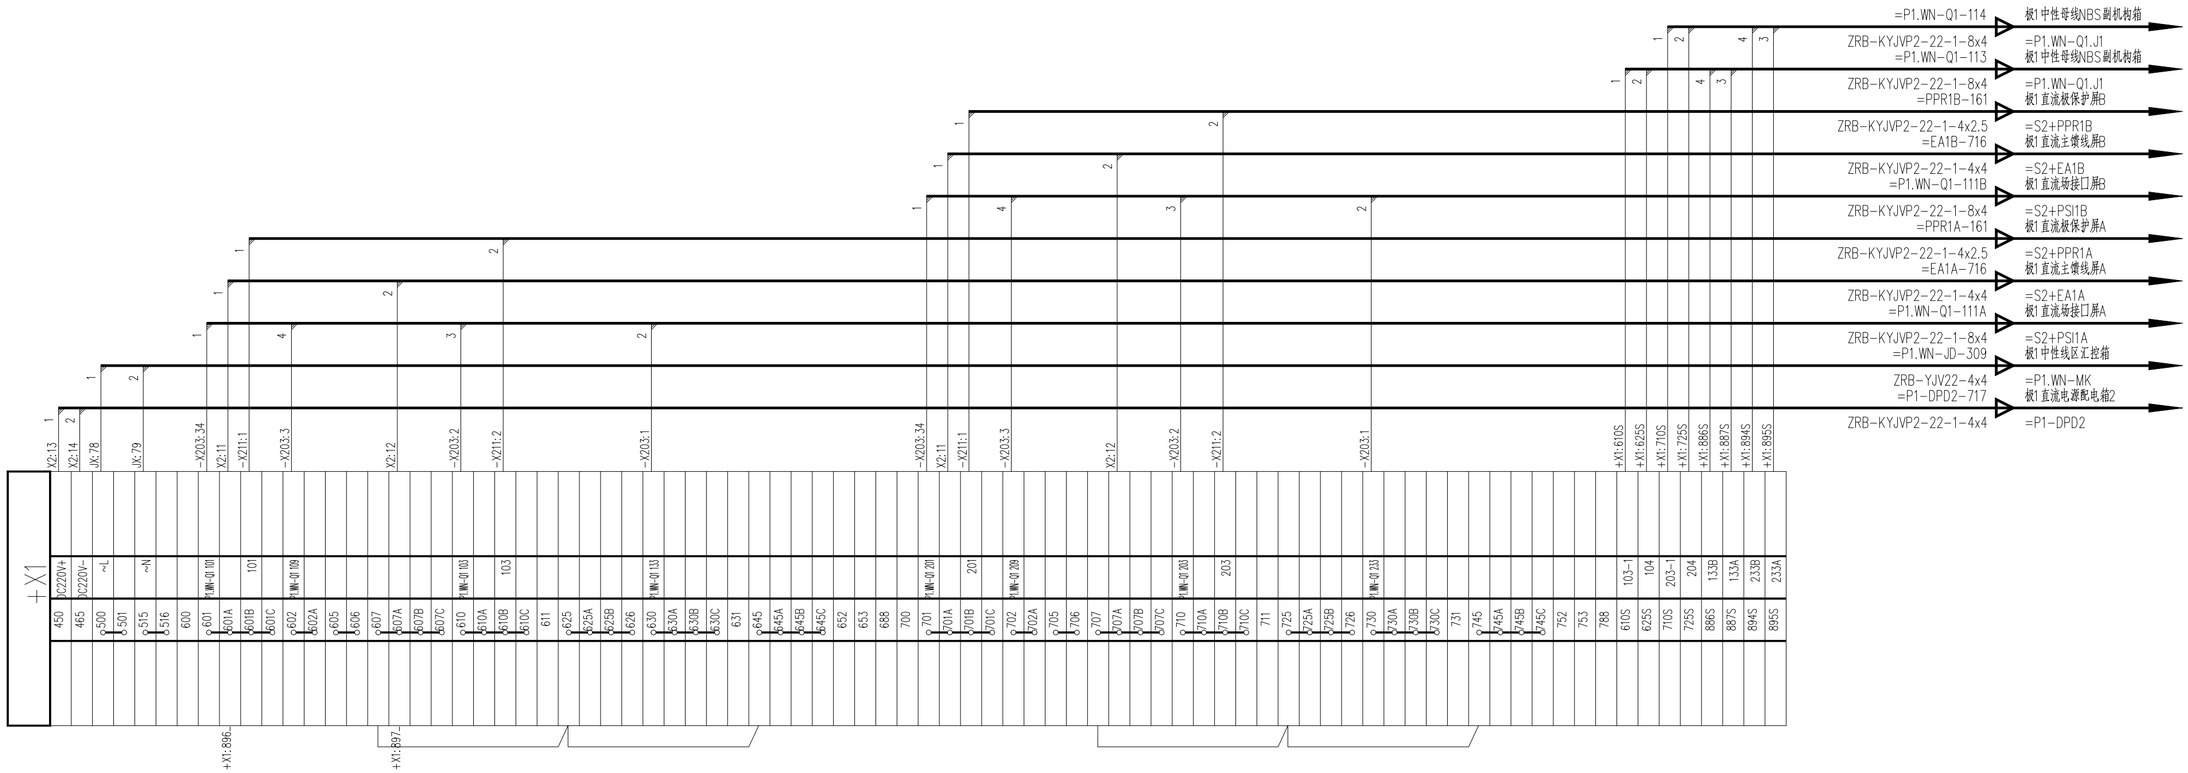

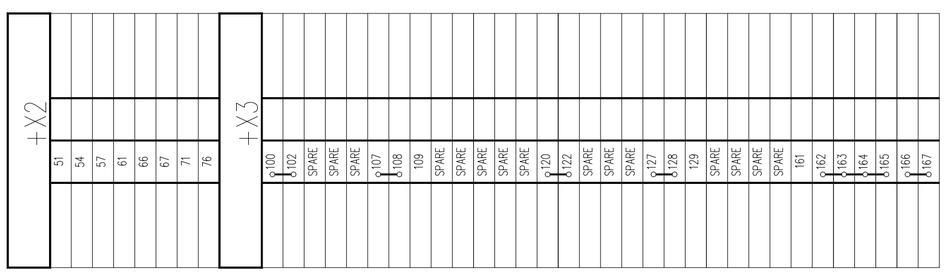

取消电缆=P1.WN-Q1-111A/B第5、6、7芯两侧接线
短接端子X1:607，625，645
短接端子X1:707，725，745

巴基斯坦默蒂亚里—拉合尔±660kV直流输电工程
±660kV HVDC Project from Matiari to Lahore in Pakistan

NATIONAL TRANSMISSION & DESPATCH COMPANY (NTDC) LIMITED PAKISTAN

CONTRACTOR 国家电网 STATE GRID 中国电力技术装备有限公司 CHINA ELECTRIC POWER EQUIPMENT AND TECHNOLOGY CO.,LTD.

SUBCONTRACTOR East China Electric Power Design Institute Co.,Ltd.

拉合尔±660kV换流站
±660kV Lahore Converter Station

设计阶段 PHASE: 施工图 Detail Design

M L H V D C - E N G - E C I - D D - P C - 0 8 2 1 - 1 3 2 A

	姓名 Name	日期 Date
设计 Designed	陈旭	2020.2.25
校核 Checked	徐勇	2020.2.25
审核 Reviewed	王建鹏	2020.2.25
批准 Approved	李钰雅	2020.2.25

极1中性母线NBS主机构箱端子排图二
Terminal diagram 2 of P1.WN-Q1.J2

比例 Scale:
图号 DWG NO.: 30-B003701S-D0821-132
版本 REV.: A

420X594