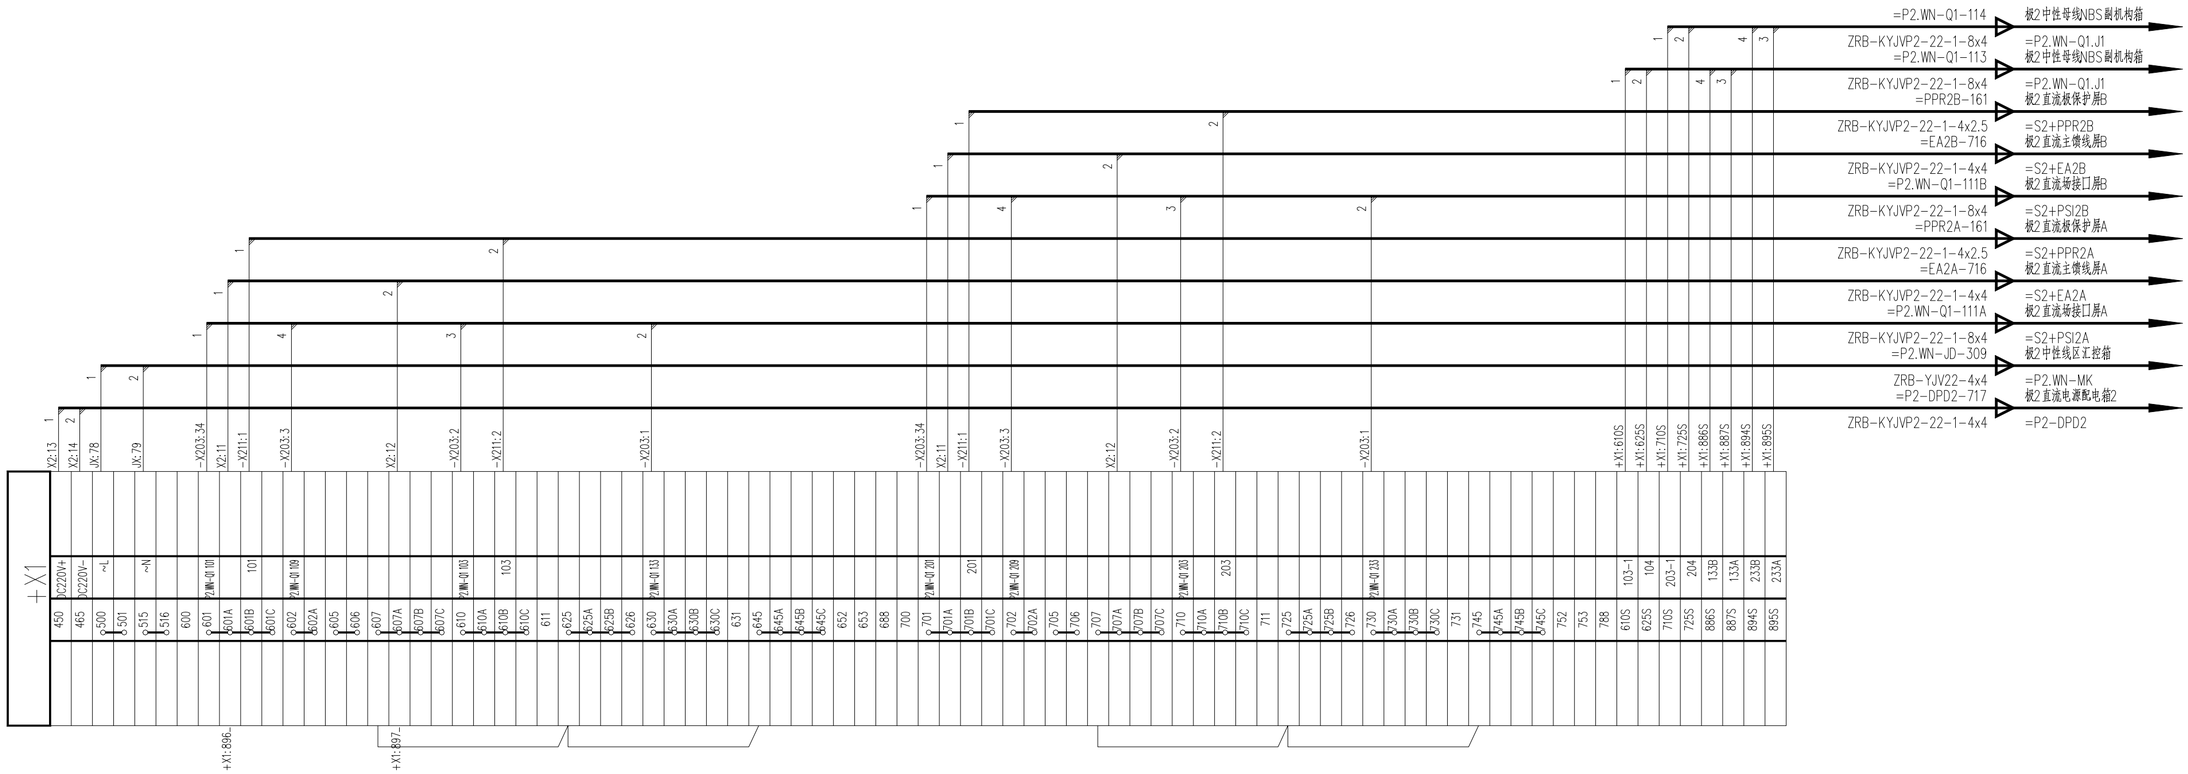

取消电缆=P2.WN-Q1-111A/B第5、6、7芯两侧接线
短接端子X1:607，625，645
短接端子X1:707，725，745

巴基斯坦默蒂亚里—拉合尔±660kV直流输电工程 ±660kV HVDC Project from Matiari to Lahore in Pakistan		NATIONAL TRANSMISSION & DESPATCH COMPANY (NTDC) LIMITED PAKISTAN	
CONTRACTOR 国家电网 STATE GRID 中国电力技术装备有限公司 CHINA ELECTRIC POWER EQUIPMENT AND TECHNOLOGY CO.,LTD.		SUBCONTRACTOR East China Electric Power Design Institute Co.,Ltd.	
拉合尔±660kV换流站 ±660kV Lahore Converter Station		设计阶段 PHASE	施工图 Detail Design
M L H V D C - E N G - E C I - D D - P C - 0 8 3 1 - 1 3 2 A			
	姓名 Name	日期 Date	极2中性母线NBS主机构箱端子排图二 Terminal diagram 2 of P2.WN-Q1.J2
设计 Designed	陈旭	2020.2.25	
校核 Checked	徐勇	2020.2.25	
审核 Reviewed	王建鹏	2020.2.25	
批准 Approved	李钰雅	2020.2.25	
比例 Scale		图号 DWG NO.	30-B003701S-D0831-132
		版本 REV.	A

420X594