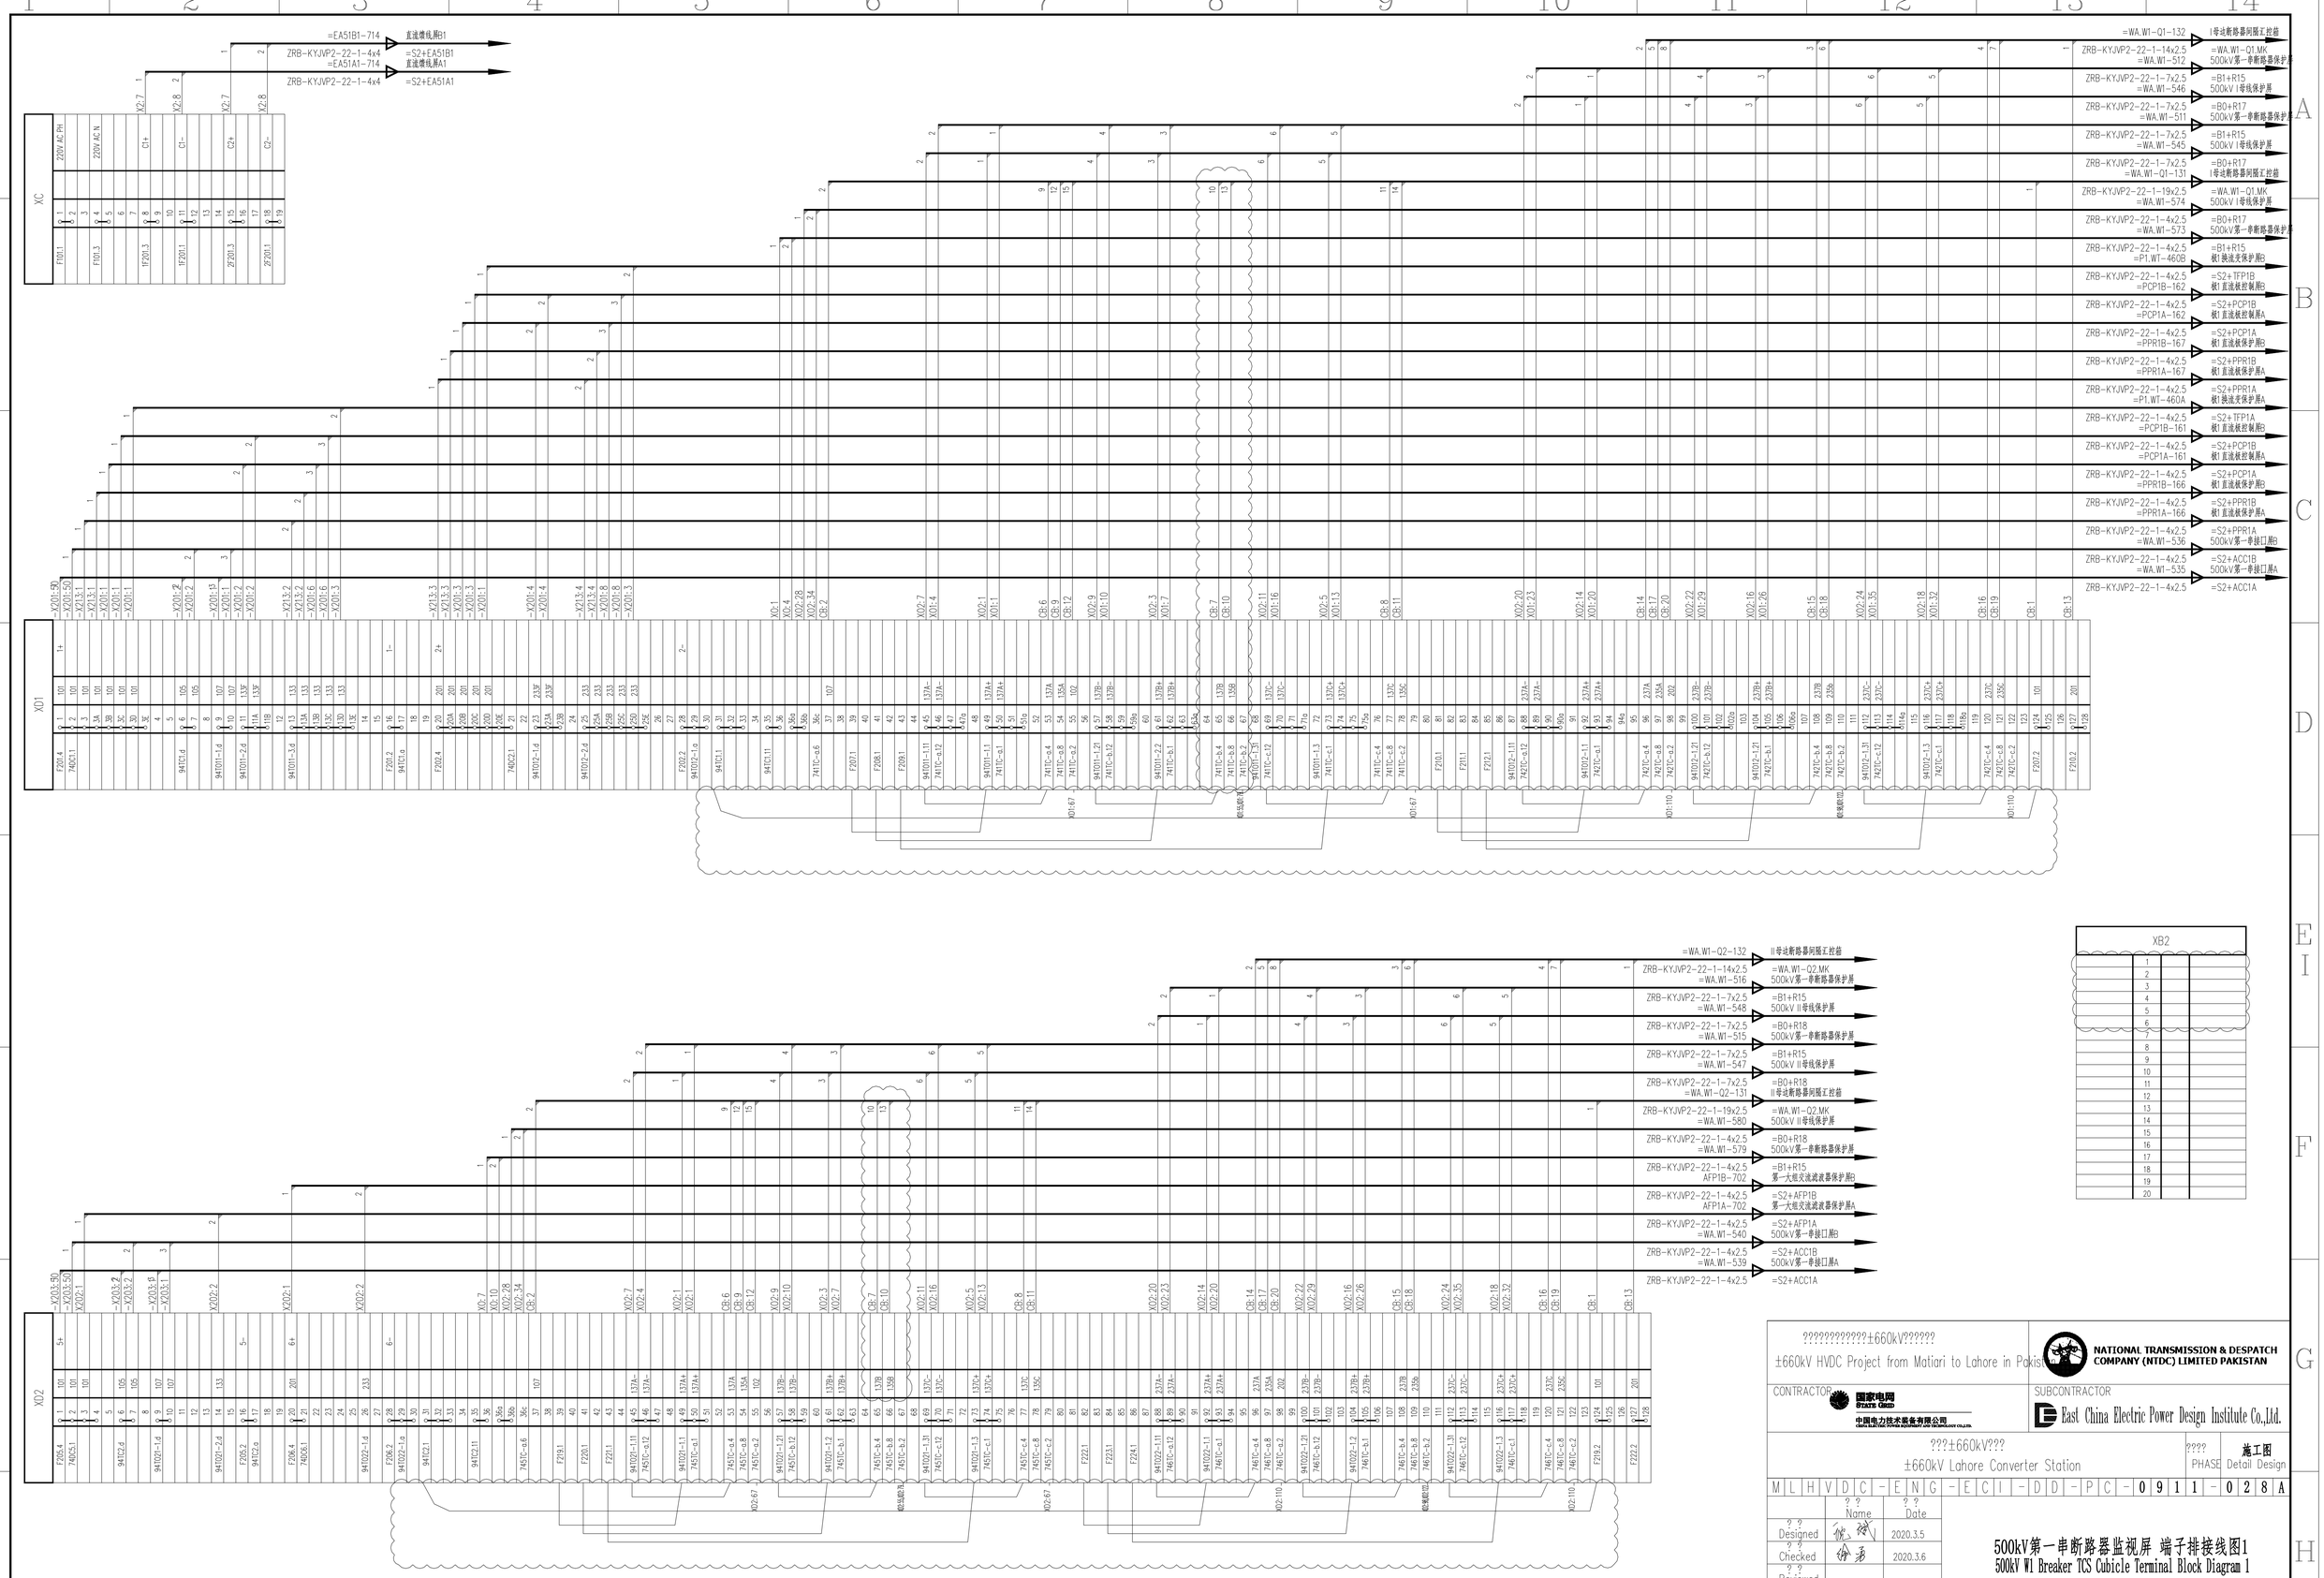

????????????±660kV??????

±660kV HVDC Project from Matiari to Lahore in Pakistan

NATIONAL TRANSMISSION & DESPATCH COMPANY (NTDC) LIMITED PAKISTAN

CONTRACTOR 国家电网 STATE GRID 中国电力技术装备有限公司 CHINA ELECTRIC EQUIPMENT AND TECHNOLOGY CO.,LTD.

SUBCONTRACTOR East China Electric Power Design Institute Co.,Ltd.

???±660kV???

±660kV Lahore Converter Station

???? PHASE 施工图 Detail Design

M L H V D C - E N G - E C I - D D - P C - 0 9 1 1 - 0 2 8 A

	?? Name	?? Date
?? Designed		2020.3.5
?? Checked		2020.3.6
?? Reviewed		
?? Approved		2020.3.9

500kV第一串断路器监视屏 端子排接线图1

500kV W1 Breaker TCS Cubicle Terminal Block Diagram 1

?? Scale

?? DWG NO. 30-B003701S-D0911-028

?? REV. A

594X841