卷册检索号 SEARCH NO. OF THE VOLUME
MLHVDC-ENG-ECI-DD-PC-1053 30-B003701S-D1053

图纸文件目录（首页）

CATALOG OF DRAWING DOCUMENTS (HEAD PAGE)

拉合尔±660kV换流站 工程 施工图 阶段
±660kV Lahore Converter Station PROJECT Detail Design DESIGN STAGE

电气 专业 第 10 卷 第 53 册
Electrical SPECIALITY VOLUME BOOK

卷册名称 35kV/11kV站用变压器二次线
Volume name Schematic of 35/11kV Auxiliary Transformer

批 准 APPROVED BY	
审 核 REVIEWED BY	
设计/勘测 DESIGNED BY/ SURVEYED BY	董利宇
图 纸 6 张 DRAWING NOS.	打印件 1 本 PRINTED COPIES NOS.

序号 No.	图 号 DRAWING NO.	文件名称 DOCUMENT TITLE	版本 EDITION	张 NOS.	本 NOS.	备注 REMARKS
1	30-B003701S-D1053-001	1号35/10kV站用变本体接线图一 Wiring diagram 1 of =WC1-31B.J	A	1		
2	30-B003701S-D1053-002	1号35/10kV站用变本体接线图二 Wiring diagram 2 of =WC1-31B.J	A	1		
3	30-B003701S-D1053-003	2号35/10kV站用变本体接线图一 Wiring diagram 1 of =WC2-32B.J	A	1		
4	30-B003701S-D1053-004	2号35/10kV站用变本体接线图二 Wiring diagram 2 of =WC2-32B.J	A	1		
5	30-B003701S-D1053-005	1号35/10kV站用变本体端子箱端子排图 Terminal Diagram of =WC1-31B.J	A	1		
6	30-B003701S-D1053-006	2号35/10kV站用变本体端子箱端子排图 Terminal Diagram of =WC2-32B.J	A	1		

注:

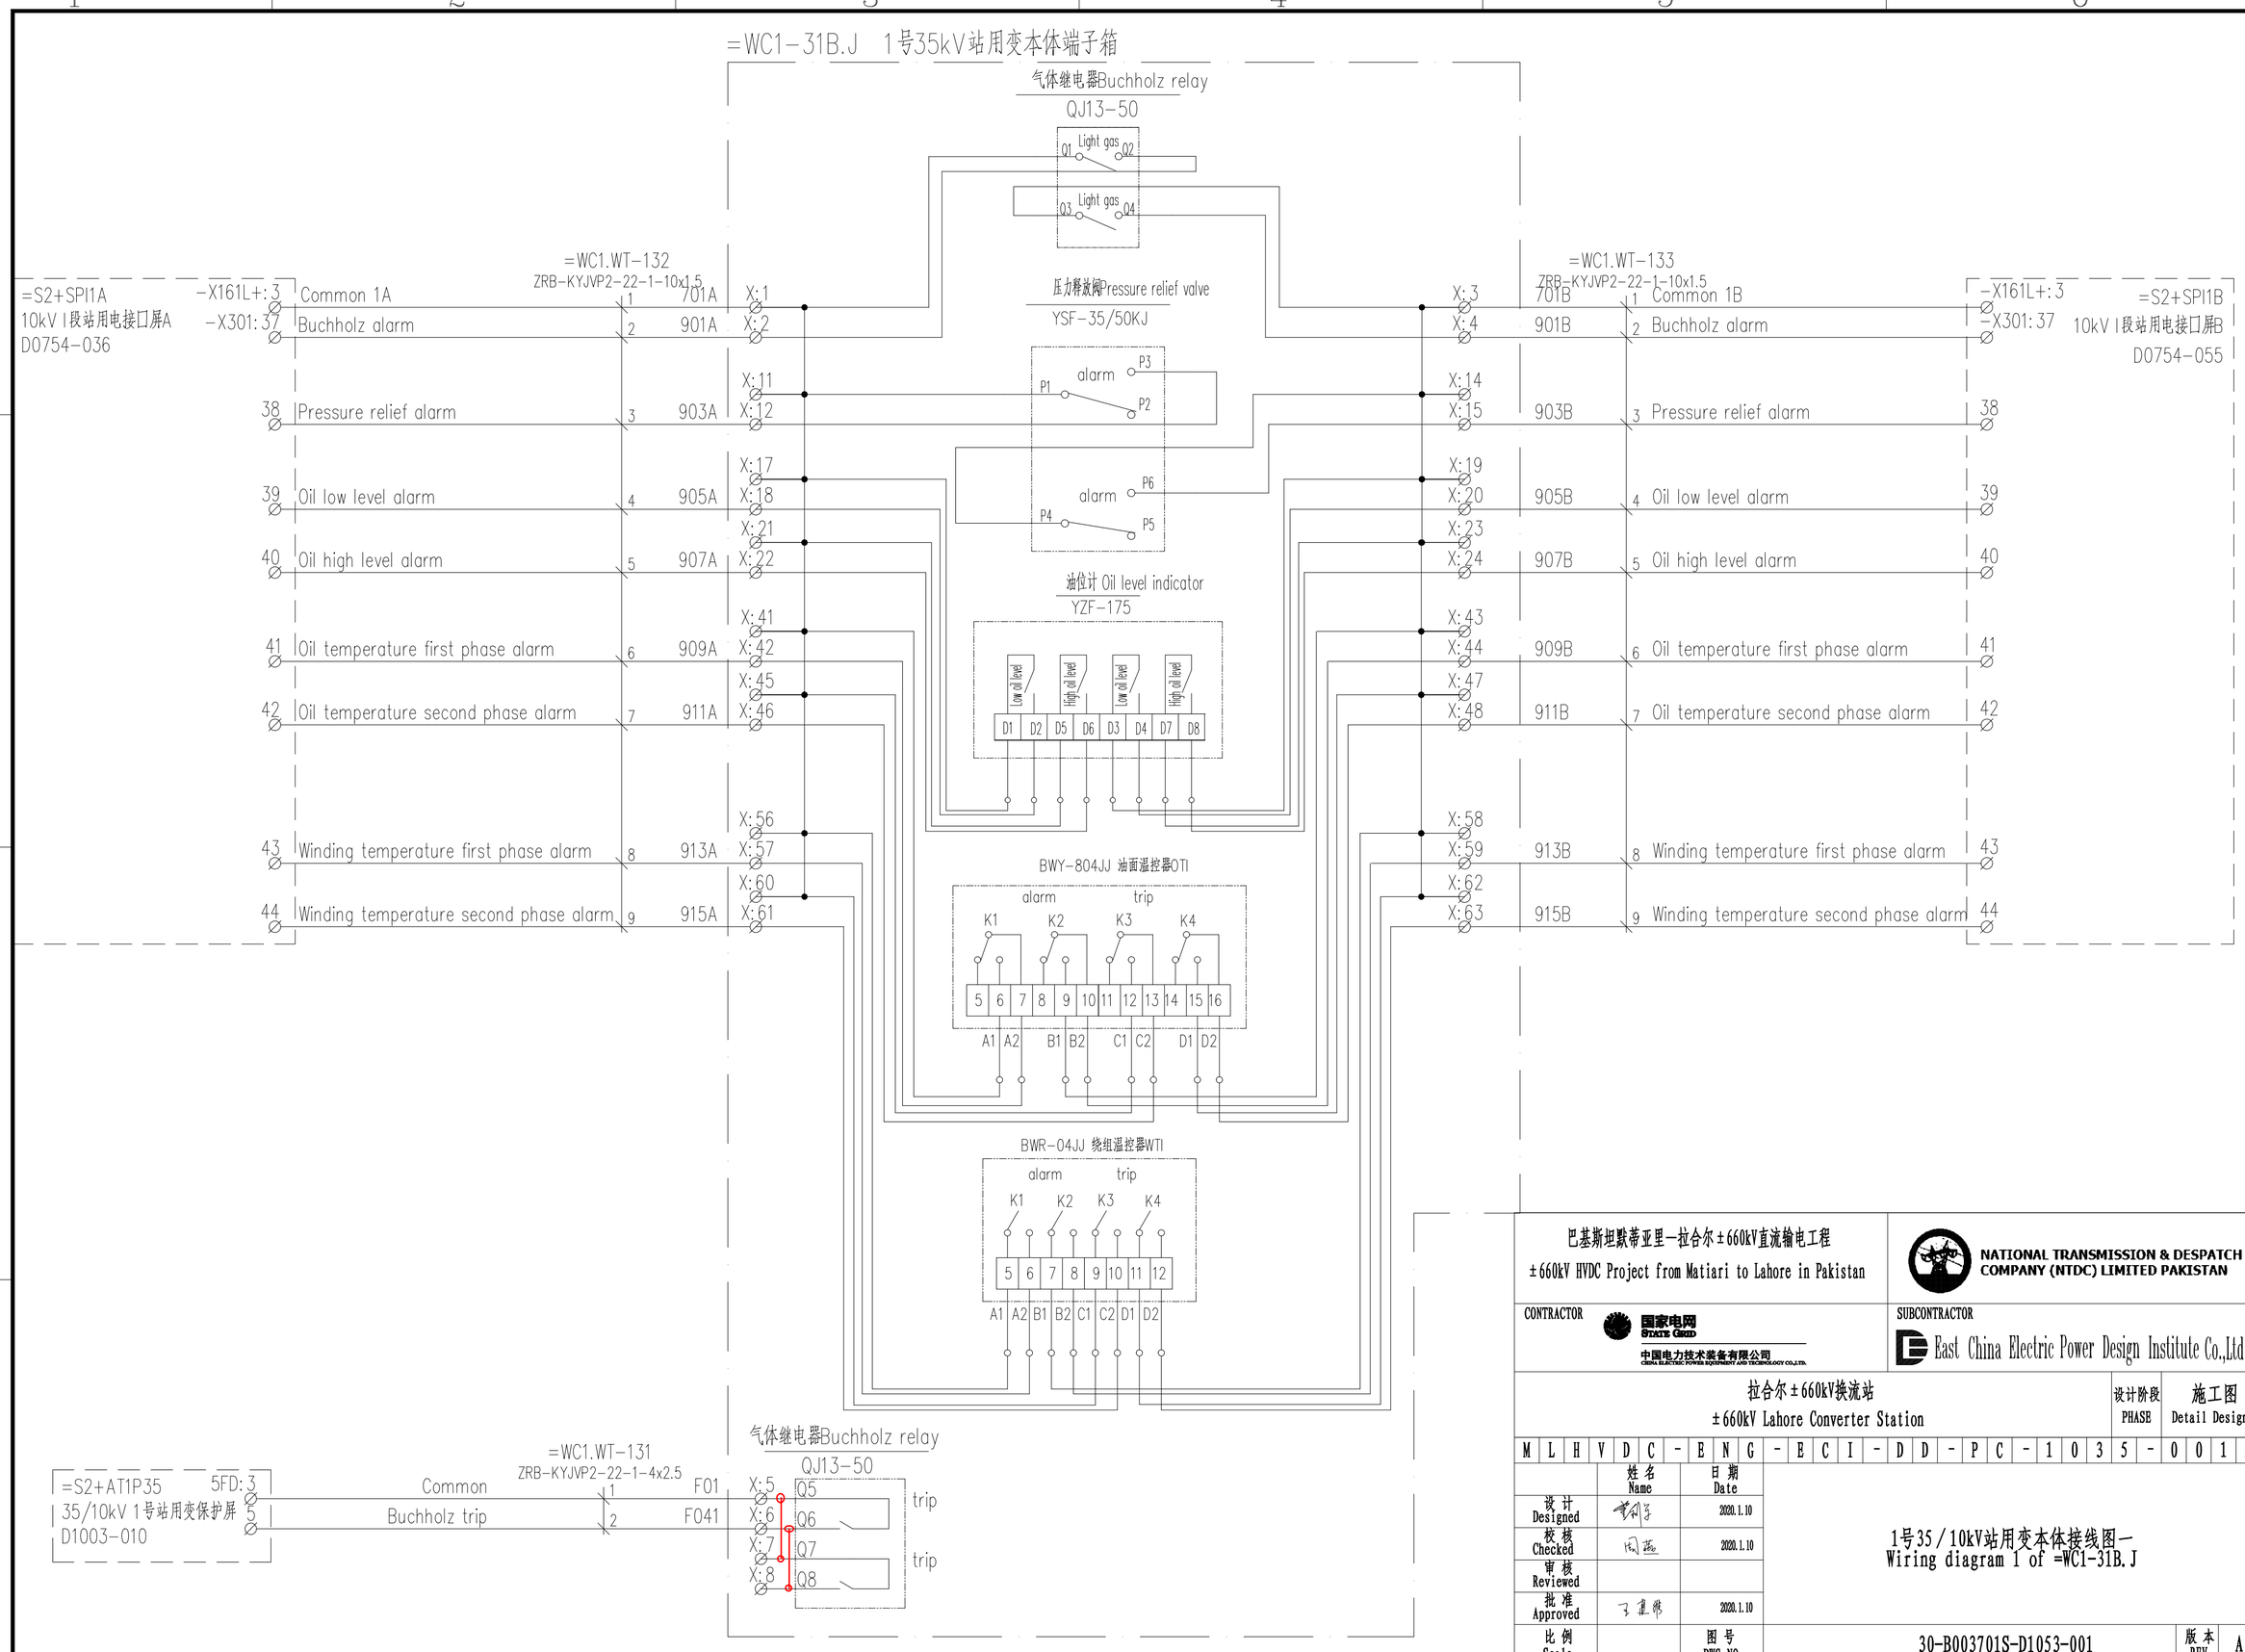

巴基斯坦默蒂亚里—拉合尔±660kV直流输电工程

±660kV HVDC Project from Matiari to Lahore in Pakistan

NATIONAL TRANSMISSION & DESPATCH COMPANY (NTDC) LIMITED PAKISTAN

CONTRACTOR 国家电网 STATE GRID 中国电力技术装备有限公司 CHINA ELECTRIC POWER EQUIPMENT AND TECHNOLOGY CO.,LTD.

SUBCONTRACTOR East China Electric Power Design Institute Co.,Ltd.

拉合尔±660kV换流站

±660kV Lahore Converter Station

设计阶段 PHASE: 施工图 Detail Design

M L H V D C - E N G - E C I - D D - P C - 1 0 3 5 - 0 0 1 A

	姓名 Name	日期 Date
设计 Designed		2020.1.10
校核 Checked		2020.1.10
审核 Reviewed		
批准 Approved		2020.1.10
比例 Scale		图号 DWG NO.

1号35/10kV站用变本体接线图一

Wiring diagram 1 of =WC1-31B.J

30-B003701S-D1053-001

版本 REV. A

297X420

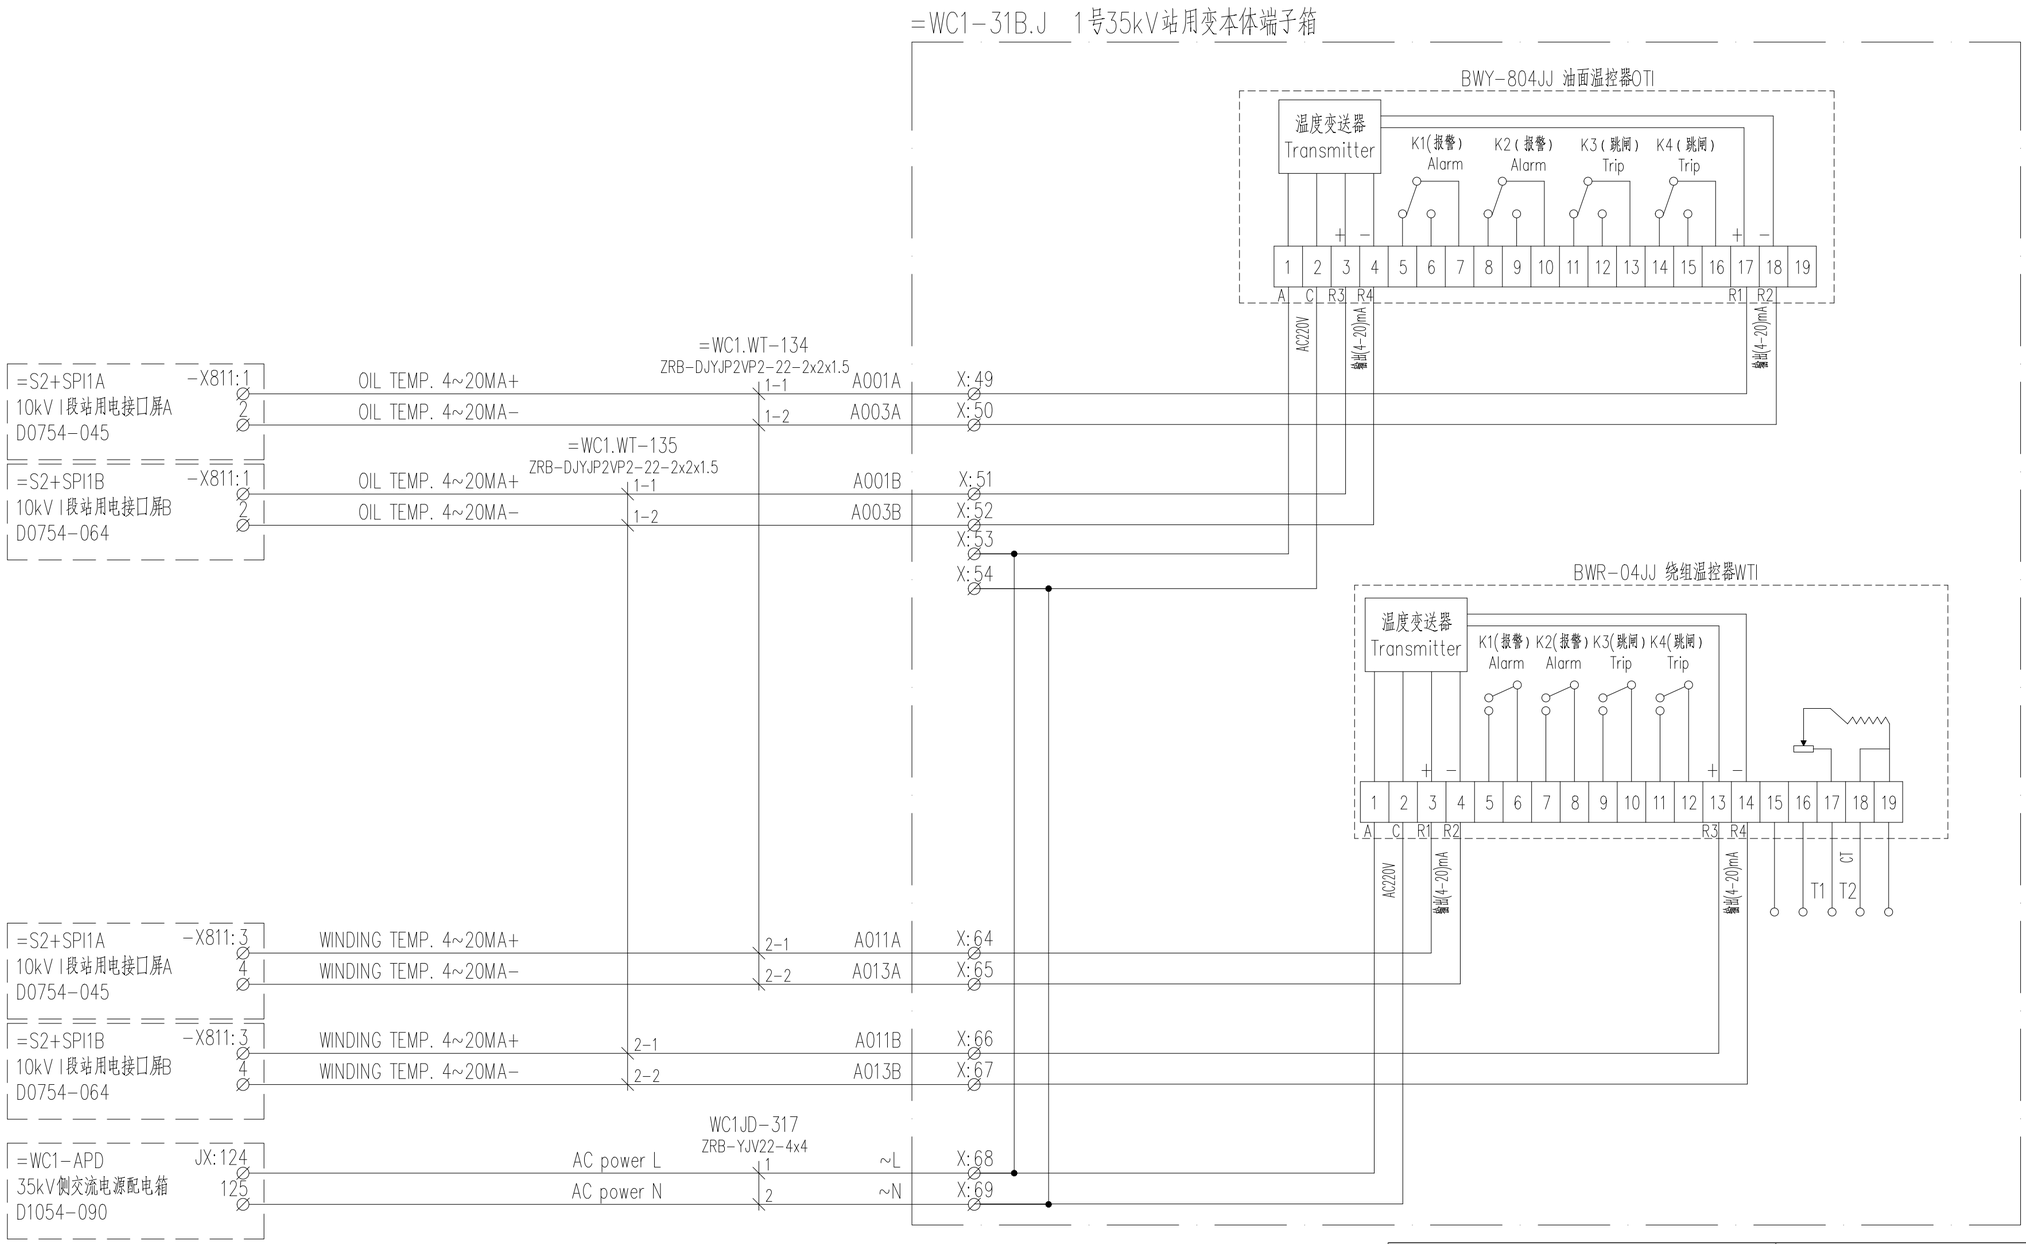

巴基斯坦默蒂亚里—拉合尔±660kV直流输电工程

±660kV HVDC Project from Matiari to Lahore in Pakistan

NATIONAL TRANSMISSION & DESPATCH COMPANY (NTDC) LIMITED PAKISTAN

CONTRACTOR 国家电网 STATE GRID 中国电力技术装备有限公司 CHINA ELECTRIC POWER EQUIPMENT AND TECHNOLOGY CO.,LTD.

SUBCONTRACTOR East China Electric Power Design Institute Co.,Ltd.

拉合尔±660kV换流站

±660kV Lahore Converter Station

设计阶段 PHASE: 施工图 Detail Design

M L H V D C - E N G - E C I - D D - P C - 1 0 3 5 - 0 0 2 A

	姓名 Name	日期 Date
设计 Designed		2020.1.10
校核 Checked		2020.1.10
审核 Reviewed		
批准 Approved		2020.1.10
比例 Scale		图号 DWG NO.

1号35/10kV站用变本体接线图二

Wiring diagram 2 of =WC1-31B.J

30-B003701S-D1053-002

版本 REV. A

297X420

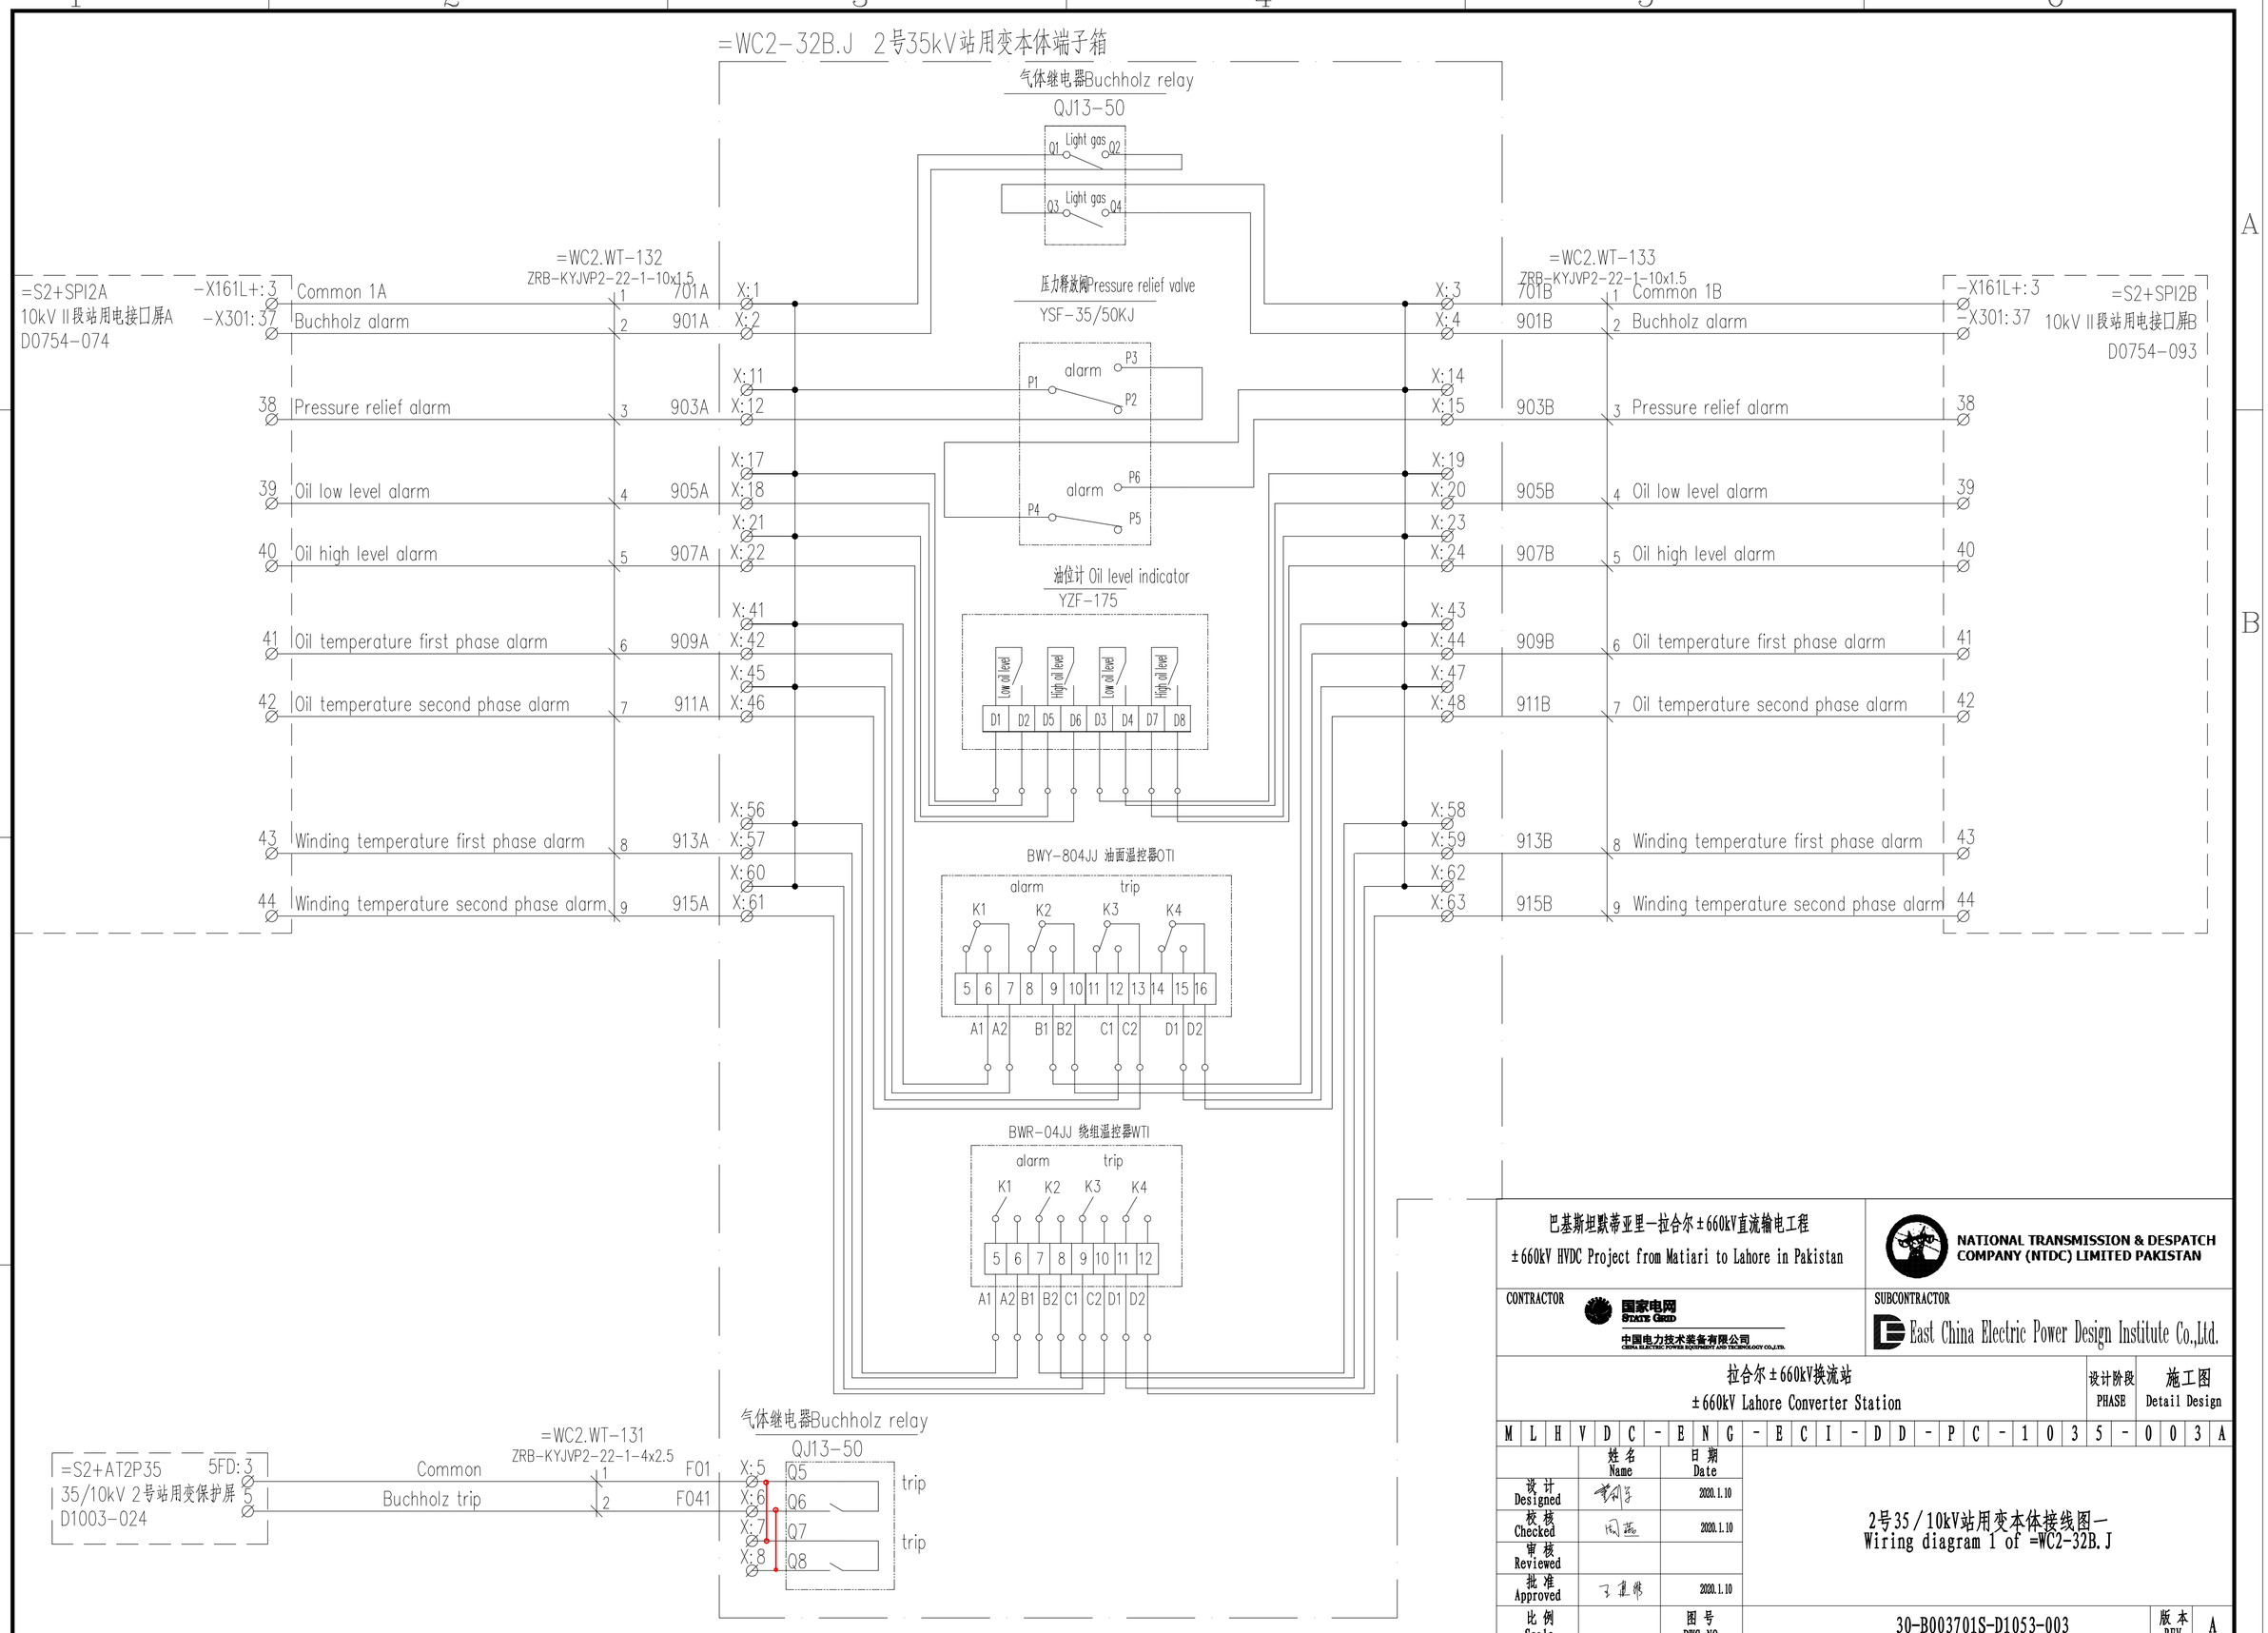

巴基斯坦默蒂亚里—拉合尔±660kV直流输电工程

±660kV HVDC Project from Matiari to Lahore in Pakistan

NATIONAL TRANSMISSION & DESPATCH COMPANY (NTDC) LIMITED PAKISTAN

CONTRACTOR 国家电网 STATE GRID 中国电力技术装备有限公司 CHINA ELECTRIC POWER EQUIPMENT AND TECHNOLOGY CO.,LTD.

SUBCONTRACTOR East China Electric Power Design Institute Co.,Ltd.

拉合尔±660kV换流站

±660kV Lahore Converter Station

设计阶段 PHASE: 施工图 Detail Design

M L H V D C - E N G - E C I - D D - P C - 1 0 3 5 - 0 0 3 A

	姓名 Name	日期 Date
设计 Designed		2020.1.10
校核 Checked		2020.1.10
审核 Reviewed		
批准 Approved		2020.1.10
比例 Scale		图号 DWG NO.

2号35/10kV站用变本体接线图一

Wiring diagram 1 of =WC2-32B.J

30-B003701S-D1053-003

版本 REV. A

297X420

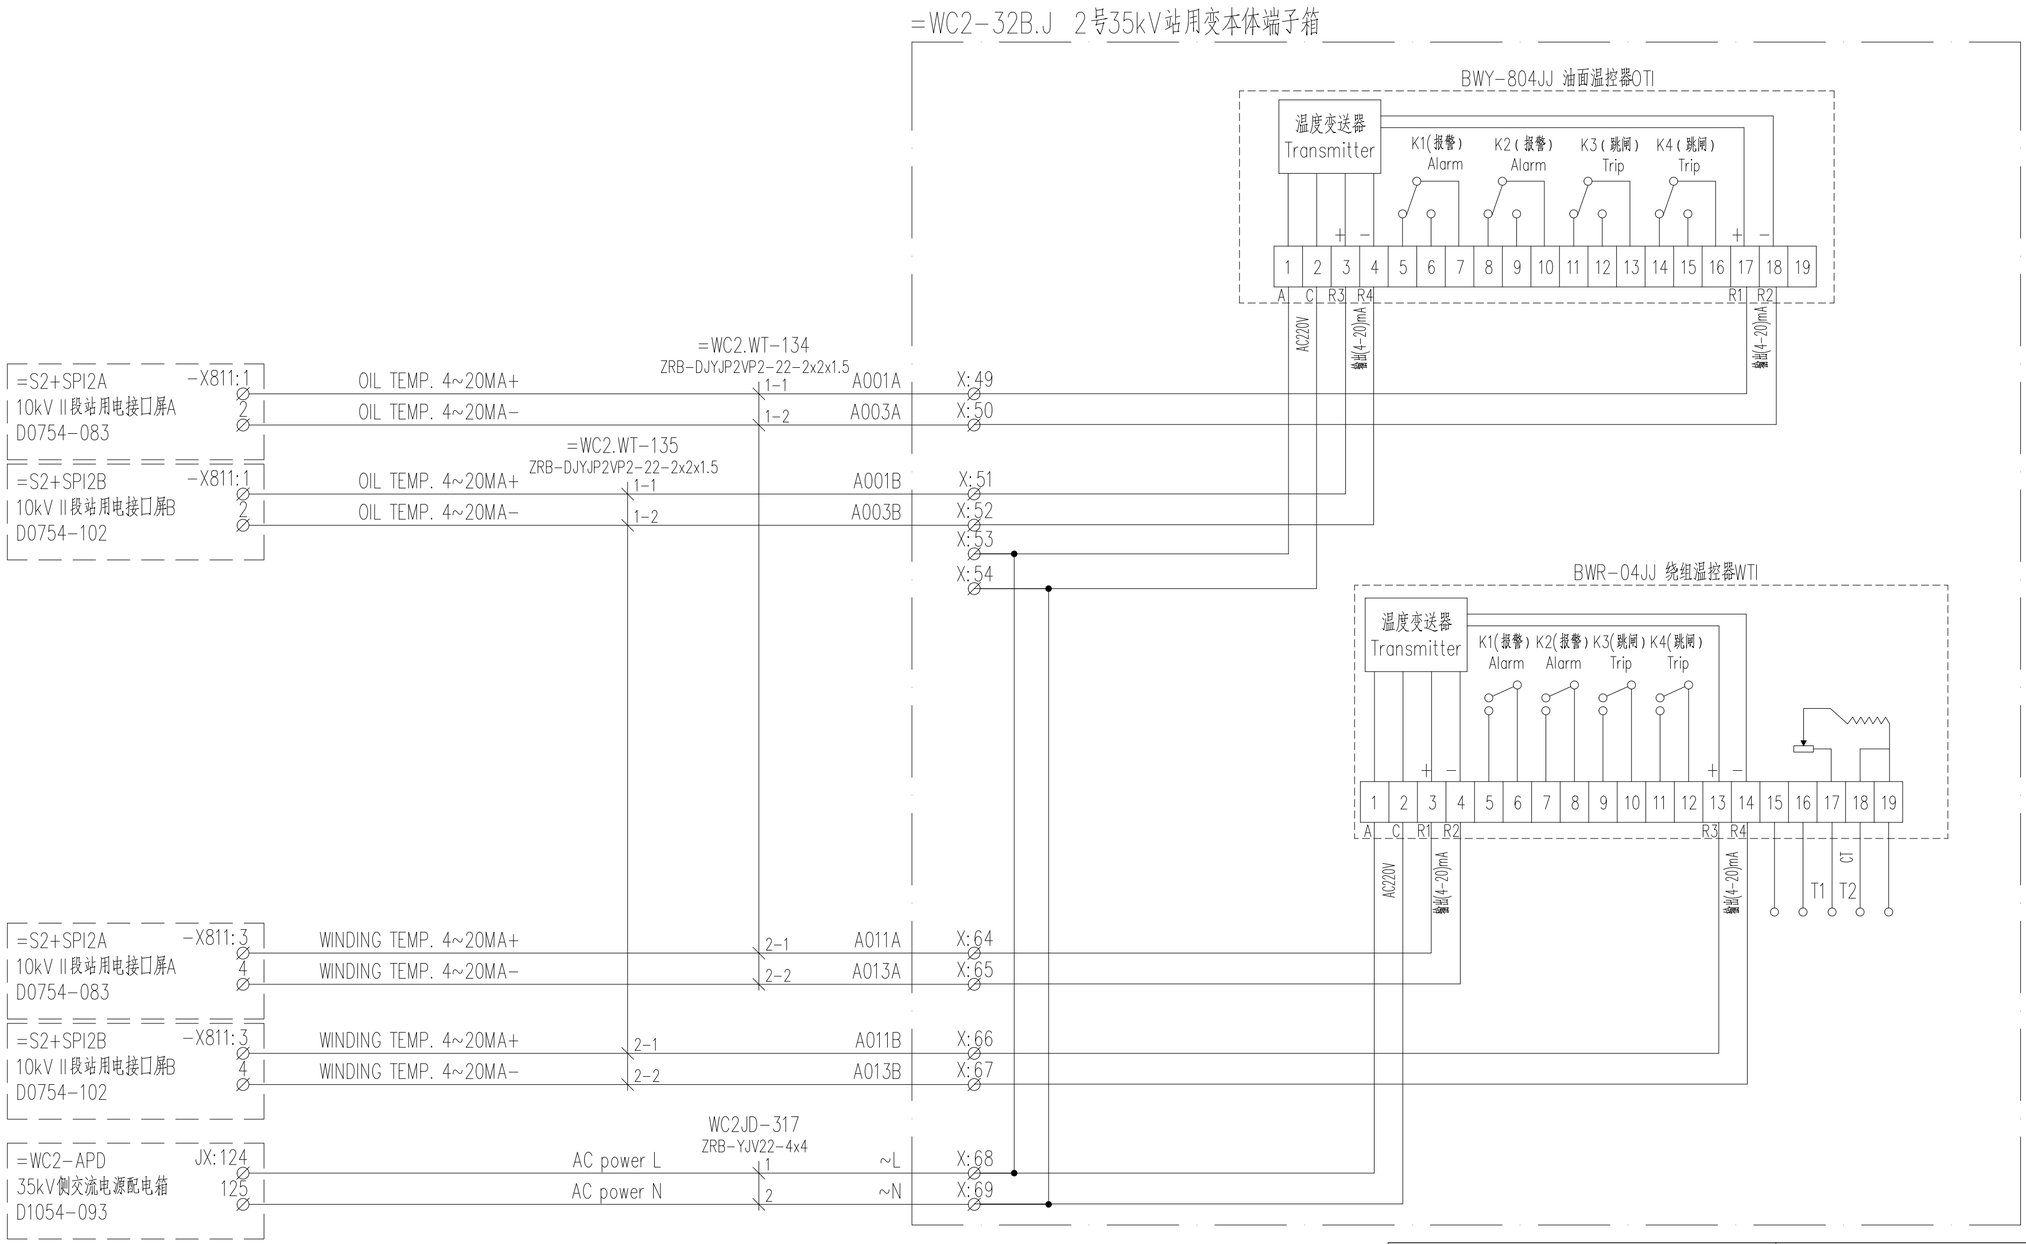

巴基斯坦默蒂亚里—拉合尔±660kV直流输电工程

±660kV HVDC Project from Matiari to Lahore in Pakistan

NATIONAL TRANSMISSION & DESPATCH COMPANY (NTDC) LIMITED PAKISTAN

CONTRACTOR 国家电网 STATE GRID 中国电力技术装备有限公司 CHINA ELECTRIC POWER EQUIPMENT AND TECHNOLOGY CO.,LTD.

SUBCONTRACTOR East China Electric Power Design Institute Co.,Ltd.

拉合尔±660kV换流站

±660kV Lahore Converter Station

设计阶段 PHASE: 施工图 Detail Design

M L H V D C - E N G - E C I - D D - P C - 1 0 3 5 - 0 0 4 A

	姓名 Name	日期 Date
设计 Designed		2020.1.10
校核 Checked		2020.1.10
审核 Reviewed		
批准 Approved		2020.1.10
比例 Scale		图号 DWG NO.

2号35/10kV站用变本体接线图二

Wiring diagram 2 of =WC2-32B.J

30-B003701S-D1053-004

版本 REV. A

297X420

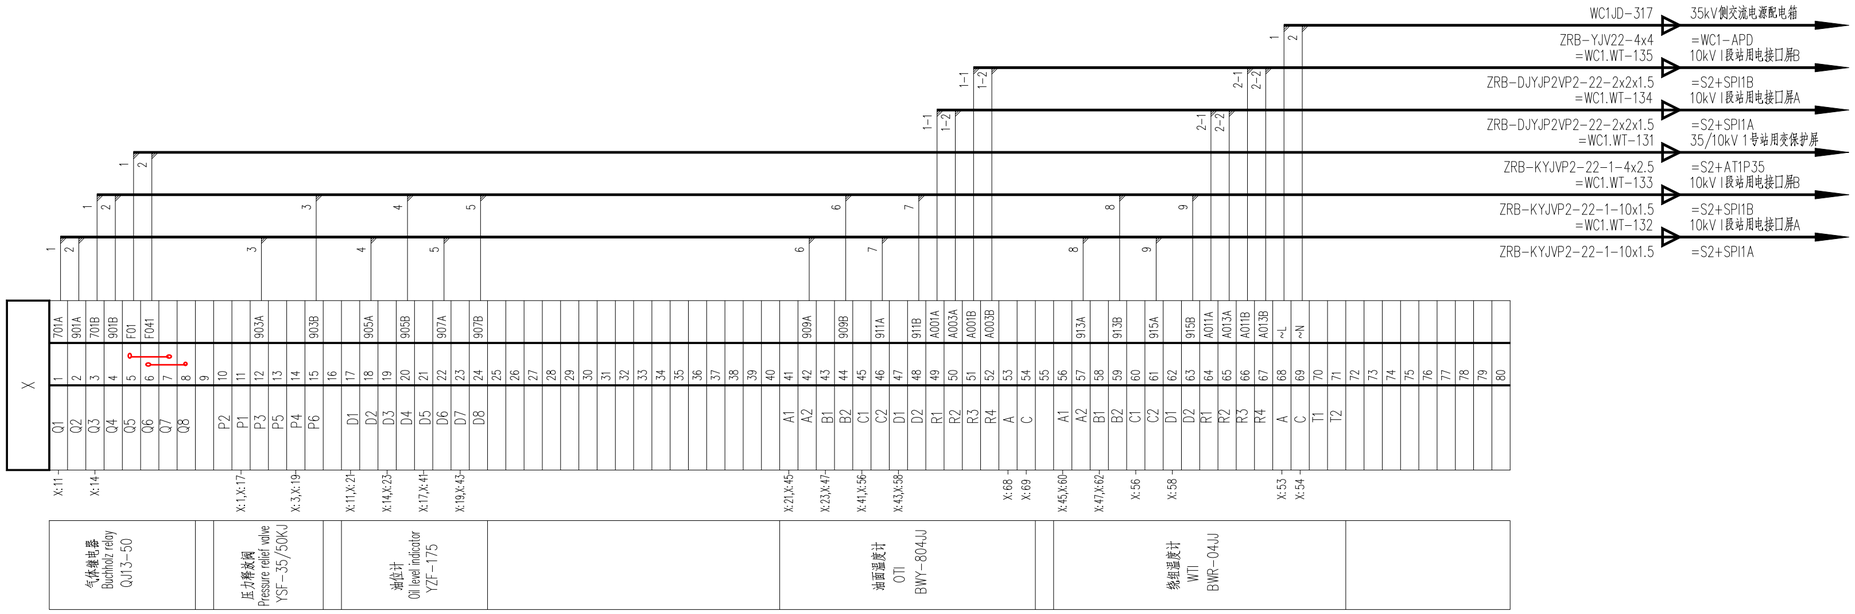

巴基斯坦默蒂亚里—拉合尔±660kV直流输电工程

±660kV HVDC Project from Matiari to Lahore in Pakistan

NATIONAL TRANSMISSION & DESPATCH COMPANY (NTDC) LIMITED PAKISTAN

CONTRACTOR 国家电网 STATE GRID 中国电力技术装备有限公司 CHINA ELECTRIC POWER EQUIPMENT AND TECHNOLOGY CO.,LTD.

SUBCONTRACTOR East China Electric Power Design Institute Co.,Ltd.

拉合尔±660kV换流站

±660kV Lahore Converter Station

设计阶段 PHASE: 施工图 Detail Design

M L H V D C - E N G - E C I - D D - P C - 1 0 5 3 - 0 0 5 A

	姓名 Name	日期 Date
设计 Designed		2020.1.10
校核 Checked		2020.1.10
审核 Reviewed		
批准 Approved		2020.1.10
比例 Scale		图号 DWG NO.

1号35/10kV站用变本体端子箱端子排图
Terminal Diagram of =WC1-31B.J

30-B003701S-D1053-005

版本 REV. A

420X594

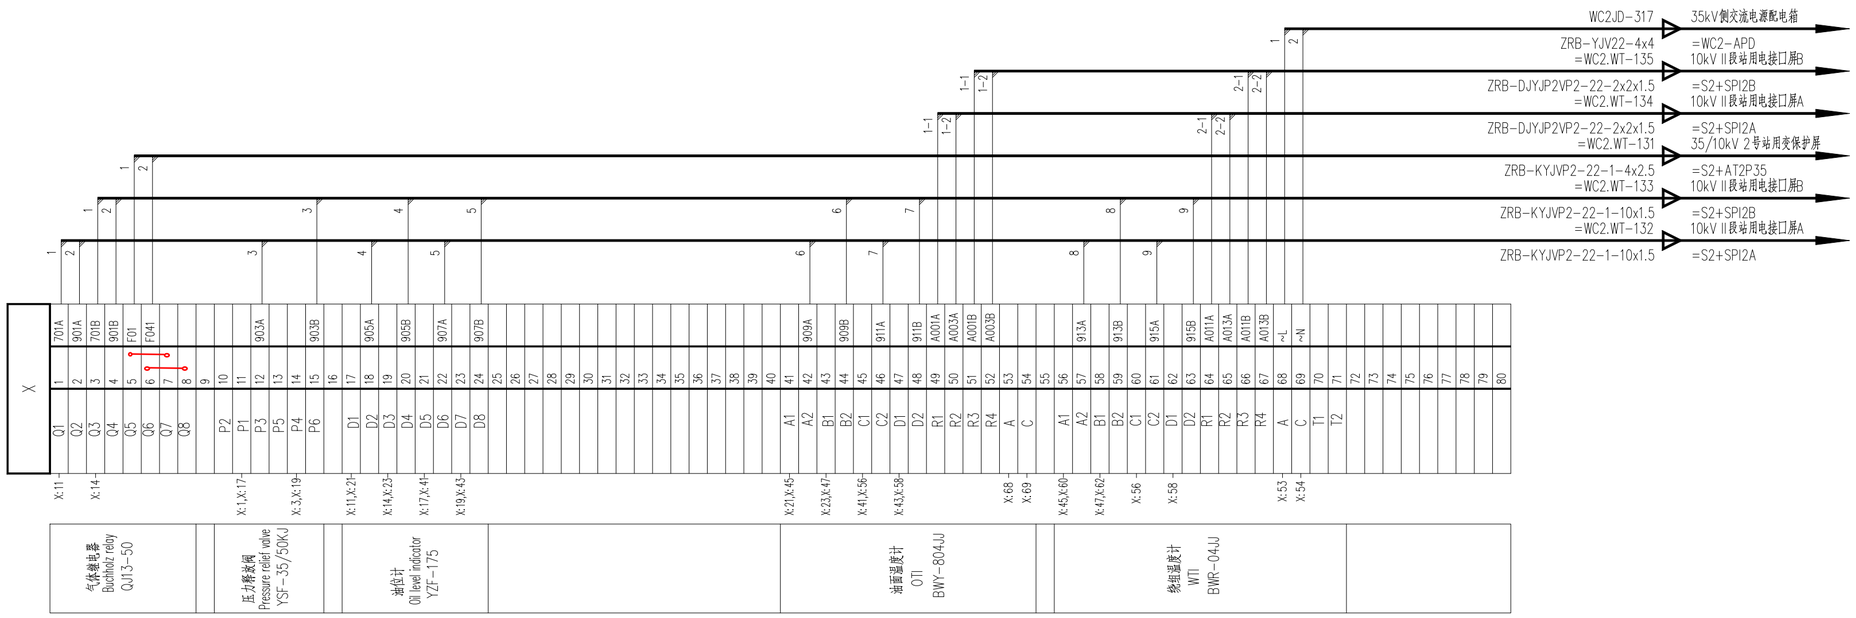

巴基斯坦默蒂亚里—拉合尔±660kV直流输电工程

±660kV HVDC Project from Matiari to Lahore in Pakistan

NATIONAL TRANSMISSION & DESPATCH COMPANY (NTDC) LIMITED PAKISTAN

CONTRACTOR 国家电网 STATE GRID 中国电力技术装备有限公司 CHINA ELECTRIC POWER EQUIPMENT AND TECHNOLOGY CO.,LTD.

SUBCONTRACTOR East China Electric Power Design Institute Co.,Ltd.

拉合尔±660kV换流站

±660kV Lahore Converter Station

设计阶段 PHASE: 施工图 Detail Design

M L H V D C - E N G - E C I - D D - P C - 1 0 5 3 - 0 0 6 A

	姓名 Name	日期 Date
设计 Designed		2020.1.10
校核 Checked		2020.1.10
审核 Reviewed		
批准 Approved		2020.1.10

2号35/10kV站用变本体端子箱端子排图
Terminal Diagram of =WC2-32B.J

比例 Scale		图号 DWG NO.	30-B003701S-D1053-006	版本 REV.	A

420X594