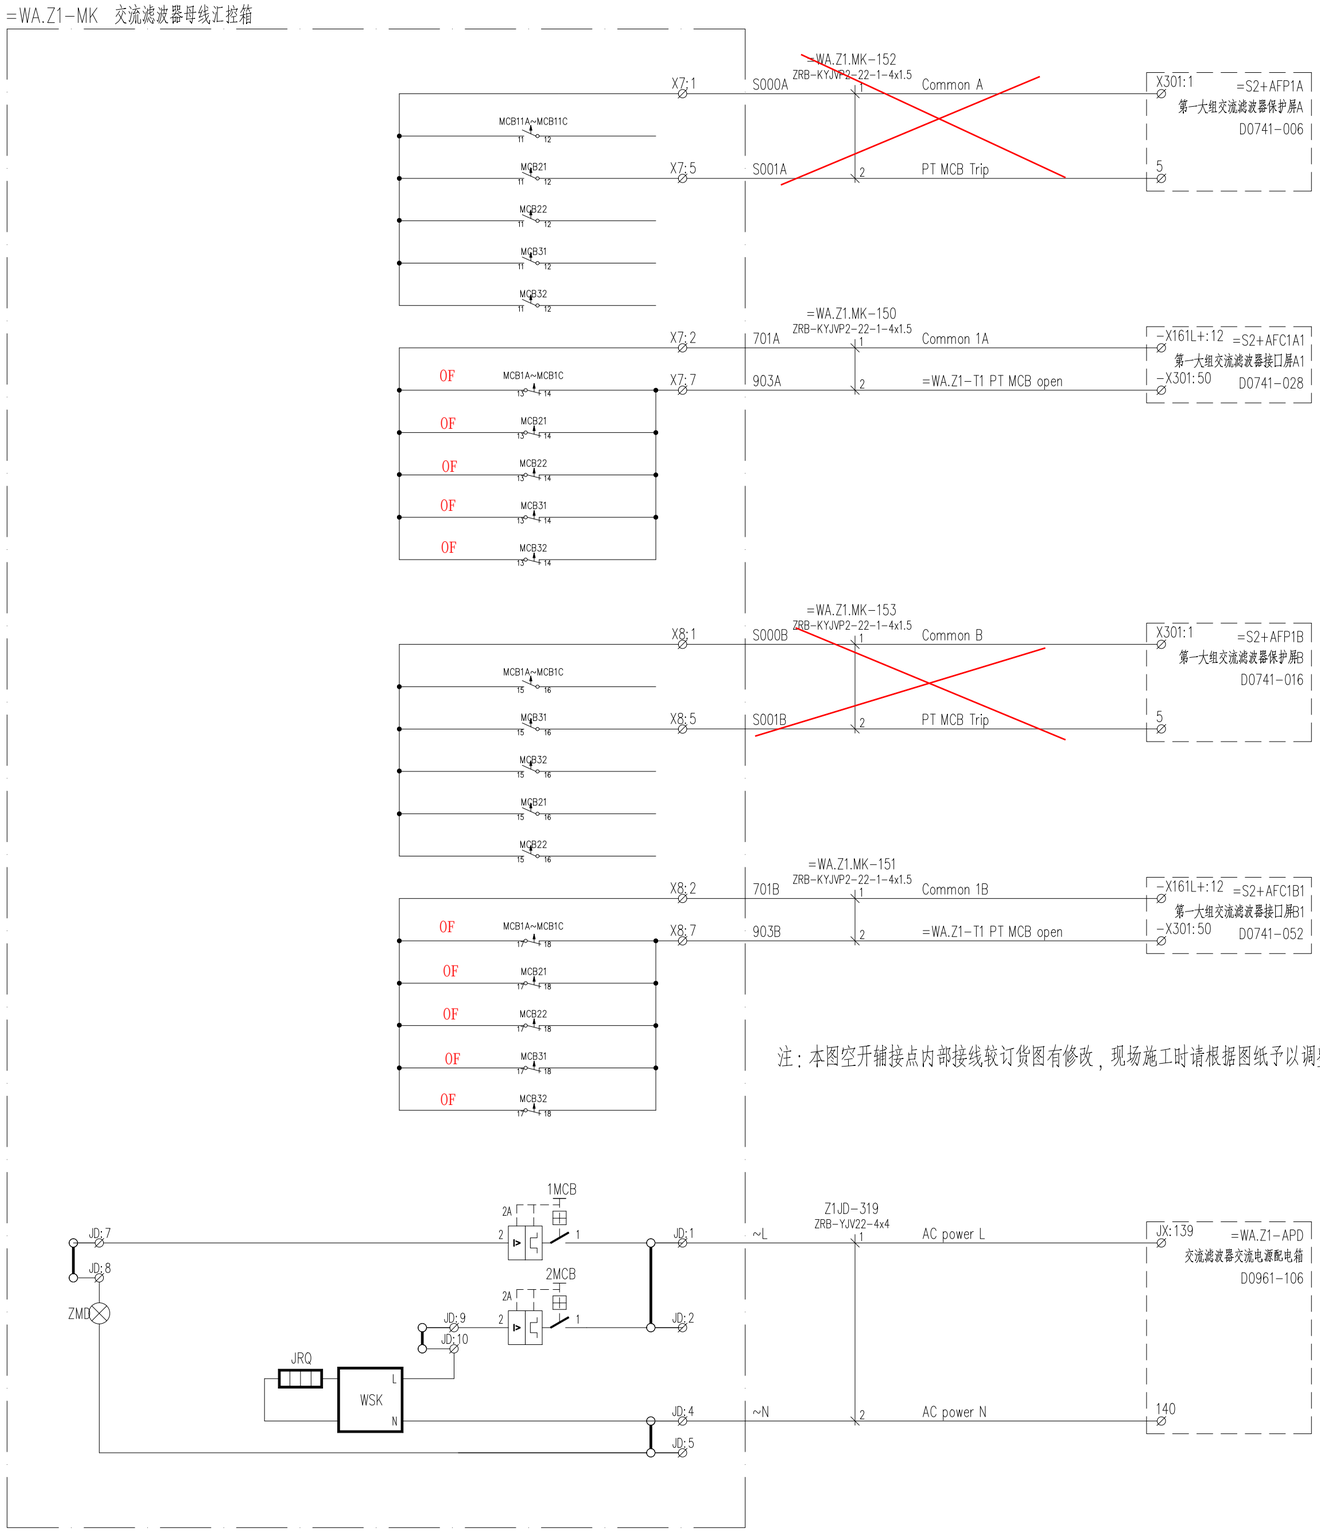

注：本图空开辅接点内部接线较订货图有修改，现场施工时请根据图纸予以调整。

符号	名称	型式及规格		数量	备注
交流滤波器母线汇控箱 =WA.Z1-MK					
	端子箱	ZXW-2/4(1948(H)X670(D)X840(B))		1	
U11~U14	试验端子	URTK/S		38	菲尼克斯
U1~U6	试验端子	URTK/S		72	菲尼克斯
	试验端子连接片	FB10-RTK/S	10位	6	菲尼克斯
X7,X8,JD,ES1,ES2	通用端子	UK6N		101	菲尼克斯
	通用端子连接片	FBI10-8	10位	3	菲尼克斯
MCB11a(b,c)	计量专用小开关	M201M-B3+2OF+2SD,AC230V,3A		3	ABB
MCB21,MCB22,MCB31,MCB32	小开关	iC65N-C3/3P+2OF+2SD		4	施耐德
1MCB,2MCB	小开关	iC65N-C6/1P		2	施耐德
WSK	温湿度控制器	WNK3D	AC220V	1	
JRQ	硅橡胶加热器	NJ100	AC220V,100W	1	
1D	照明灯	PHILIPS-8W	AC220V,8W	1	
	接地铜排	截面：25X8mm^2		0.6米	
	标签框			12	

巴基斯坦默蒂亚里—拉合尔±660kV直流输电工程
±660kV HVDC Project from Matiari to Lahore in Pakistan

NATIONAL TRANSMISSION & DESPATCH COMPANY (NTDC) LIMITED PAKISTAN

CONTRACTOR 国家电网 State Grid 中国电力技术装备有限公司 CHINA ELECTRIC POWER EQUIPMENT AND TECHNOLOGY CO.,LTD.

SUBCONTRACTOR East China Electric Power Design Institute Co.,Ltd.

拉合尔±660kV换流站
±660kV Lahore Converter Station

设计阶段 PHASE: 施工图 Detail Design

M L H V D C - E N G - E C I - D D - P C - 0 9 6 1 - 1 0 2 A

	姓名 Name	日期 Date
设计 Designed	吴晓江	2020.1.10
校核 Checked	徐勇	2020.1.10
审核 Reviewed		
批准 Approved	王建邦	2020.1.10
比例 Scale		

ACF1母线汇控箱接线回路图一
Circuit diagram 1 of =WA.Z1-MK

图号 DWG NO.: 30-B003701S-D0961-102

版本 REV.: A

420X594