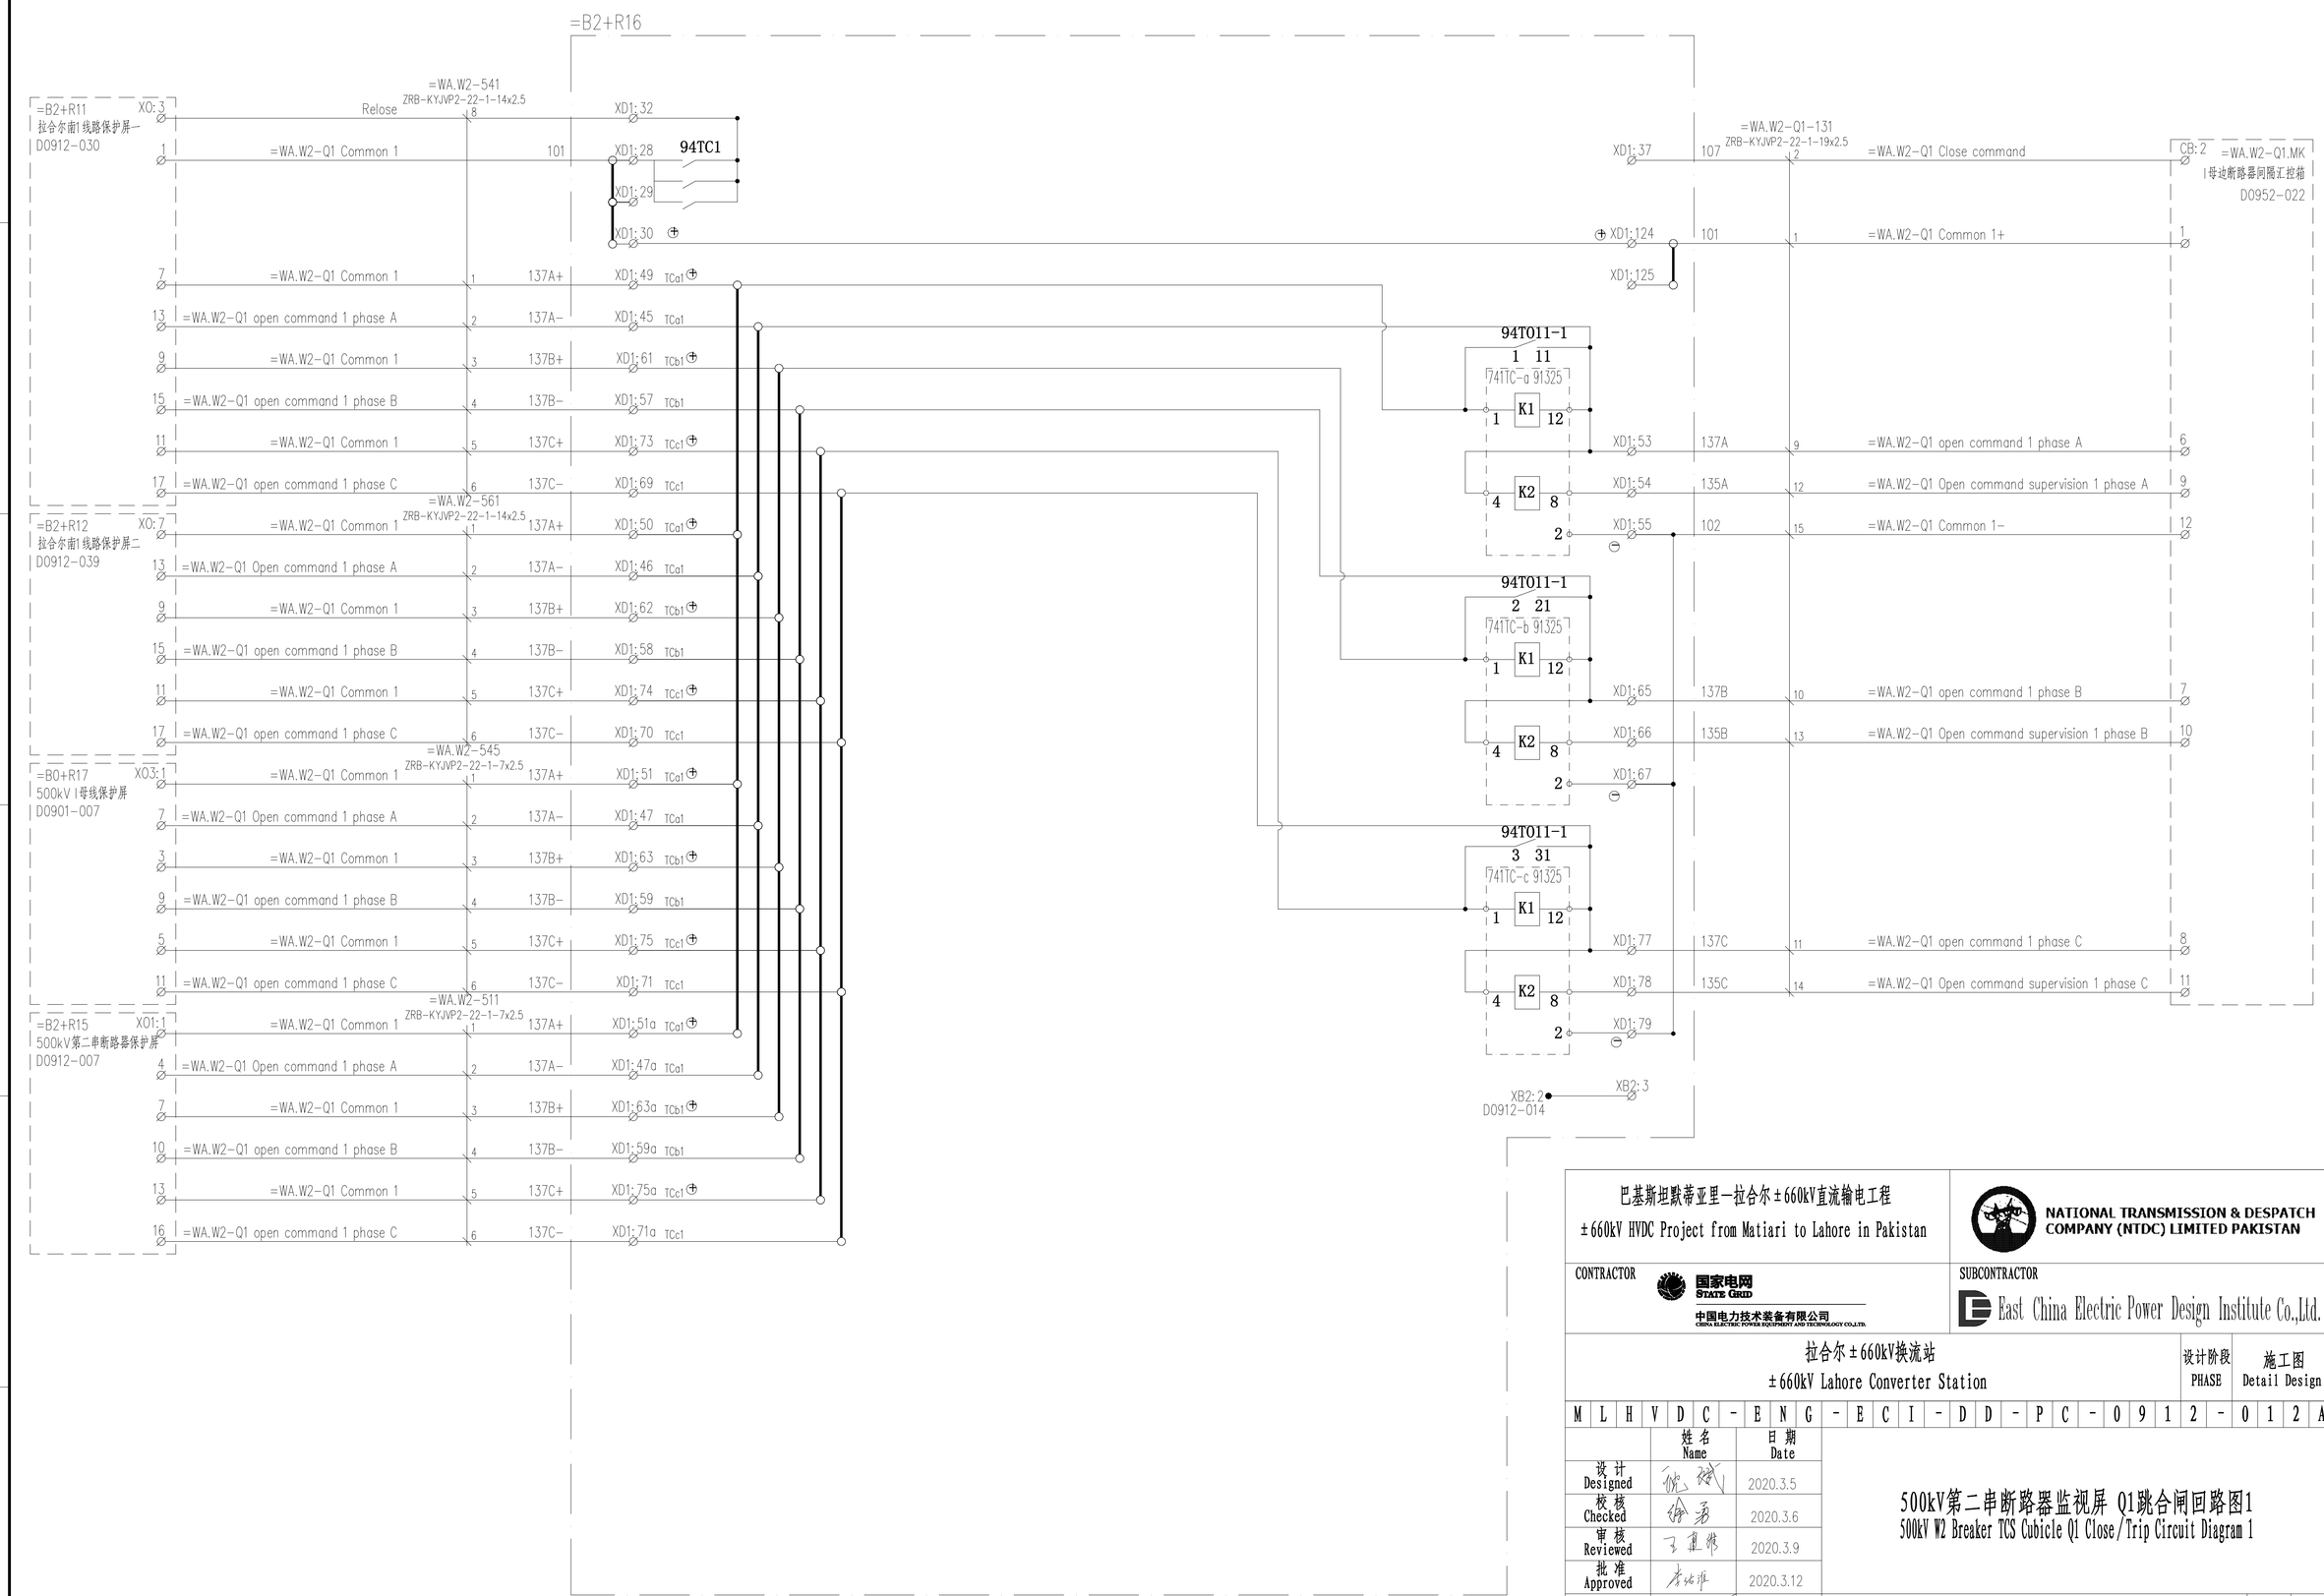

巴基斯坦默蒂亚里—拉合尔±660kV直流输电工程

±660kV HVDC Project from Matiari to Lahore in Pakistan

NATIONAL TRANSMISSION & DESPATCH COMPANY (NTDC) LIMITED PAKISTAN

CONTRACTOR 国家电网 STATE GRID 中国电力技术装备有限公司 CHINA ELECTRIC POWER EQUIPMENT AND TECHNOLOGY CO.,LTD.

SUBCONTRACTOR East China Electric Power Design Institute Co.,Ltd.

拉合尔±660kV换流站

±660kV Lahore Converter Station

设计阶段 PHASE: 施工图 Detail Design

MLHVDC-ENG-ECI-DD-PC-0912-012A

	姓名 Name	日期 Date
设计 Designed	倪 [illegible]	2020.3.5
校核 Checked	徐 [illegible]	2020.3.6
审核 Reviewed	王 [illegible]	2020.3.9
批准 Approved	李 [illegible]	2020.3.12

500kV第二串断路器监视屏 Q1跳合闸回路图1

500kV W2 Breaker TCS Cubicle Q1 Close/Trip Circuit Diagram 1

比例 Scale:

图号 DWG NO.: 30-B003701S-D0912-012

版本 REV.: A

420X594