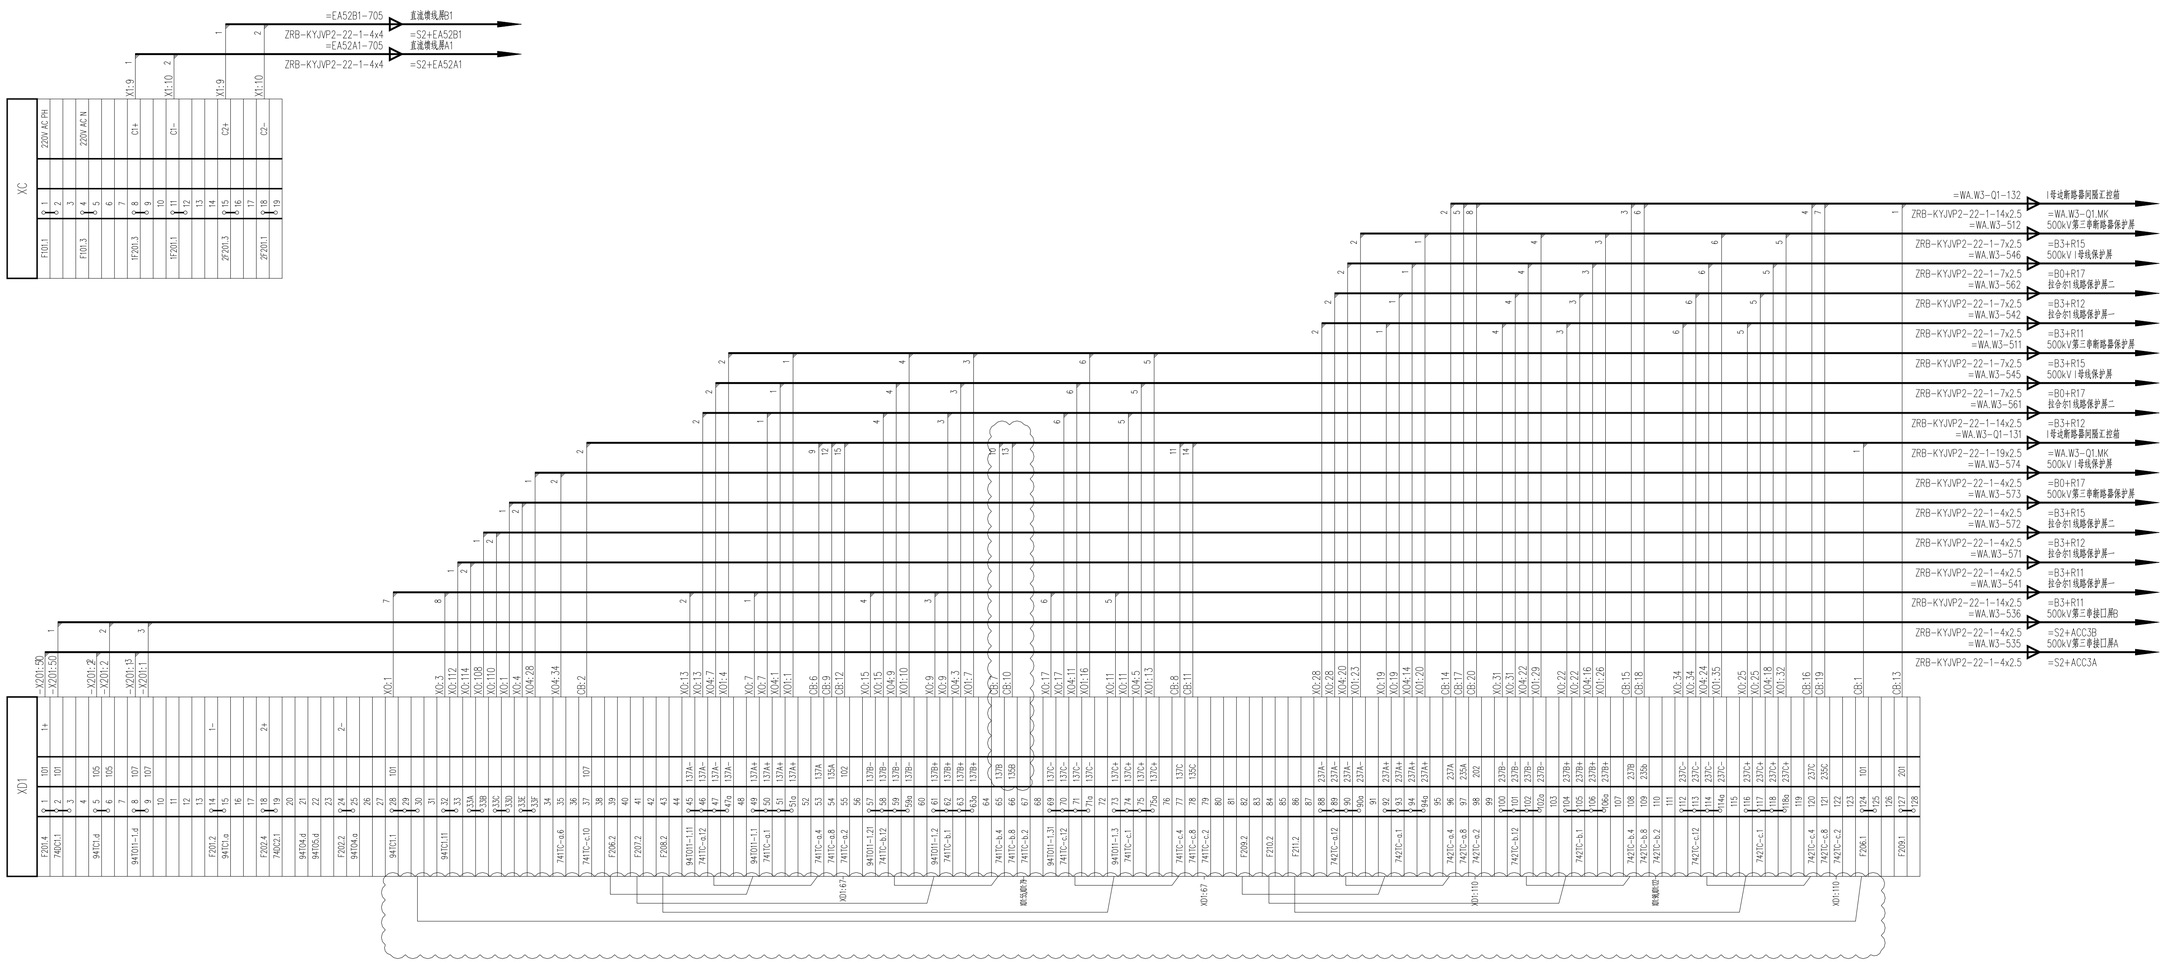

巴基斯坦默蒂亚里—拉合尔±660kV直流输电工程 ±660kV HVDC Project from Matiari to Lahore in Pakistan	NATIONAL TRANSMISSION & DESPATCH COMPANY (NTDC) LIMITED PAKISTAN
CONTRACTOR 国家电网 STATE GRID 中国电力技术装备有限公司 CHINA ELECTRIC POWER EQUIPMENT AND TECHNOLOGY CO.,LTD.	SUBCONTRACTOR East China Electric Power Design Institute Co.,Ltd.
拉合尔±660kV换流站 ±660kV Lahore Converter Station	设计阶段 PHASE: 施工图 Detail Design

M L H V D C - E N G - E C I - D D - P C - 0 9 1 3 - 0 4 7 A

	姓名 Name	日期 Date
设计 Designed	[illegible]	2020.3.5
校核 Checked	[illegible]	2020.3.6
审核 Reviewed		
批准 Approved	[illegible]	2020.3.9
比例 Scale		

500kV第三串断路器监视屏 端子排接线图1
500kV W3 Breaker TCS Cubicle Terminal Block Diagram 1

图号 DWG NO. 30-B003701S-D0913-047 版本 REV. A

594X841