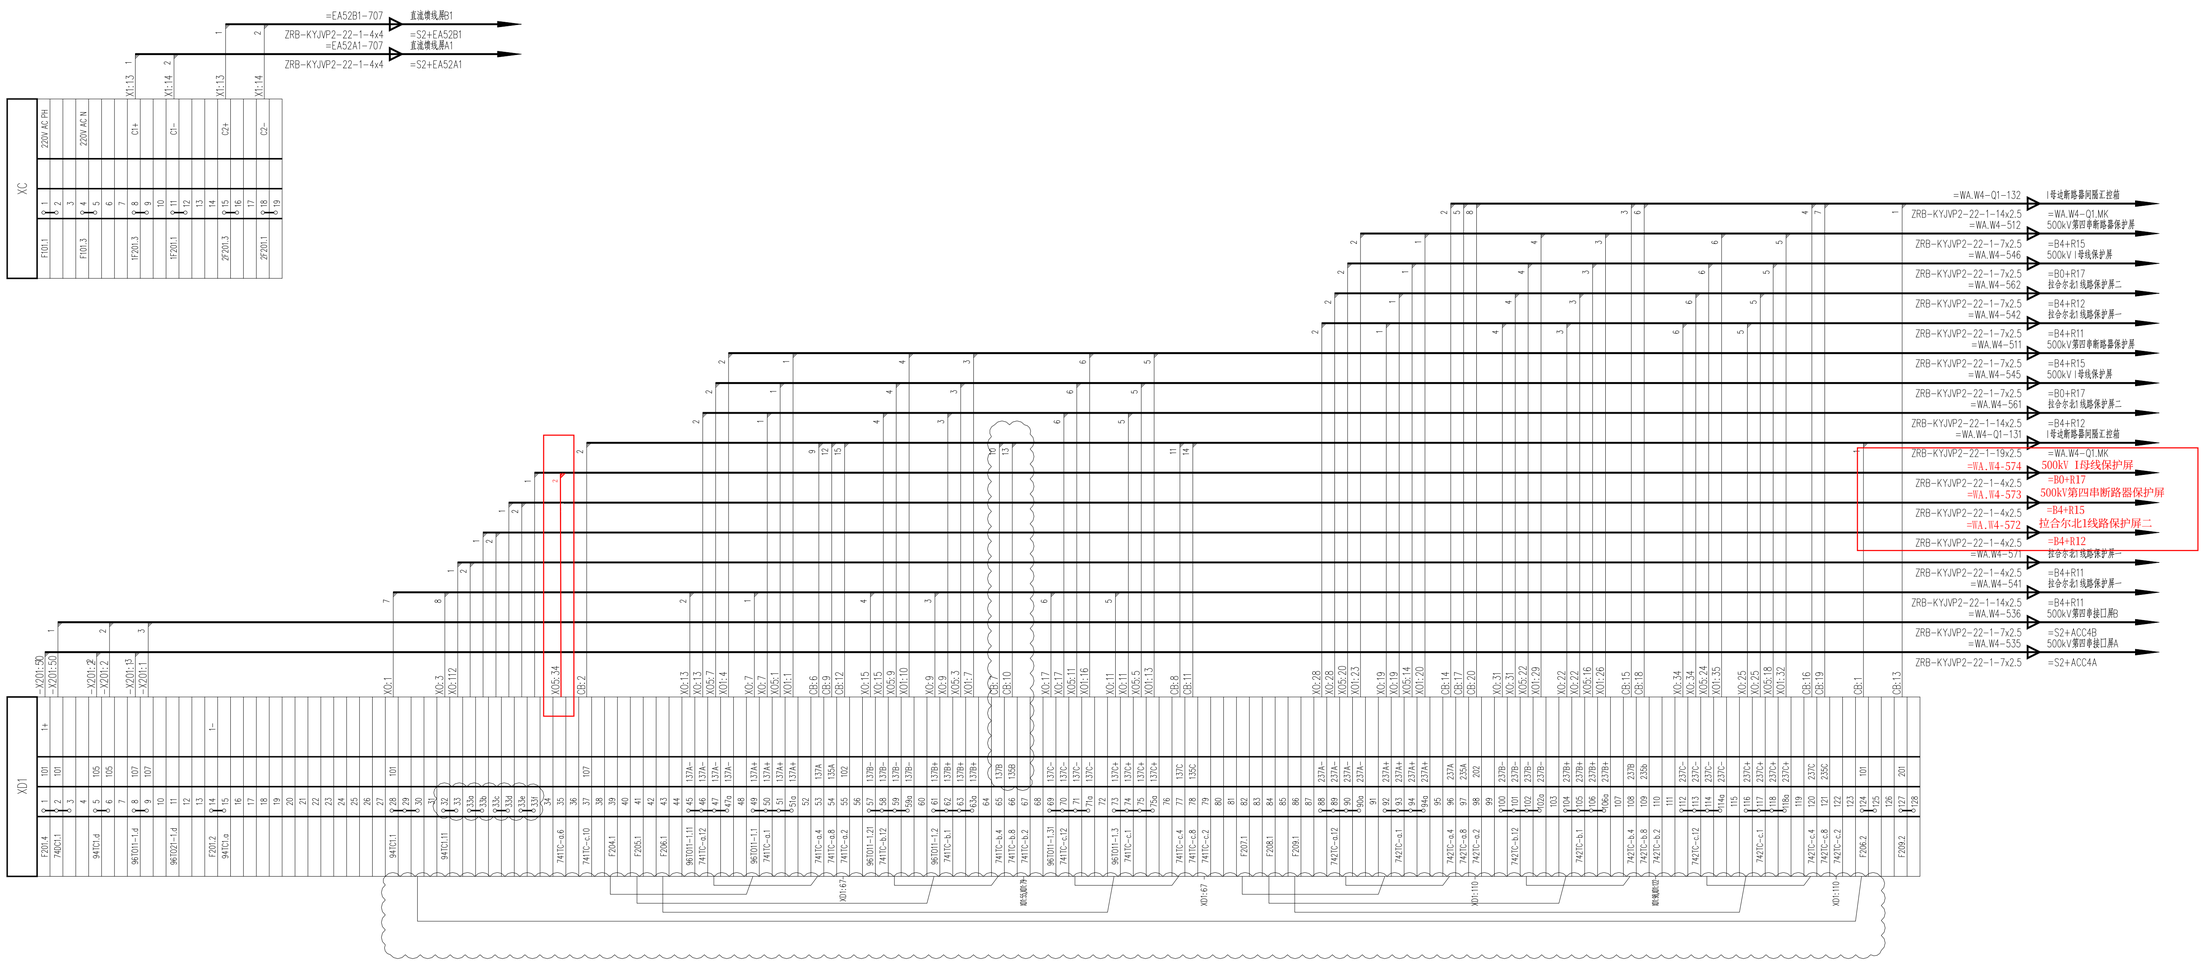


巴基斯坦默蒂亚里—拉合尔±660kV直流输电工程

±660kV HVDC Project from Matiari to Lahore in Pakistan

NATIONAL TRANSMISSION & DESPATCH COMPANY (NTDC) LIMITED PAKISTAN

CONTRACTOR 国家电网 STATE GRID 中国电力技术装备有限公司 CHINA ELECTRIC POWER EQUIPMENT AND TECHNOLOGY CO.,LTD.

SUBCONTRACTOR East China Electric Power Design Institute Co.,Ltd.

拉合尔±660kV换流站

±660kV Lahore Converter Station

设计阶段 PHASE: 施工图 Detail Design

M L H V D C - E N G - E C I - D D - P C - 0 9 1 4 - 0 6 7 A

| | 姓名 Name | 日期 Date |
|---|---|---|
| 设计 Designed | [illegible] | 2020.3.5 |
| 校核 Checked | [illegible] | 2020.3.6 |
| 审核 Reviewed | | |
| 批准 Approved | [illegible] | 2020.3.9 |
| 比例 Scale | | |

500kV第四串断路器监视屏 端子排接线图1

500kV W4 Breaker TCS Cubicle Terminal Block Diagram 1

图号 DWG NO. 30-B003701S-D0914-067

版本 REV. A

594X841