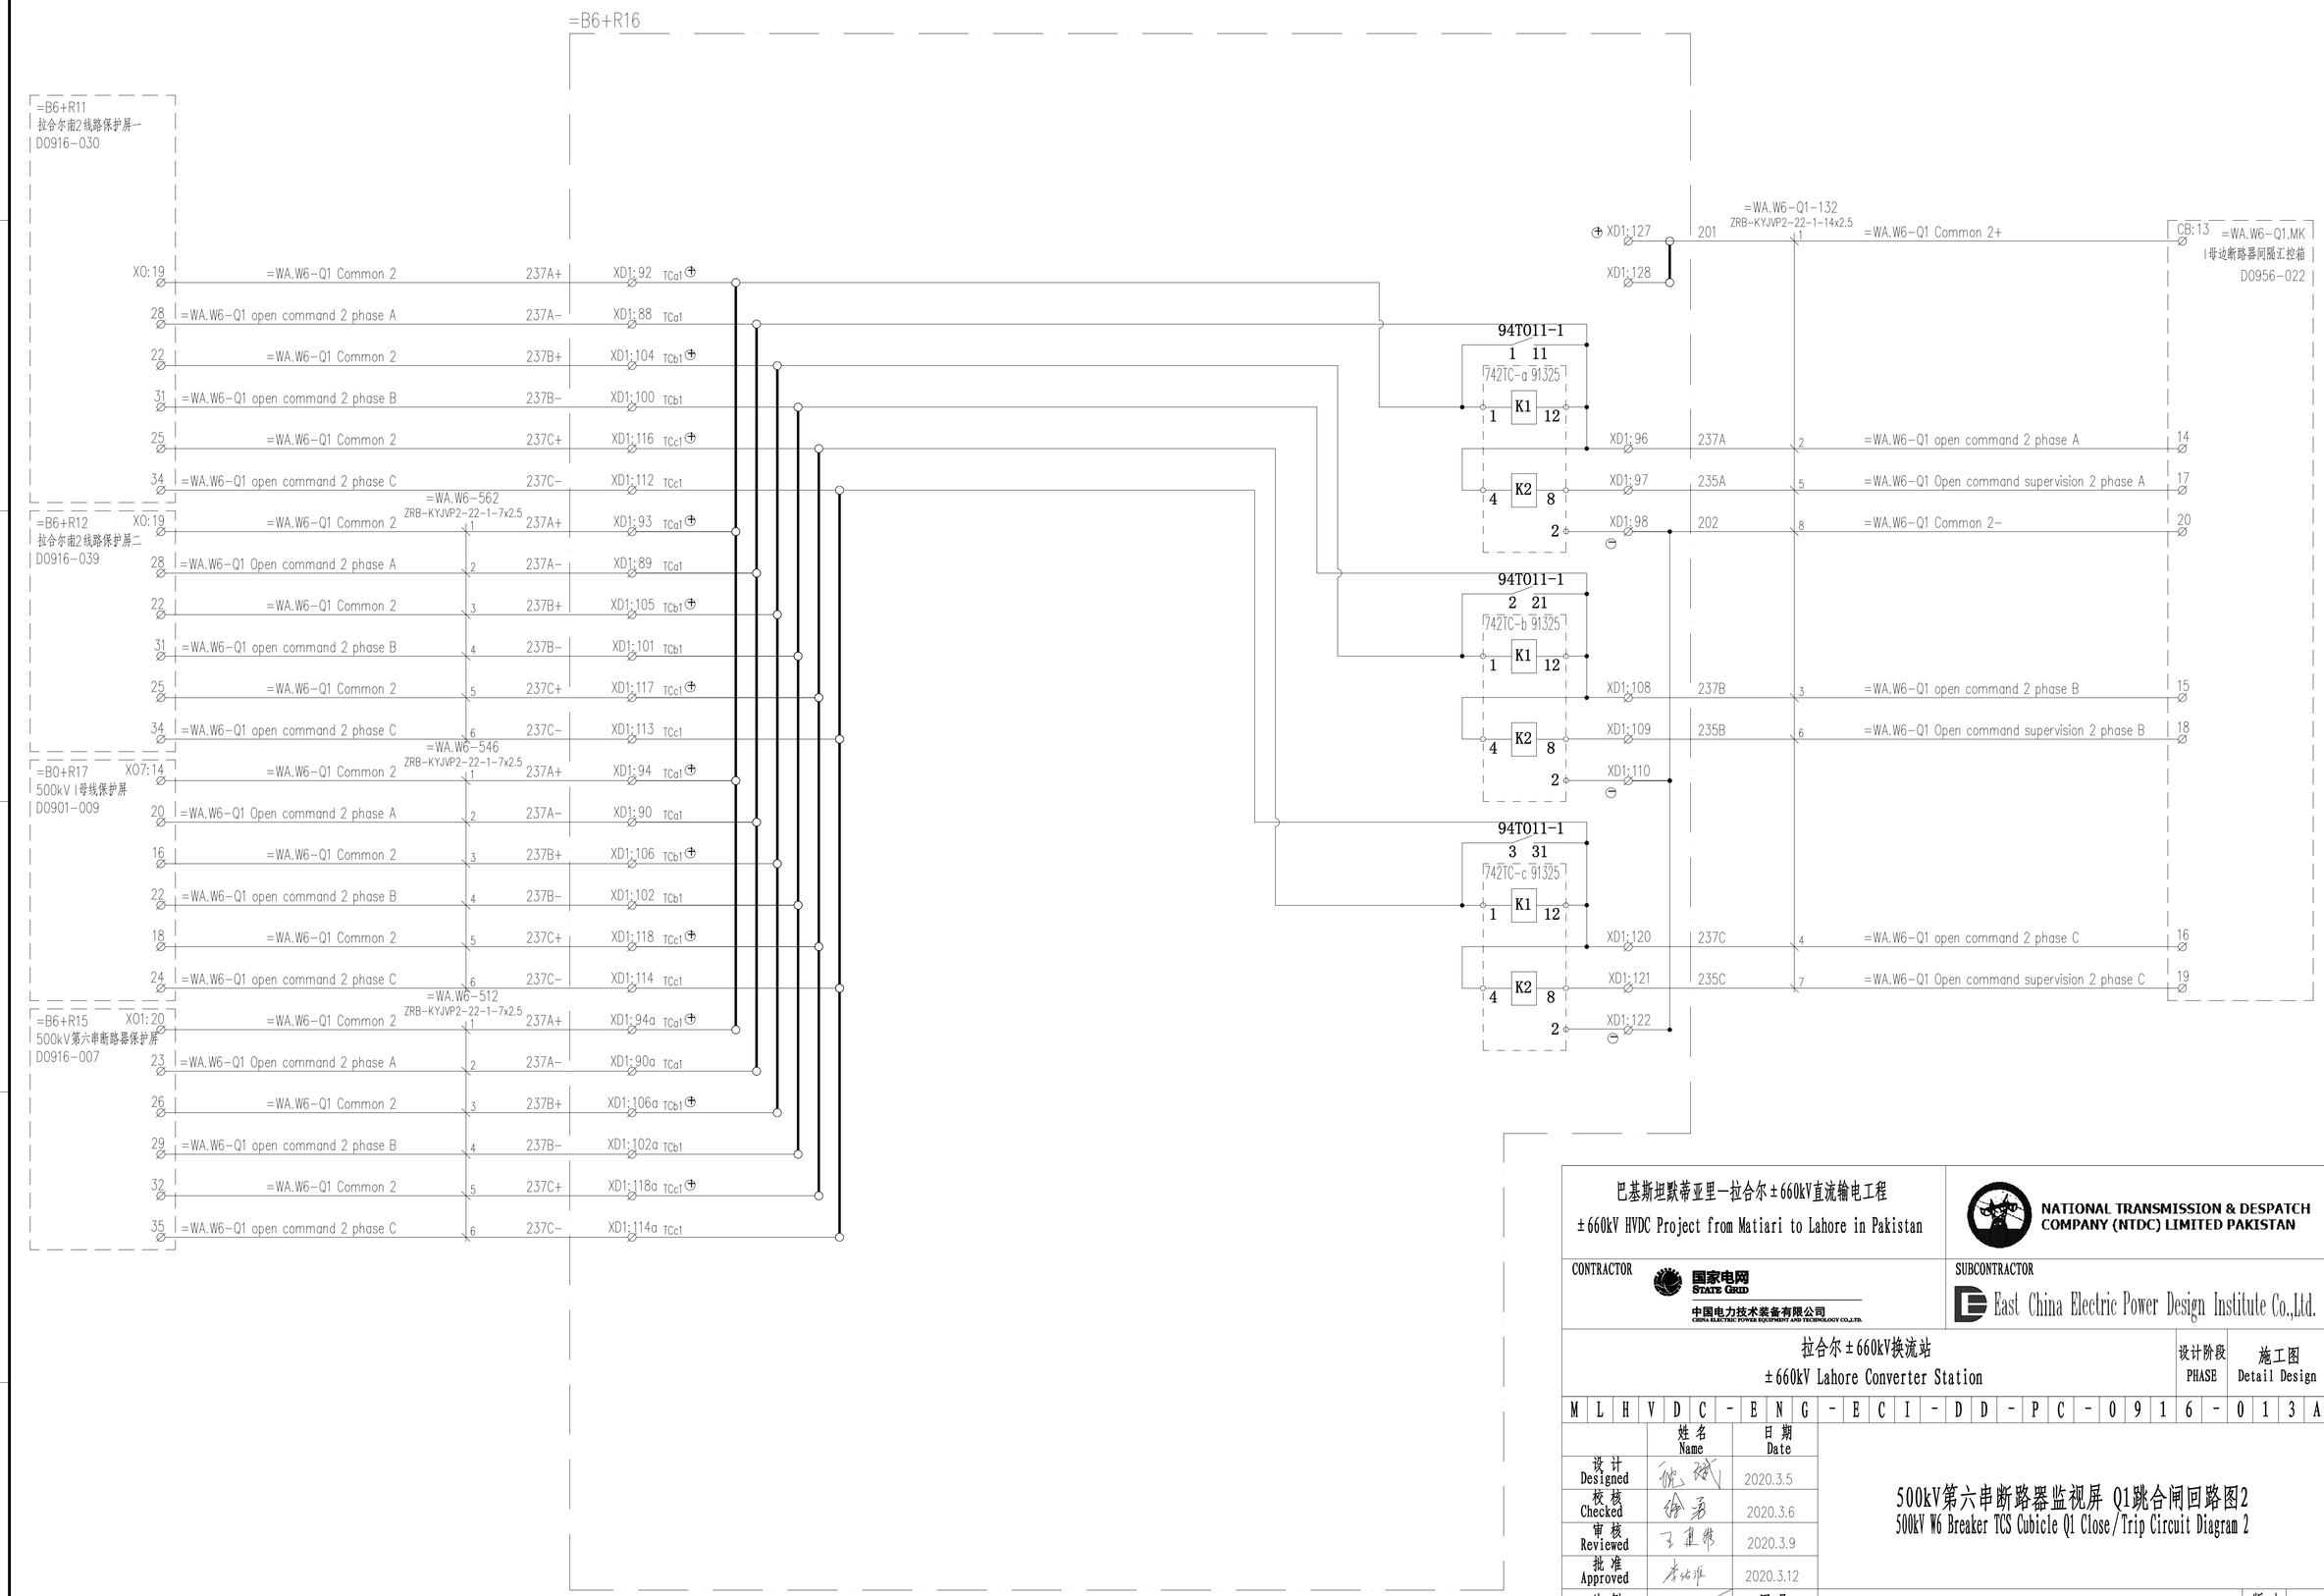

巴基斯坦默蒂亚里—拉合尔±660kV直流输电工程

±660kV HVDC Project from Matiari to Lahore in Pakistan

NATIONAL TRANSMISSION & DESPATCH COMPANY (NTDC) LIMITED PAKISTAN

CONTRACTOR 国家电网 STATE GRID 中国电力技术装备有限公司 CHINA ELECTRIC POWER EQUIPMENT AND TECHNOLOGY CO.,LTD.

SUBCONTRACTOR East China Electric Power Design Institute Co.,Ltd.

拉合尔±660kV换流站

±660kV Lahore Converter Station

设计阶段 PHASE: 施工图 Detail Design

M L H V D C - E N G - E C I - D D - P C - 0 9 1 6 - 0 1 3 A

	姓名 Name	日期 Date
设计 Designed		2020.3.5
校核 Checked		2020.3.6
审核 Reviewed		2020.3.9
批准 Approved		2020.3.12
比例 Scale		图号 DWG NO.

500kV第六串断路器监视屏 Q1跳合闸回路图2

500kV W6 Breaker TCS Cubicle Q1 Close/Trip Circuit Diagram 2

30-B003701S-D0916-013

版本 REV. A

420X594