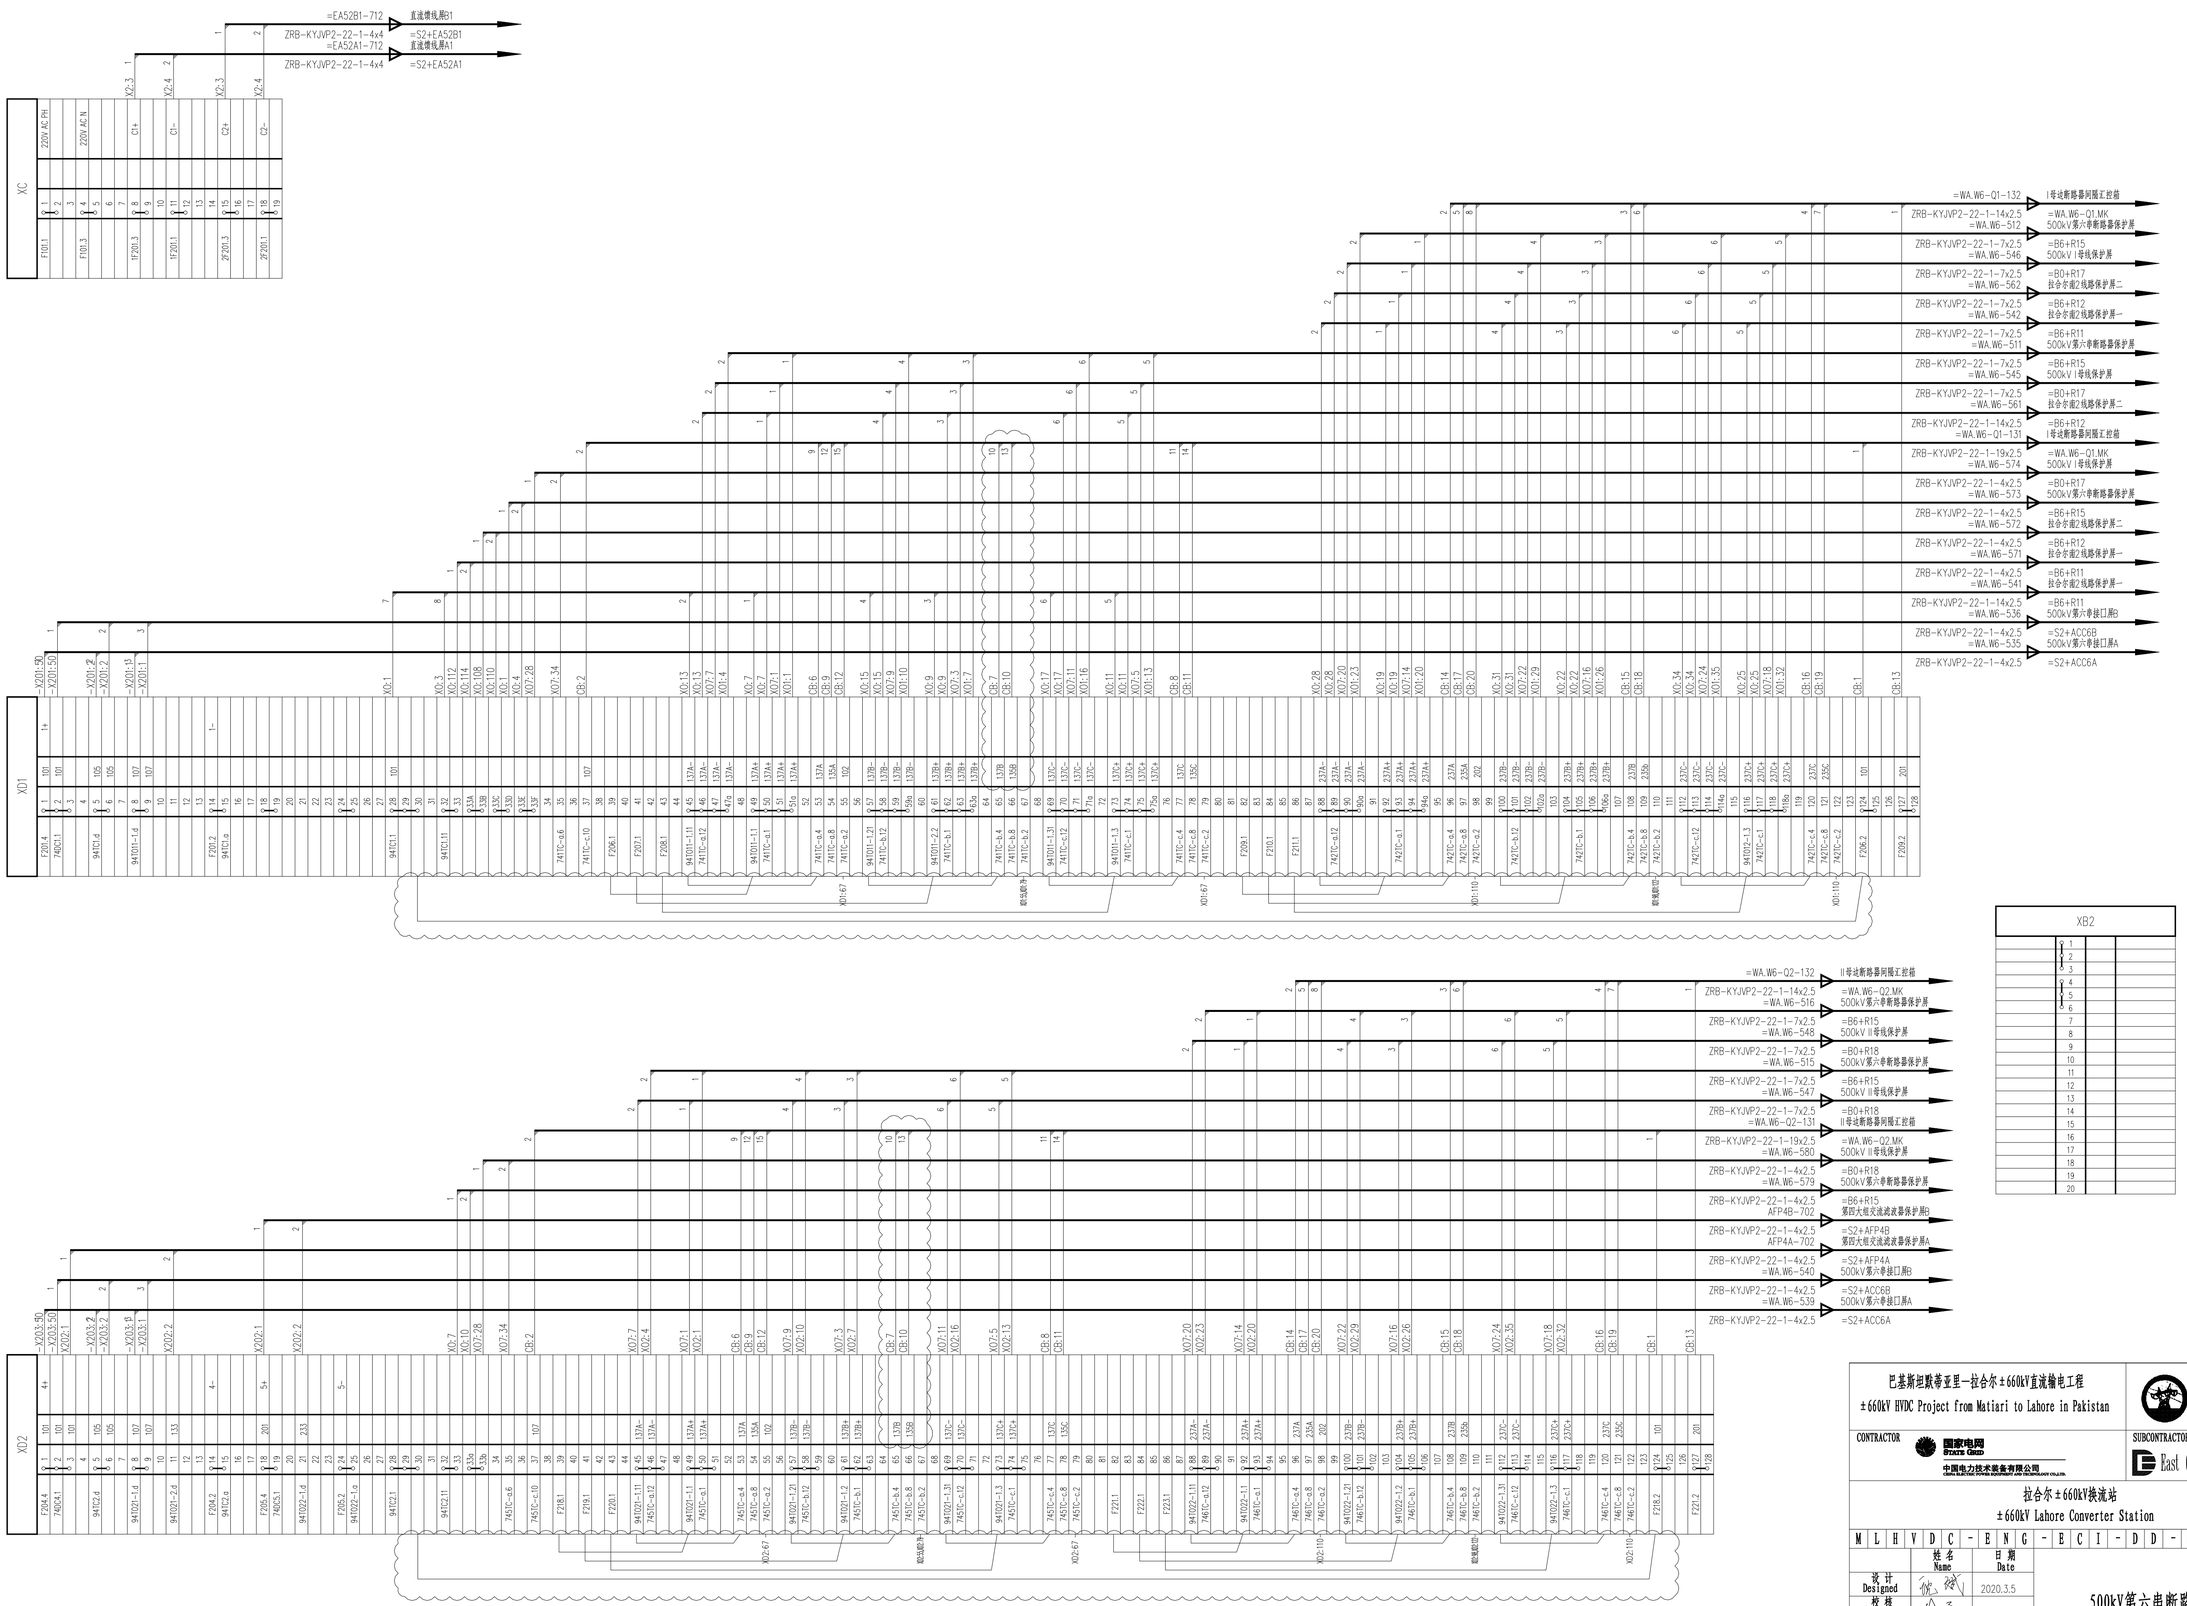

巴基斯坦默蒂亚里—拉合尔±660kV直流输电工程

±660kV HVDC Project from Matiari to Lahore in Pakistan

NATIONAL TRANSMISSION & DESPATCH COMPANY (NTDC) LIMITED PAKISTAN

CONTRACTOR 国家电网 State Grid 中国电力技术装备有限公司 CHINA ELECTRIC POWER TECHNOLOGY EQUIPMENT CO.,LTD.

SUBCONTRACTOR East China Electric Power Design Institute Co.,Ltd.

拉合尔±660kV换流站

±660kV Lahore Converter Station

设计阶段 PHASE: 施工图 Detail Design

MLHVDC-ENG-ECI-DD-PC-0916-045A

	姓名 Name	日期 Date
设计 Designed	张	2020.3.5
校核 Checked	徐	2020.3.6
审核 Reviewed		
批准 Approved	子	2020.3.9

500kV第六串断路器监视屏 端子排接线图1

500kV W6 Breaker TCS Cubicle Terminal Block Diagram 1

比例 Scale: /

图号 DWG NO.: 30-B003701S-D0916-045

版本 REV.: A

594X841