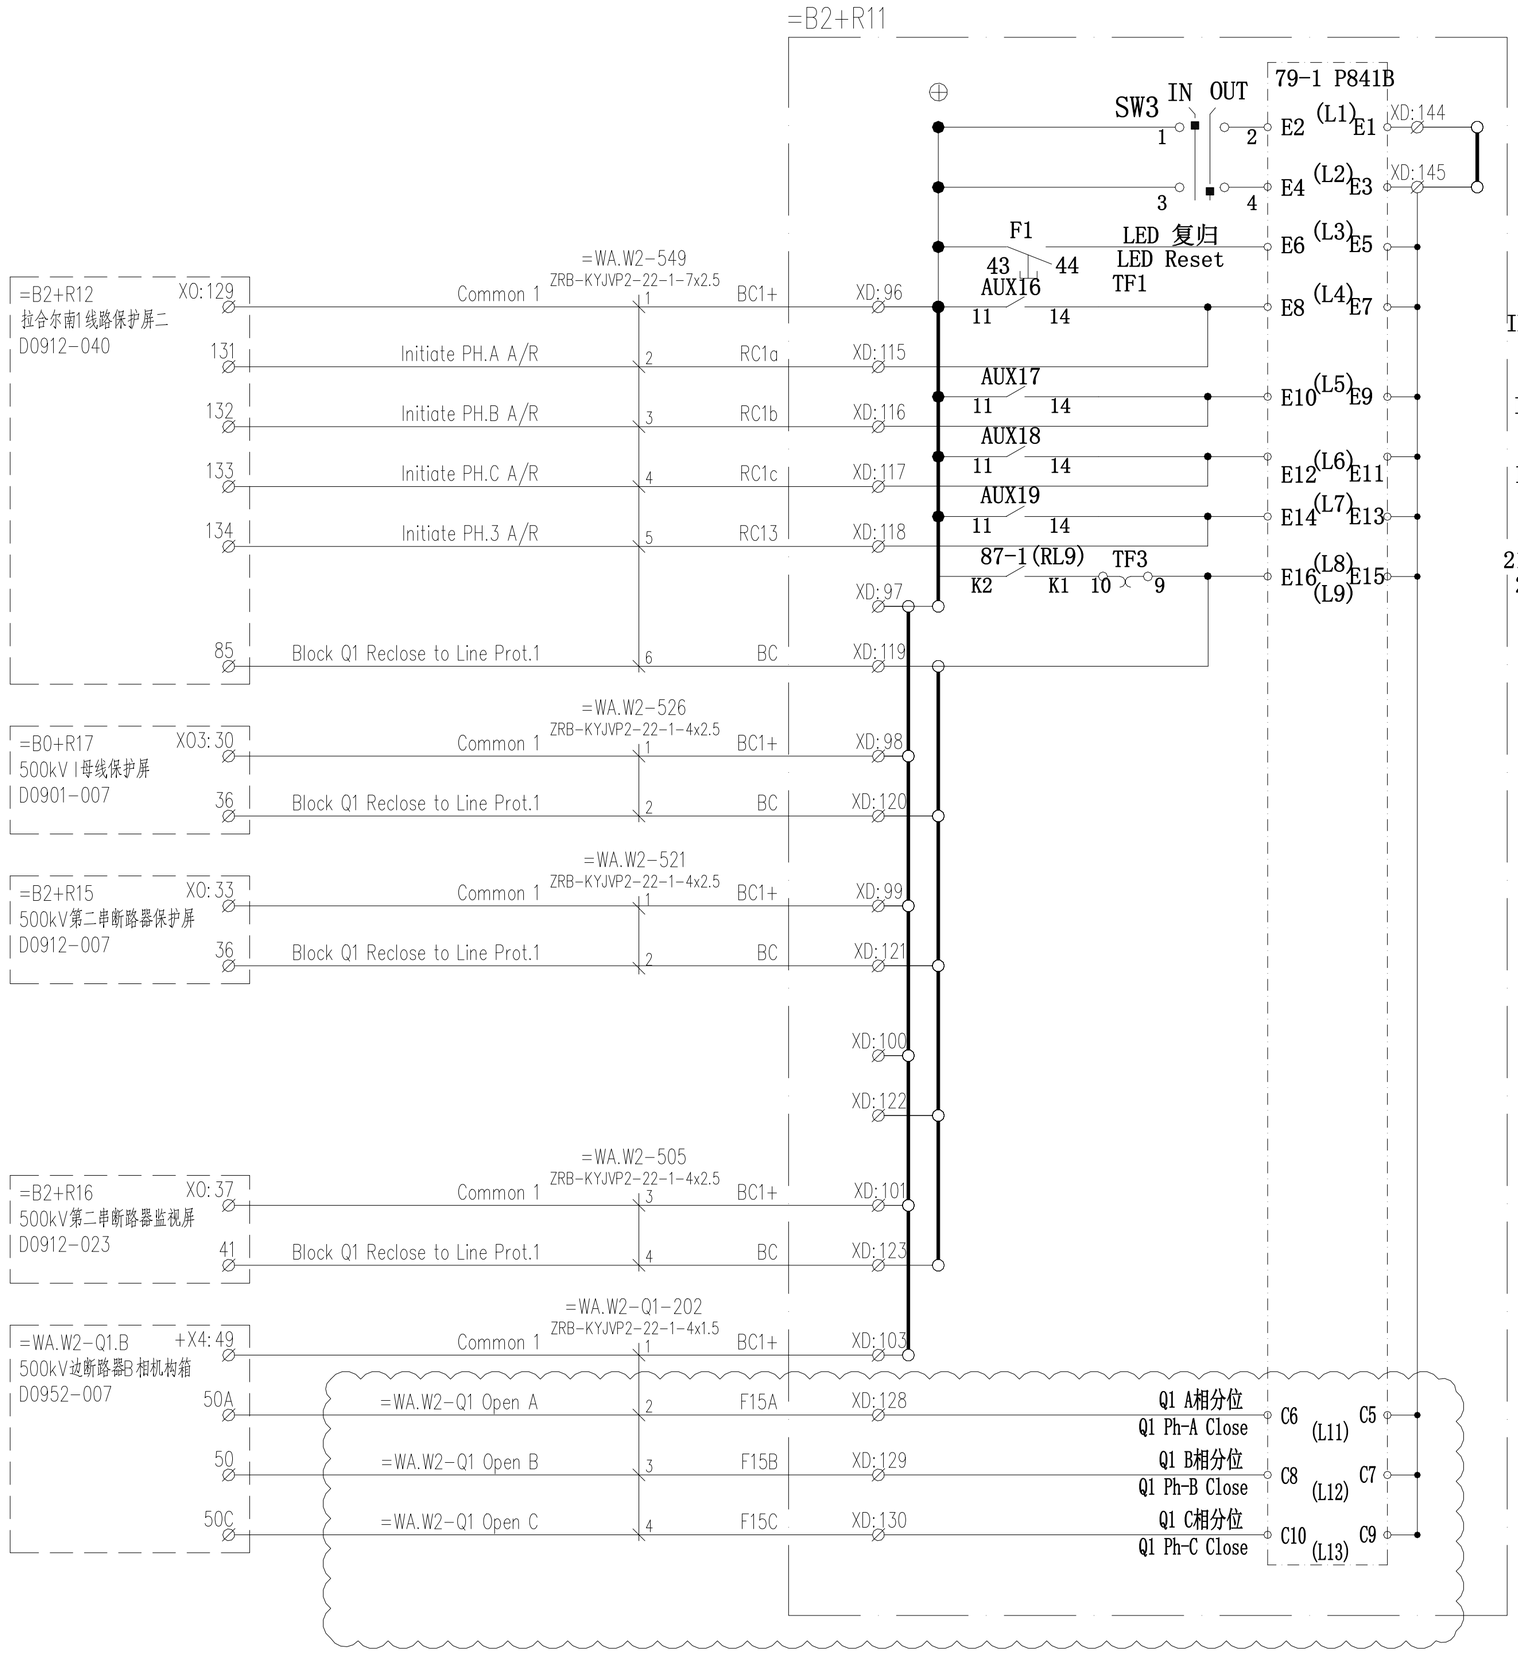

L2 L1	重合闸方式 A/R MODE
0 0	AR OFF
0 1	1-POLE
0 1	3-POLE
1 1	1/3-POLE

启动A相重合
INITIATE PH.A A/R

启动B相重合
INITIATE PH.B A/R

启动C相重合
INITIATE PH.C A/R

启动三相重合
INITIATE PH.3 A/R

21-1 距离/短引线/SOTF
21-1 Z2/Z3/50S/SOTF

闭锁重合闸
Block A/R

巴基斯坦默蒂亚里—拉合尔±660kV直流输电工程
±660kV HVDC Project from Matiari to Lahore in Pakistan

NATIONAL TRANSMISSION & DESPATCH COMPANY (NTDC) LIMITED PAKISTAN

CONTRACTOR 国家电网 STATE GRID 中国电力技术装备有限公司 CHINA ELECTRIC POWER EQUIPMENT AND TECHNOLOGY CO.,LTD.

SUBCONTRACTOR East China Electric Power Design Institute Co.,Ltd.

拉合尔±660kV换流站
±660kV Lahore Converter Station

设计阶段 PHASE: 施工图 Detail Design

M L H V D C - E N G - E C I - D D - P C - 0 9 2 1 - 0 2 9 A

	姓名 Name	日期 Date
设计 Designed		2020.3.5
校核 Checked		2020.3.6
审核 Reviewed		2020.3.9
批准 Approved		2020.3.12
比例 Scale		图号 DWG NO.

500kV线路保护屏(R11) 79-1 P841-B直流回路图
500kV Line Distance Protection(R11) Cubicle 79-1 P841-B DC Circuit Diagram

30-B003701S-D0912-029

版本 REV. A

297X420