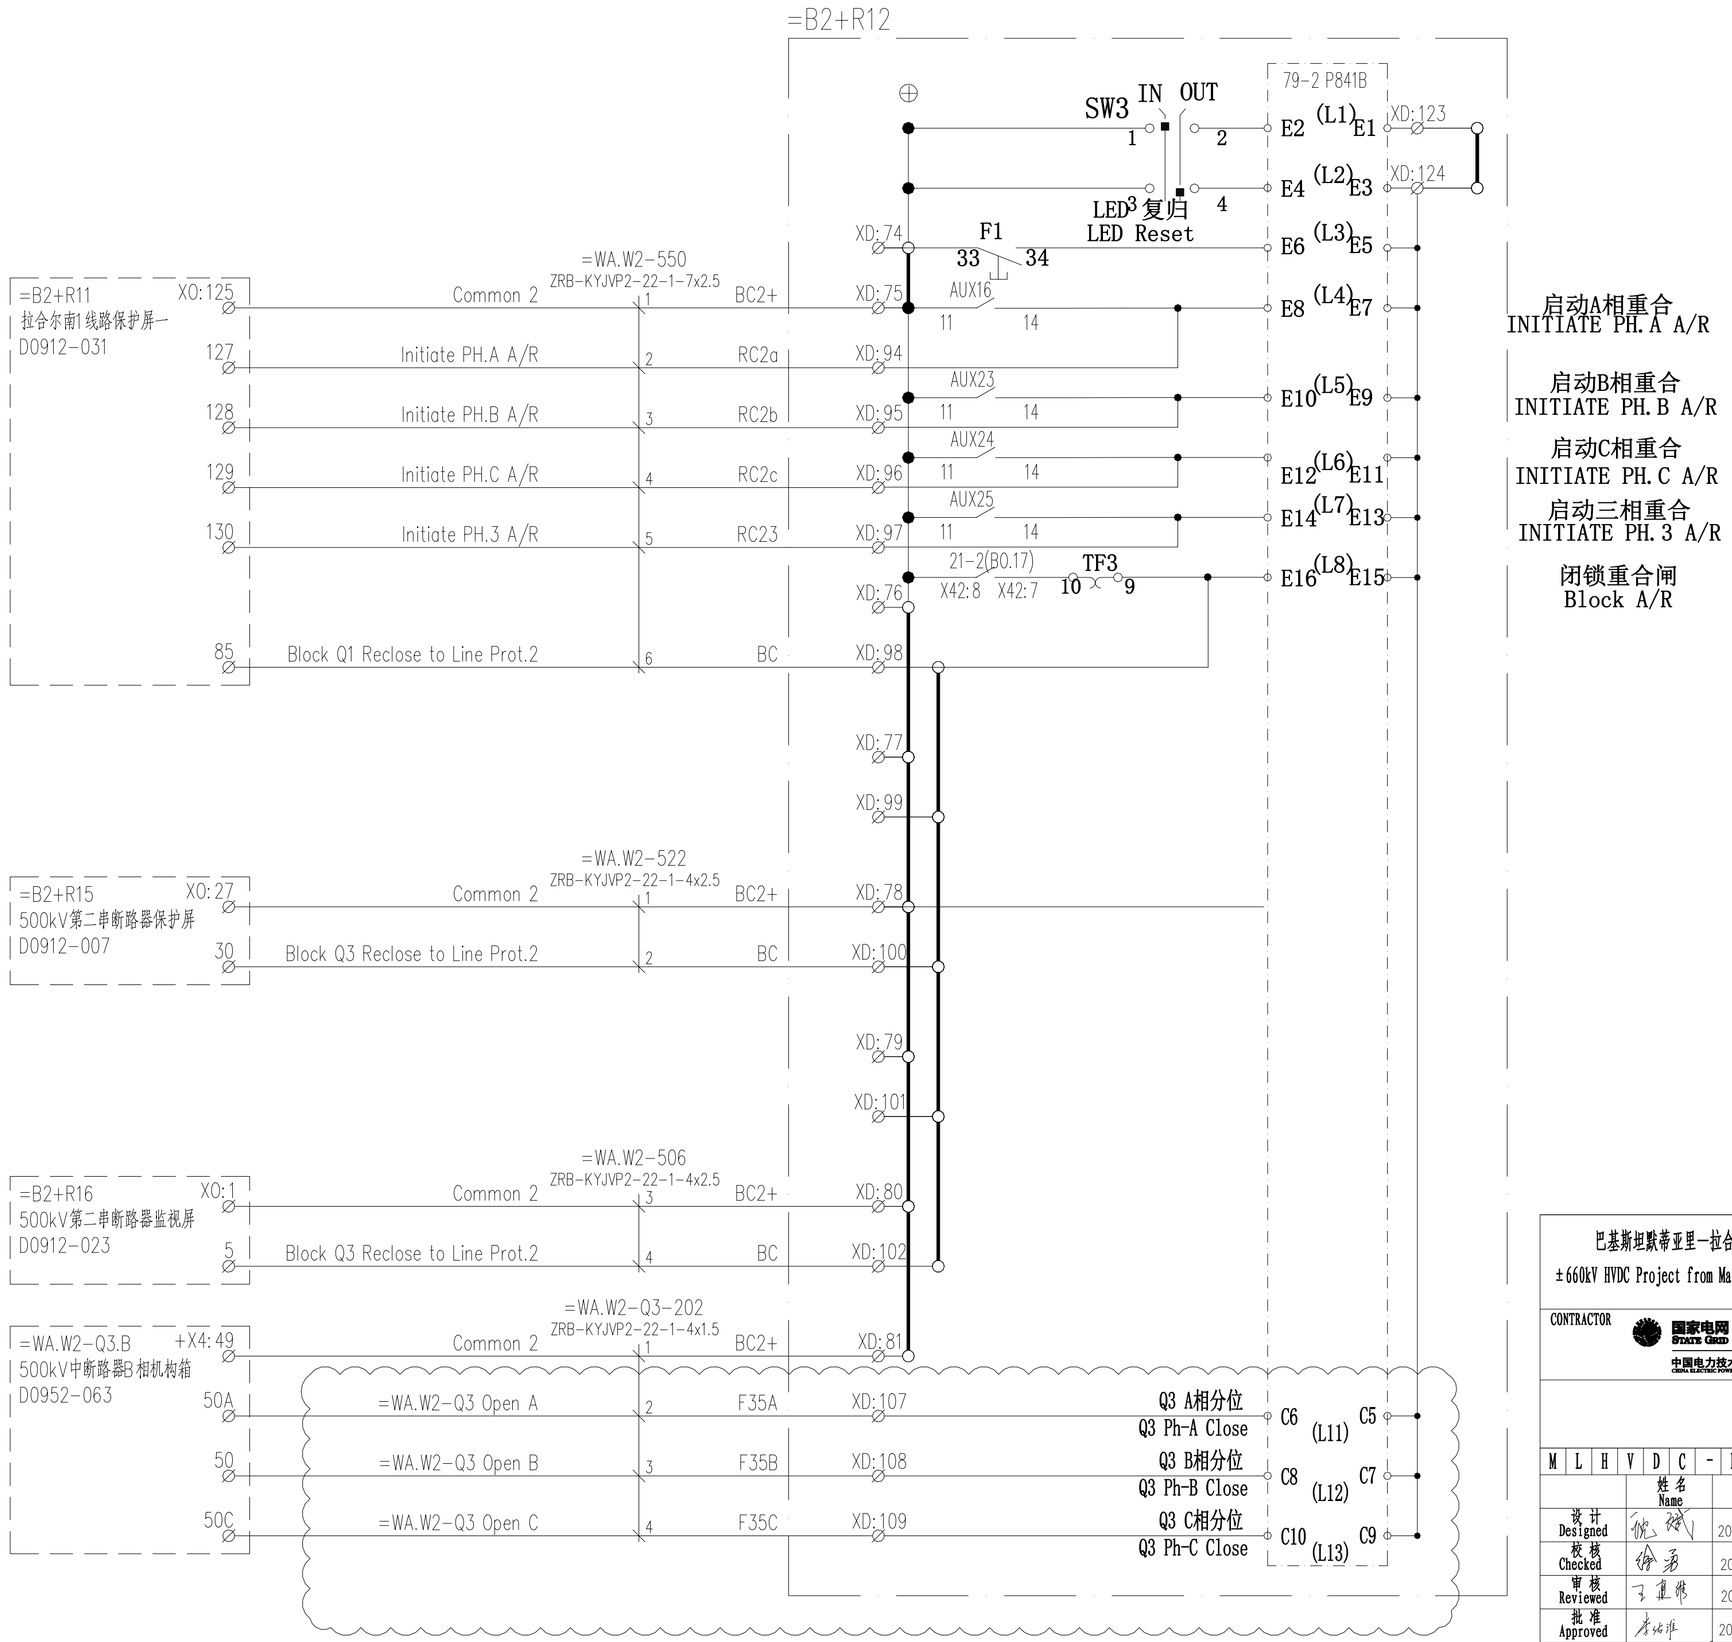


## SW3 (A/R IN/OUT Switch)
## LW39-16C-90B-22/2

| Contacts \ Lettering | IN (Angle 45°) | OUT (Angle 45°) |
|---|---|---|
| 1-2 | X | |
| 3-4 | | X |

巴基斯坦默蒂亚里—拉合尔±660kV直流输电工程

±660kV HVDC Project from Matiari to Lahore in Pakistan

NATIONAL TRANSMISSION & DESPATCH COMPANY (NTDC) LIMITED PAKISTAN

CONTRACTOR 国家电网 STATE GRID 中国电力技术装备有限公司 CHINA ELECTRIC POWER EQUIPMENT AND TECHNOLOGY CO.,LTD.

SUBCONTRACTOR East China Electric Power Design Institute Co.,Ltd.

拉合尔±660kV换流站

±660kV Lahore Converter Station

设计阶段 PHASE: 施工图 Detail Design

M L H V D C - E N G - E C I - D D - P C - 0 9 2 1 - 0 3 8 A

| | 姓名 Name | 日期 Date |
|---|---|---|
| 设计 Designed | 倪斌 | 2020.3.5 |
| 校核 Checked | 徐勇 | 2020.3.6 |
| 审核 Reviewed | 王建华 | 2020.3.9 |
| 批准 Approved | 李培雄 | 2020.3.12 |
| 比例 Scale | | 图号 DWG NO. |

500kV线路保护屏(R12) 79-2 P841-A直流回路图

500kV Line Distance Protection(R12) Cubicle 79-2 P841-A DC Circuit Diagram

30-B003701S-D0912-038

版本 REV. A

297X420