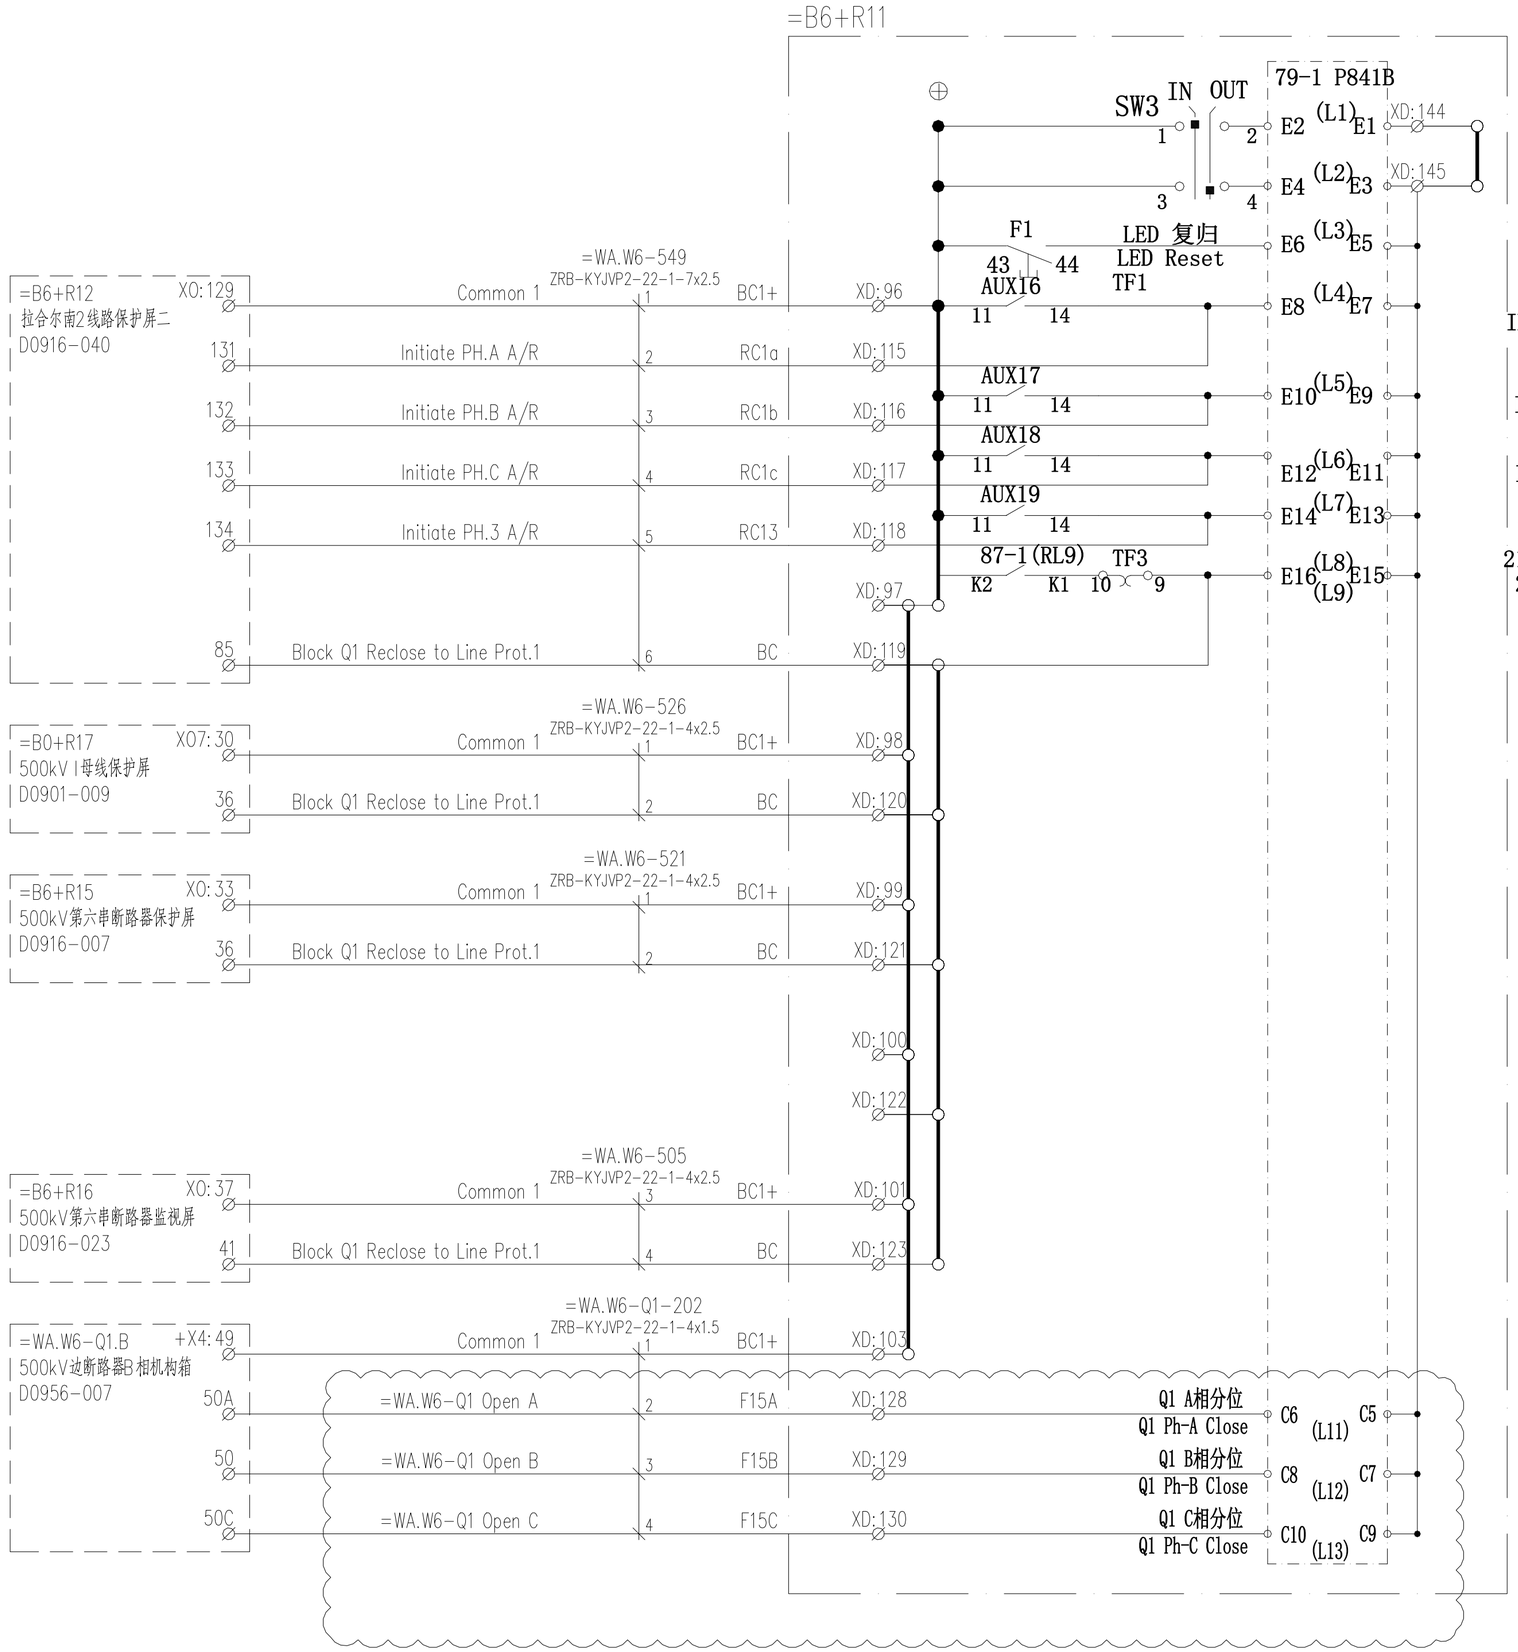


| L2 L1 | 重合闸方式 A/R MODE |
|---|---|
| 0 0 | AR OFF |
| 0 1 | 1-POLE |
| 0 1 | 3-POLE |
| 1 1 | 1/3-POLE |

启动A相重合
INITIATE PH.A A/R

启动B相重合
INITIATE PH.B A/R

启动C相重合
INITIATE PH.C A/R

启动三相重合
INITIATE PH.3 A/R

21-1 距离/短引线/SOTF
21-1 Z2/Z3/50S/SOTF

闭锁重合闸
Block A/R

巴基斯坦默蒂亚里—拉合尔±660kV直流输电工程
±660kV HVDC Project from Matiari to Lahore in Pakistan

NATIONAL TRANSMISSION & DESPATCH COMPANY (NTDC) LIMITED PAKISTAN

CONTRACTOR 国家电网 STATE GRID 中国电力技术装备有限公司 CHINA ELECTRIC POWER EQUIPMENT AND TECHNOLOGY CO.,LTD.

SUBCONTRACTOR East China Electric Power Design Institute Co.,Ltd.

拉合尔±660kV换流站
±660kV Lahore Converter Station

设计阶段 PHASE: 施工图 Detail Design

M L H V D C - E N G - E C I - D D - P C - 0 9 6 1 - 0 2 9 A

| | 姓名 Name | 日期 Date |
|---|---|---|
| 设计 Designed | 杨斌 | 2020.3.5 |
| 校核 Checked | 徐勇 | 2020.3.6 |
| 审核 Reviewed | 王建伟 | 2020.3.9 |
| 批准 Approved | 李炳雄 | 2020.3.12 |
| 比例 Scale | | 图号 DWG NO. |

500kV线路保护屏(R11) 79-1 P841-B直流回路图
500kV Line Distance Protection(R11) Cubicle 79-1 P841-B DC Circuit Diagram

30-B003701S-D0916-029

版本 REV. A

297X420