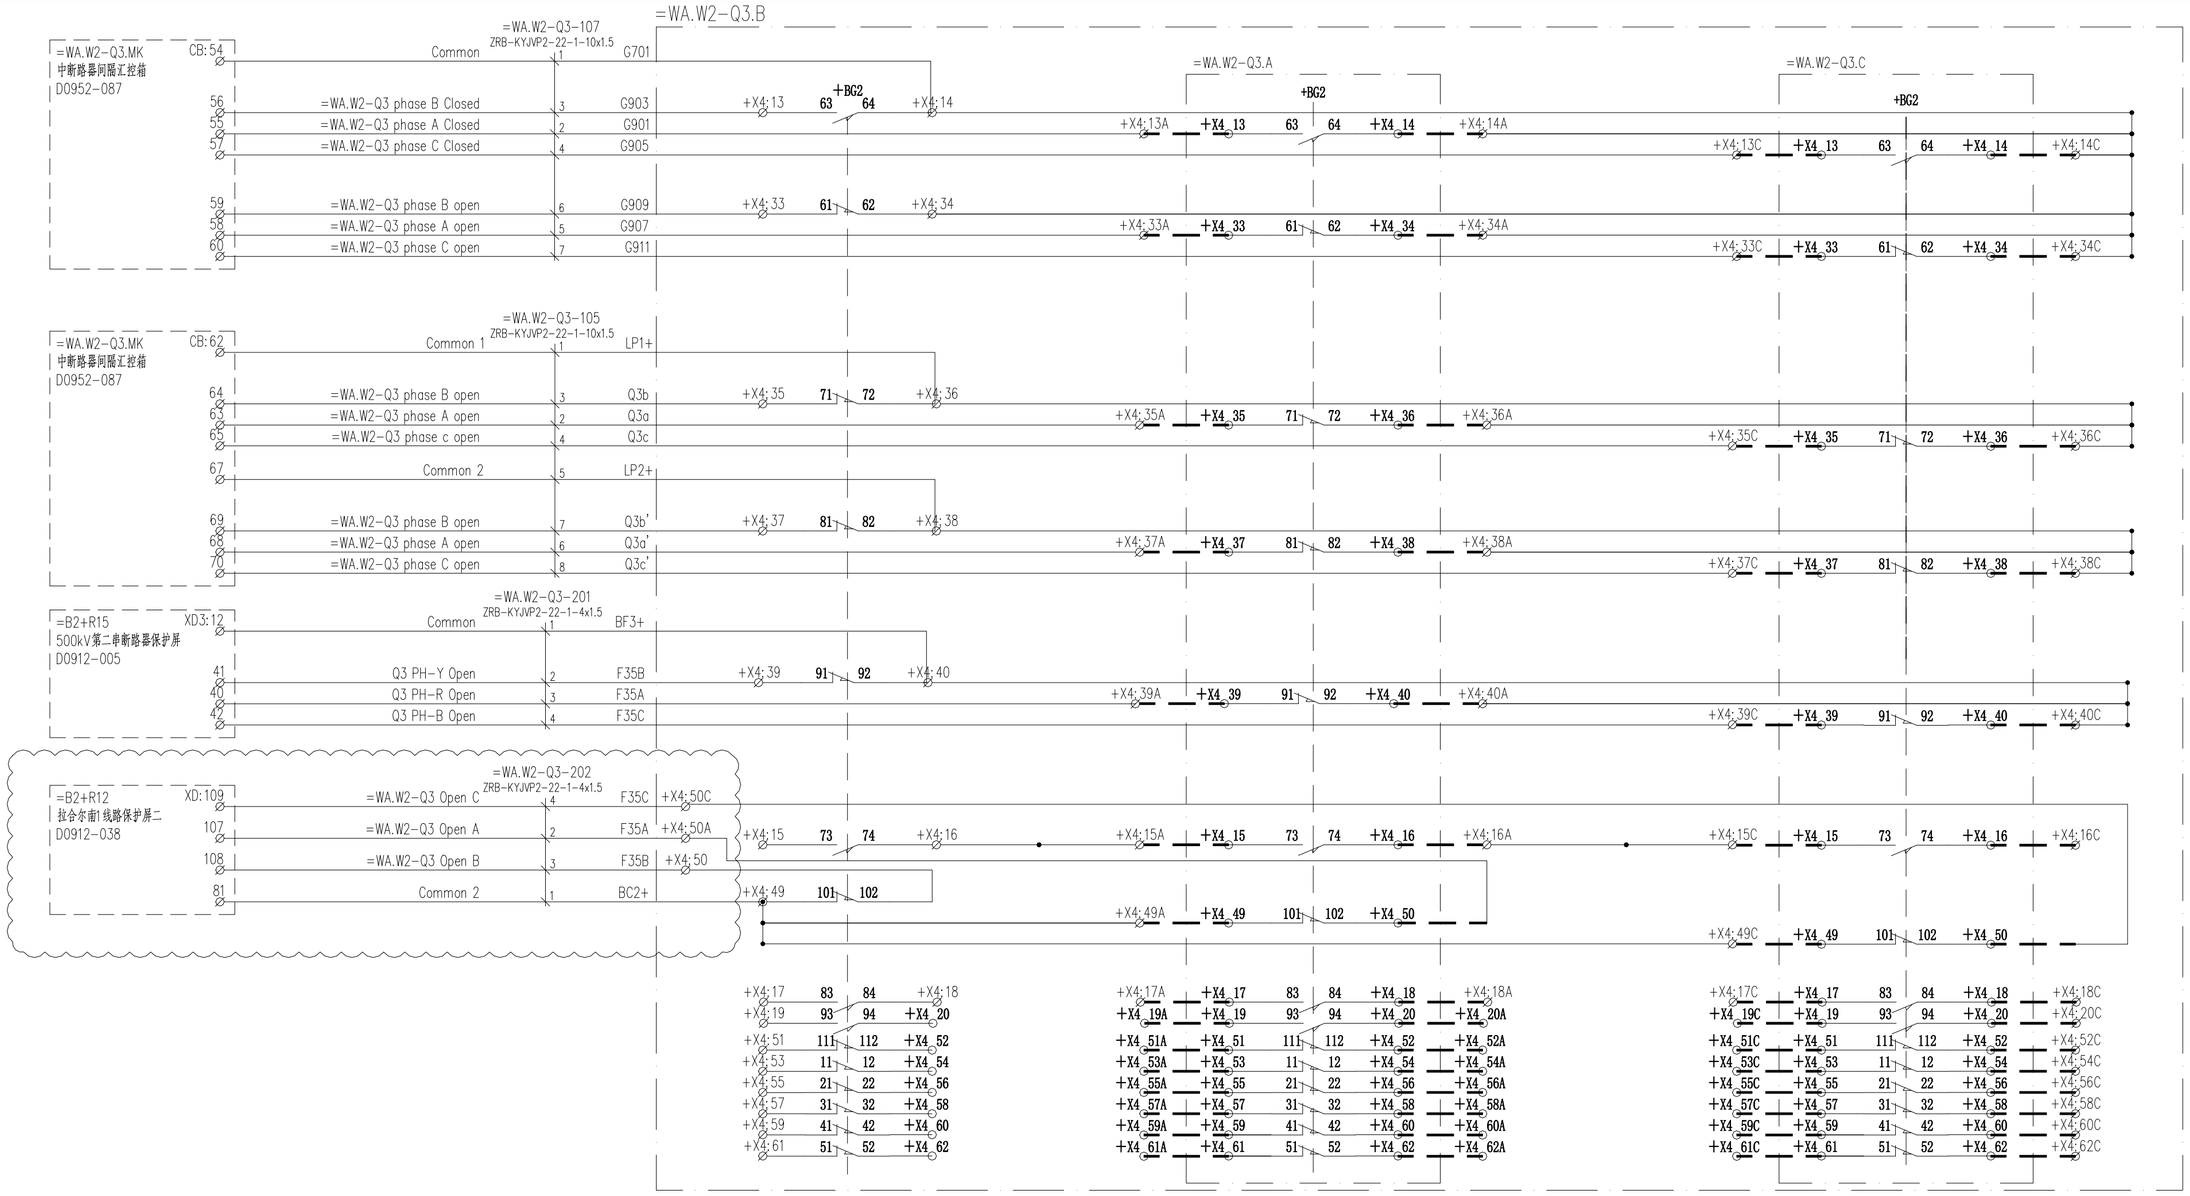


巴基斯坦默蒂亚里—拉合尔±660kV直流输电工程

±660kV HVDC Project from Matiari to Lahore in Pakistan

NATIONAL TRANSMISSION & DESPATCH COMPANY (NTDC) LIMITED PAKISTAN

CONTRACTOR 国家电网 STATE GRID 中国电力技术装备有限公司 CHINA ELECTRIC POWER EQUIPMENT AND TECHNOLOGY CO.,LTD.

SUBCONTRACTOR East China Electric Power Design Institute Co.,Ltd.

拉合尔±660kV换流站

±660kV Lahore Converter Station

设计阶段 PHASE: 施工图 Detail Design

MLHVDC-ENG-ECI-DD-PC-0952-063A

| | 姓名 Name | 日期 Date |
|---|---|---|
| 设计 Designed | 吴施正 | 2020.1.10 |
| 校核 Checked | 徐勇 | 2020.1.10 |
| 审核 Reviewed | | |
| 批准 Approved | 王建华 | 2020.1.10 |
| 比例 Scale | | 图号 DWG NO. |

断路器WA.W2-Q3辅助接点回路图二

Auxiliary Contact Circuit 2 of =WA.W2-Q3

30-B003701S-D0952-063

版本 REV. A

420X594