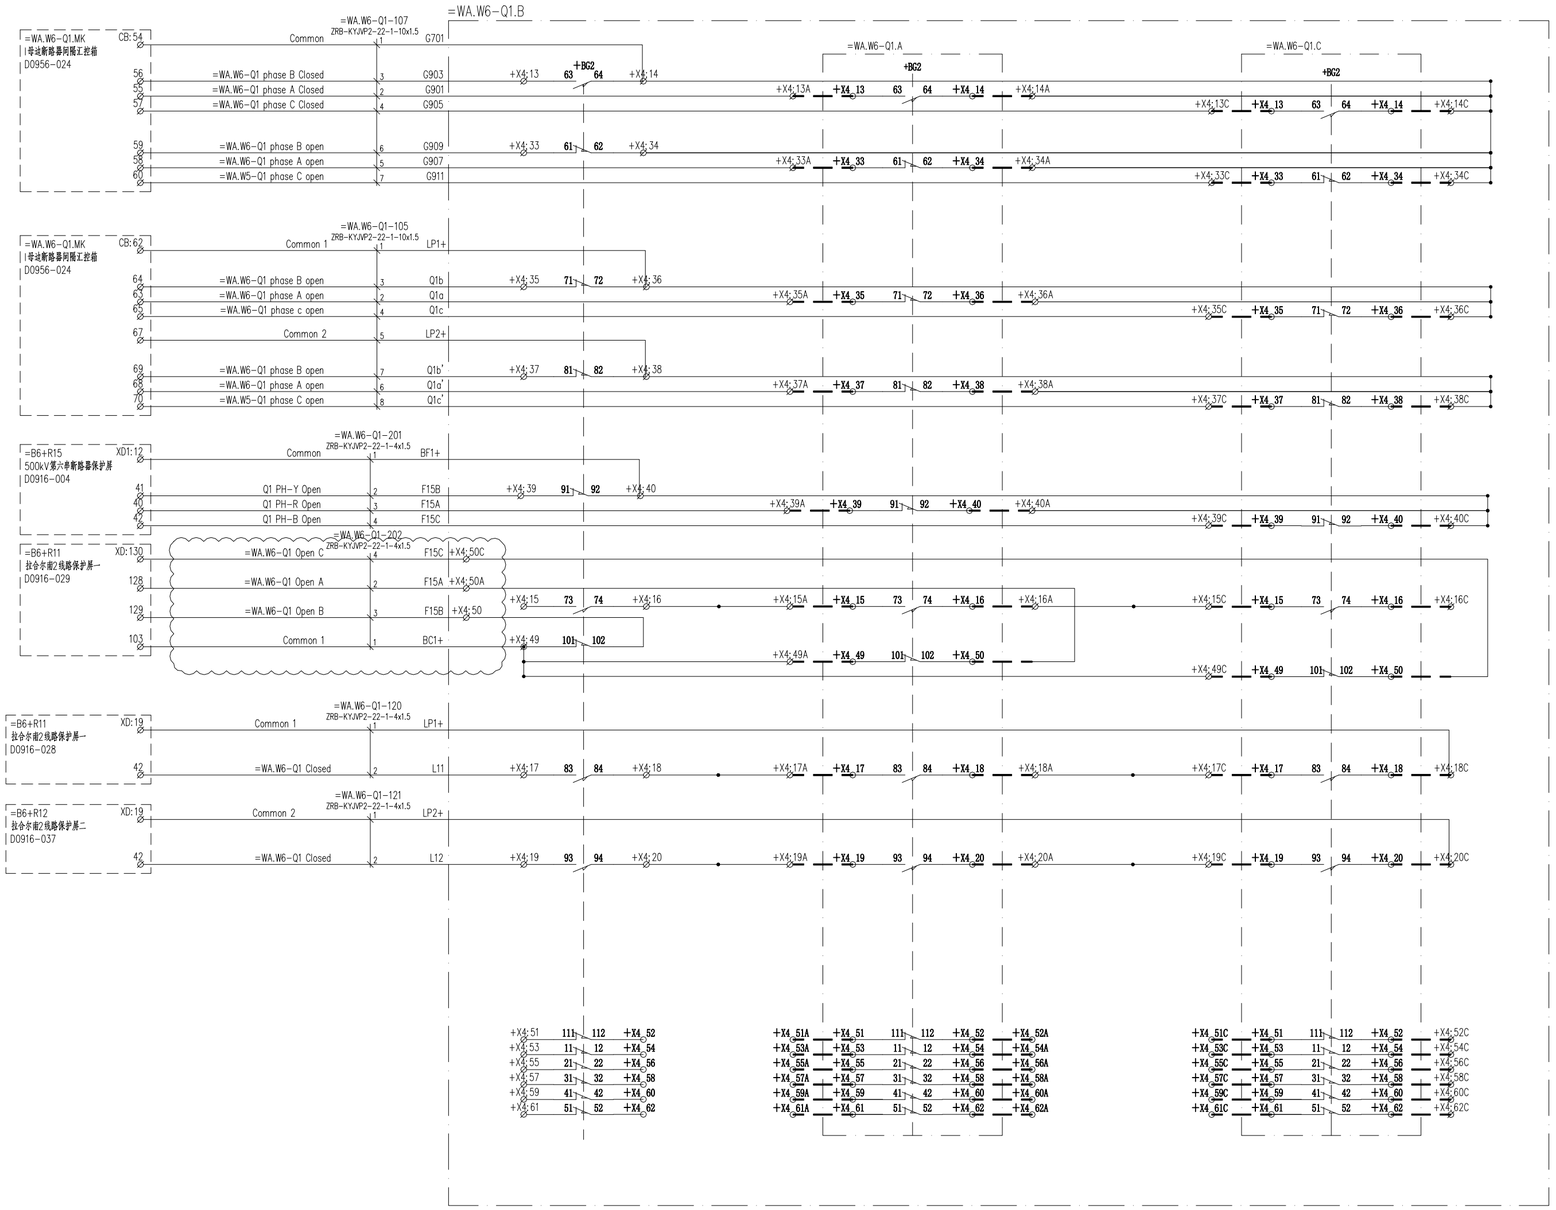

巴基斯坦默蒂亚里—拉合尔±660kV直流输电工程

±660kV HVDC Project from Matiari to Lahore in Pakistan

NATIONAL TRANSMISSION & DESPATCH COMPANY (NTDC) LIMITED PAKISTAN

CONTRACTOR 国家电网 STATE GRID 中国电力技术装备有限公司 CHINA ELECTRIC POWER EQUIPMENT AND TECHNOLOGY CO.,LTD.

SUBCONTRACTOR East China Electric Power Design Institute Co.,Ltd.

拉合尔±660kV换流站

±660kV Lahore Converter Station

设计阶段 PHASE: 施工图 Detail Design

MLHVDC-ENG-ECI-DD-PC-0956-007A

	姓名 Name	日期 Date
设计 Designed	吴敏江	2021.1.18
校核 Checked	徐磊	2021.1.18
审核 Reviewed		
批准 Approved	王建勇	2021.1.18
比例 Scale		图号 DWG NO.

断路器WA.W6-Q1辅助接点回路图二

Auxiliary Contact Circuit 2 of =WA.W6-Q1

30-B003701S-D0956-007

版本 REV. A

594X841