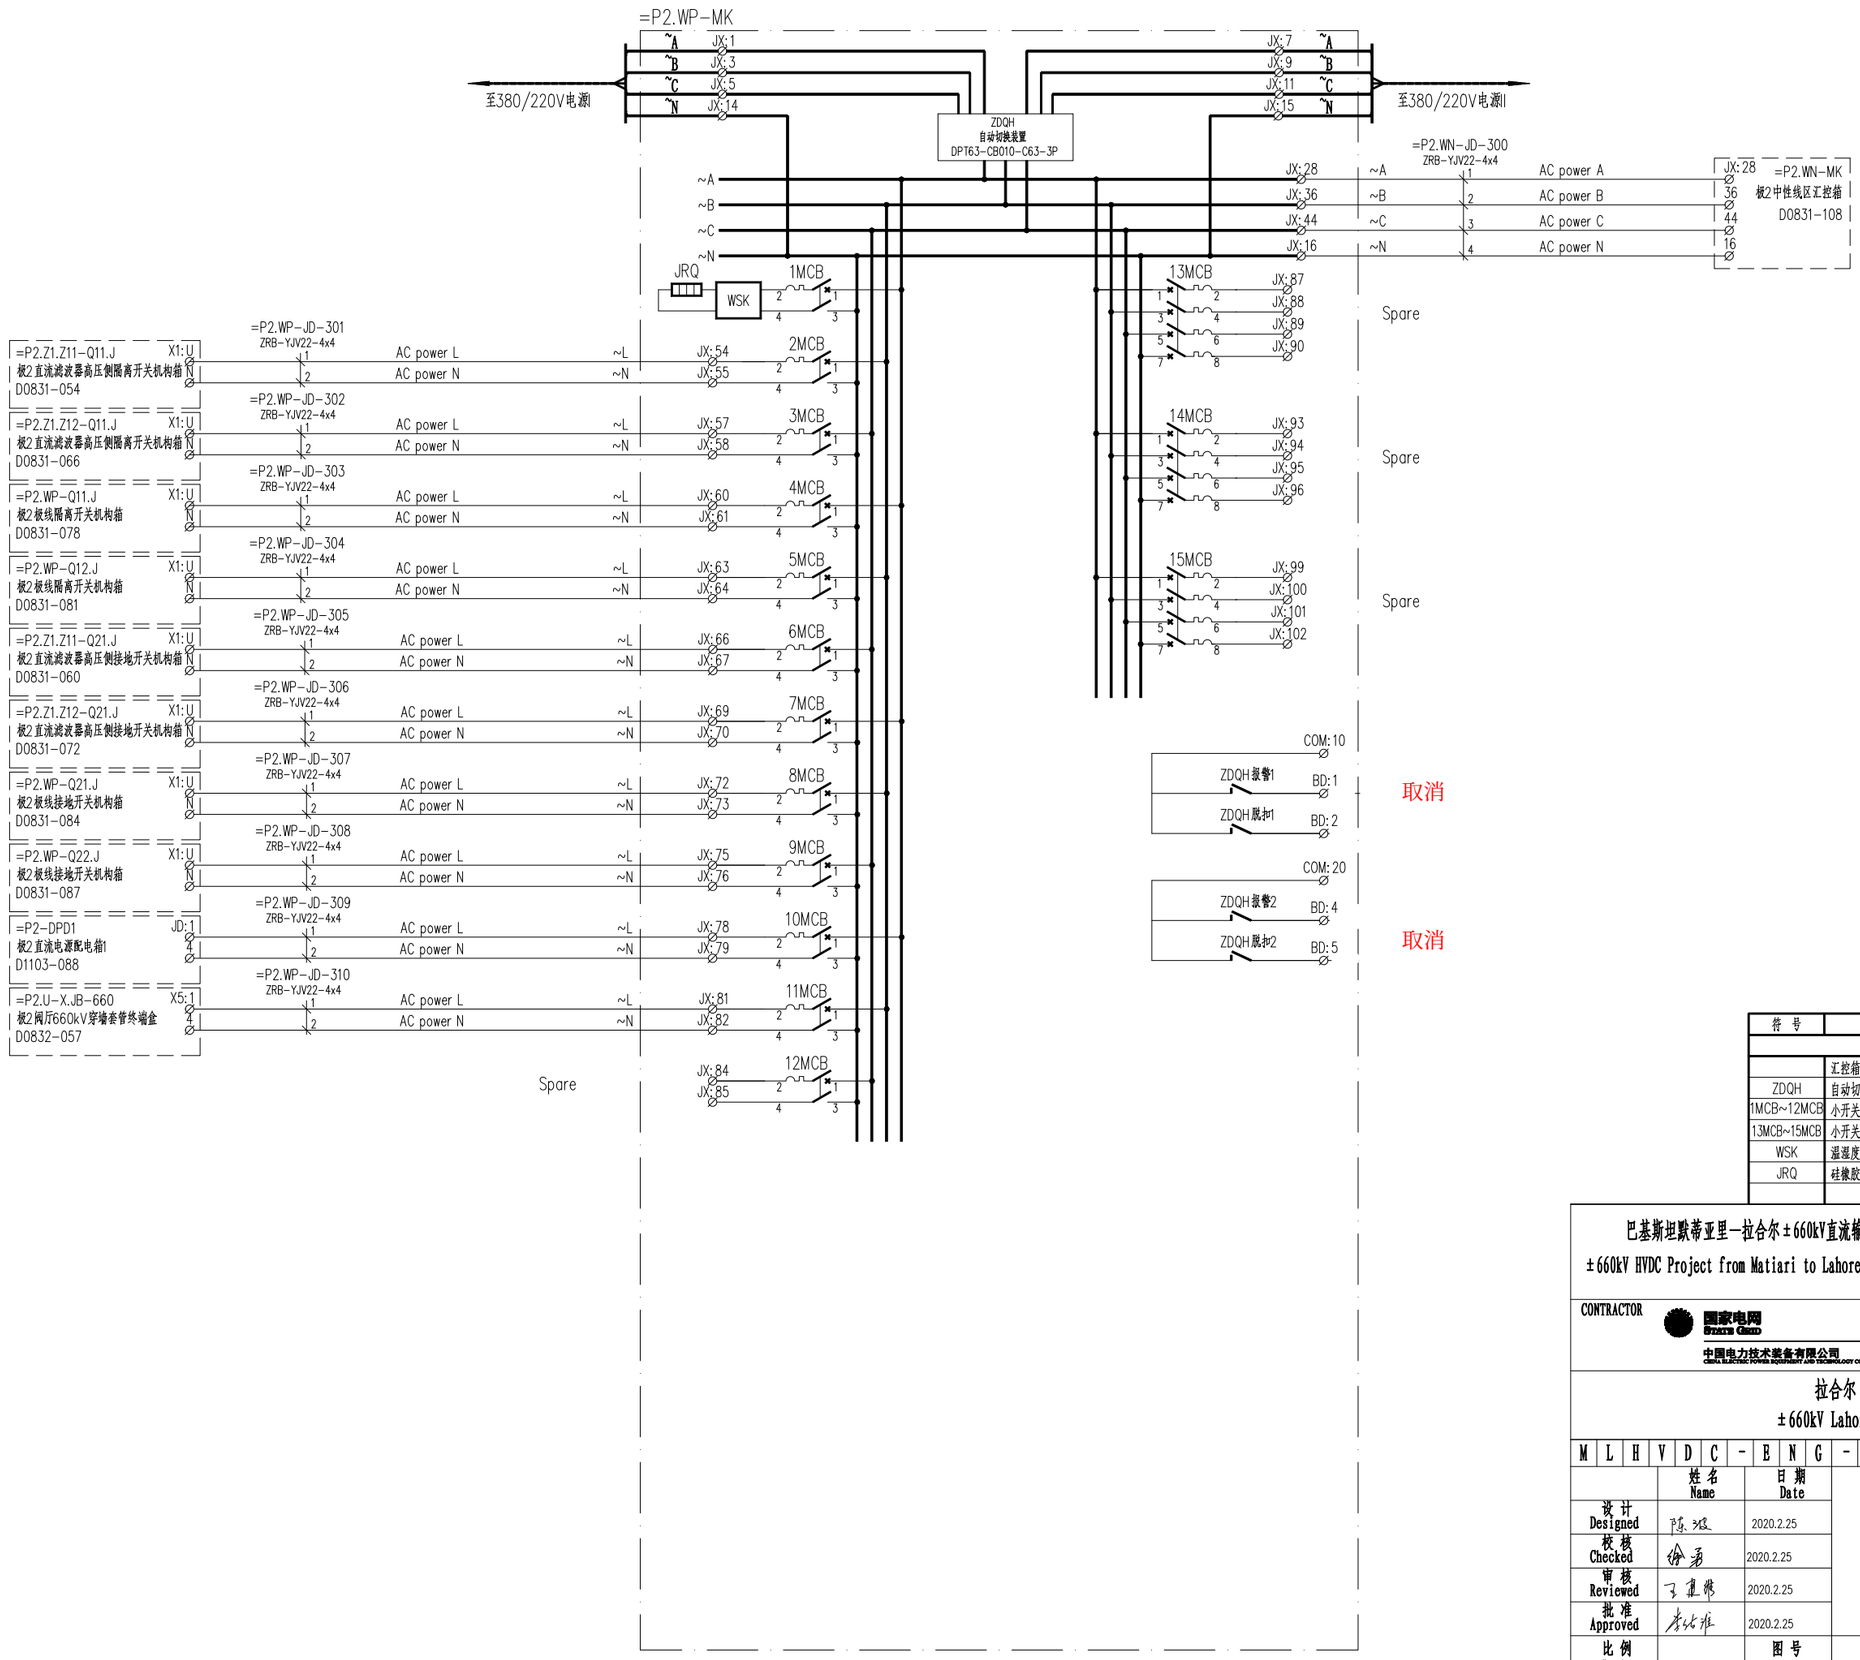

端子箱内布置图

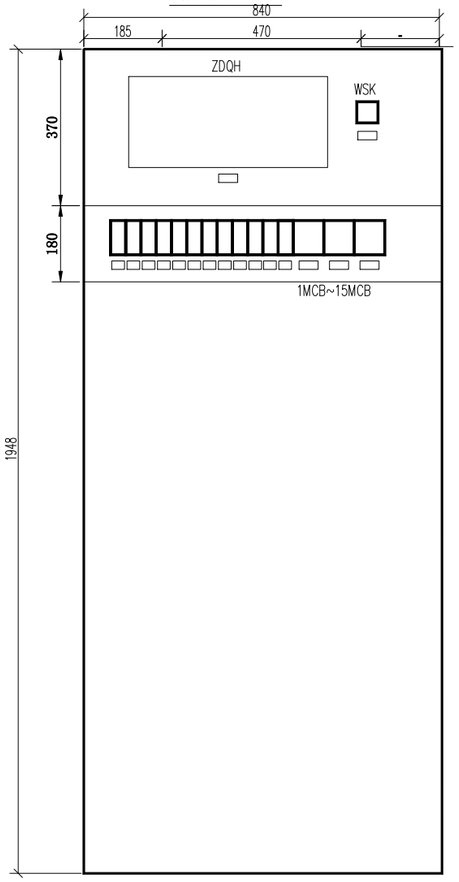

设 备 表

符 号	名 称	型 式	技术特性	数量	备 注
=P2.WP-MK 极2极线区汇控箱					
	汇控箱	ZXW-2/4(1948(H)X670(D)X840(B))		1	
ZDQH	自动切换装置	DPT63-CB010-C63-3P		1	ABB
1MCB~12MCB	小开关	iC65N-C16/2P		12	施耐德
13MCB~15MCB	小开关	iC65N-C25/4P		3	施耐德
WSK	湿湿度控制器	WNK3D	AC220V	1	陕西印创
JRQ	硅橡胶加热器	NJ50	AC220V,50W	1	陕西印创

巴基斯坦默蒂亚里—拉合尔±660kV直流输电工程

±660kV HVDC Project from Matiari to Lahore in Pakistan

NATIONAL TRANSMISSION & DESPATCH COMPANY (NTDC) LIMITED PAKISTAN

CONTRACTOR 国家电网 STATE GRID 中国电力技术装备有限公司 CHINA ELECTRIC POWER EQUIPMENT AND TECHNOLOGY CO.,LTD.

SUBCONTRACTOR East China Electric Power Design Institute Co.,Ltd.

拉合尔±660kV换流站

±660kV Lahore Converter Station

设计阶段 PHASE: 施工图 Detail Design

M L H V D C - E N G - E C I - D D - P C - 0 8 3 1 - 1 0 7 A

	姓名 Name	日期 Date
设计 Designed	陈 [illegible]	2020.2.25
校核 Checked	徐 [illegible]	2020.2.25
审核 Reviewed	王 [illegible]	2020.2.25
批准 Approved	李 [illegible]	2020.2.25
比例 Scale		图号 DWG NO.

极2直流极线区汇控箱交流电源配电回路图

AC Power circuit in P2.WP-MK

30-B003701S-D0831-107

版本 REV. A

420X594

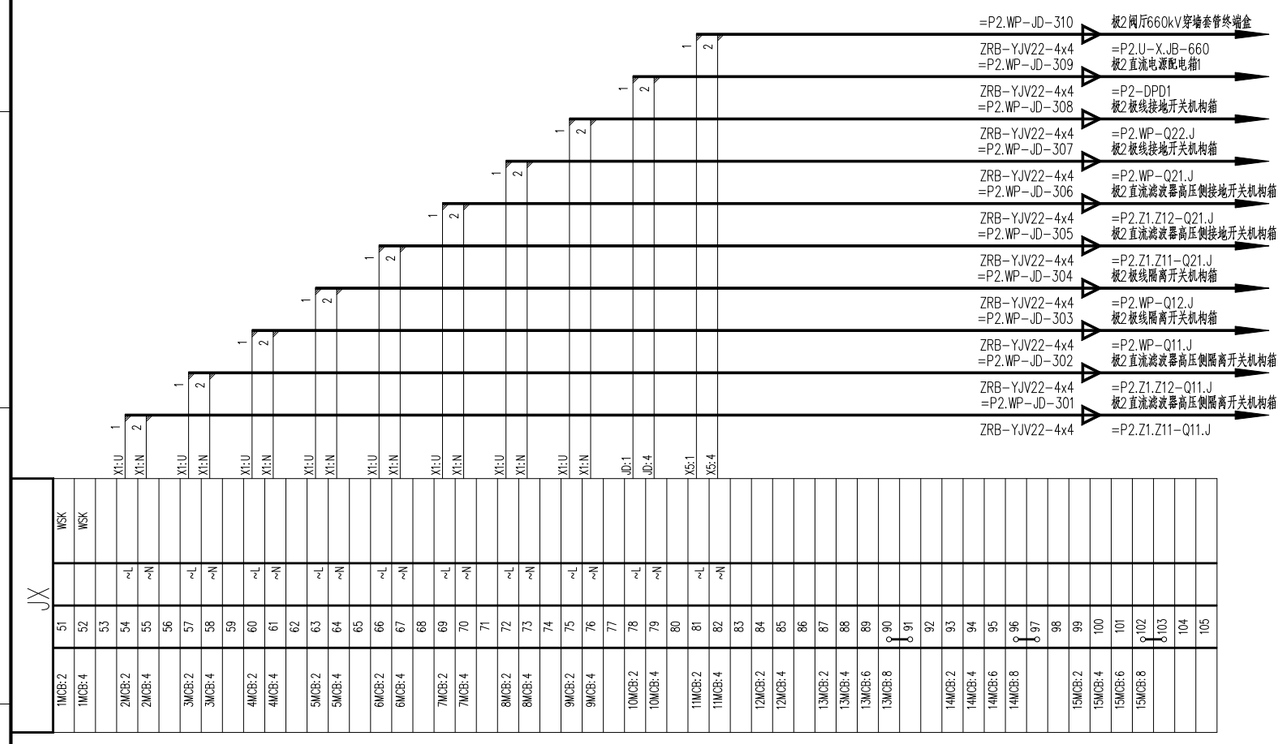

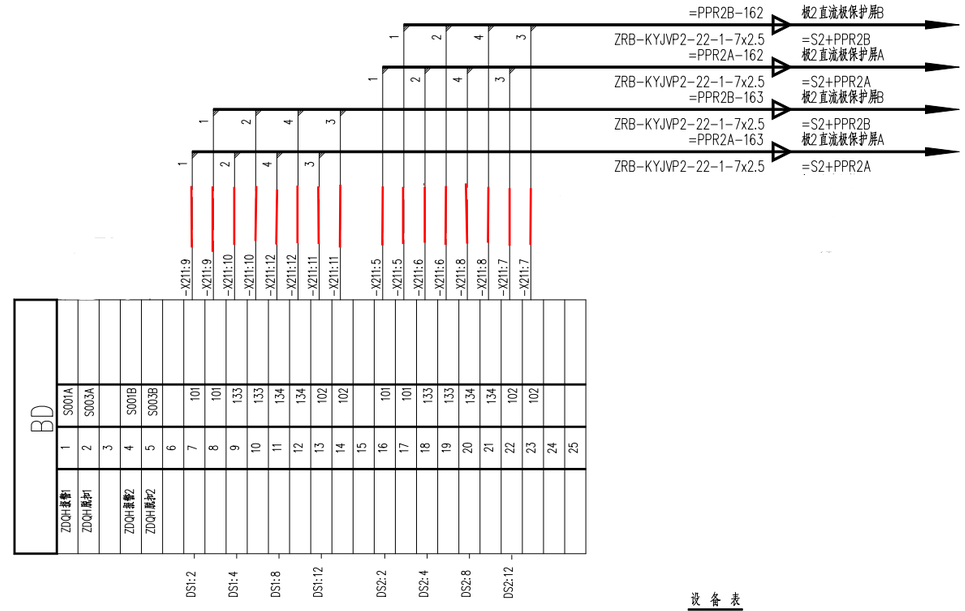

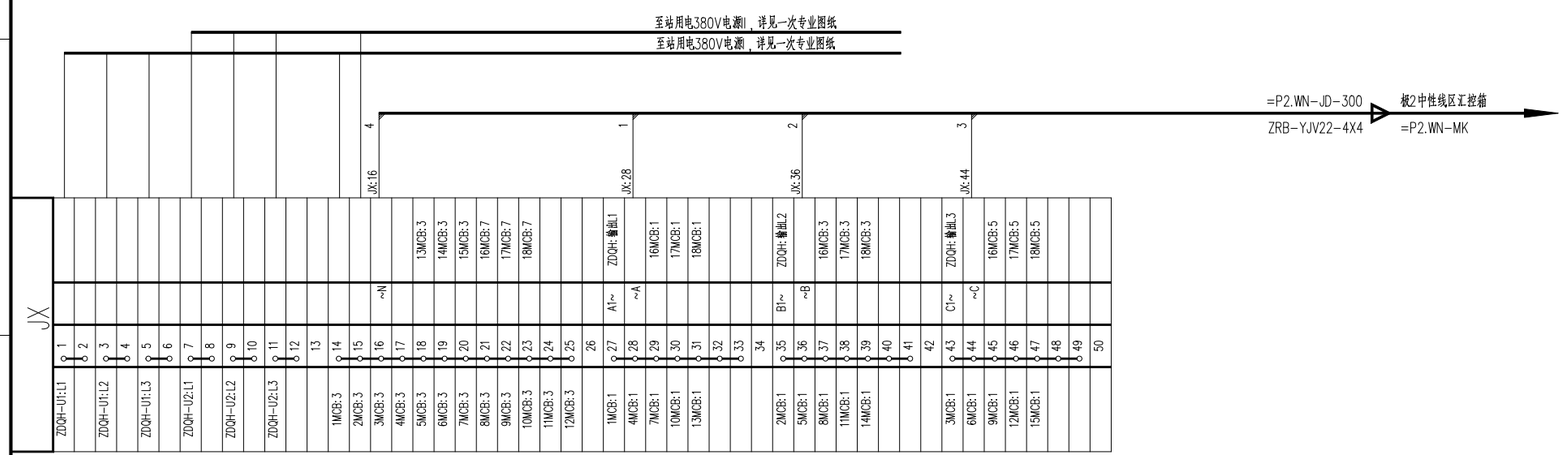

设 备 表

符 号	名 称	型 式	技术特性	数量	备 注
=P2.WP-MK 汇控箱					
	汇控箱	ZXW-2/4(1948(H)X670(D)X840(B))		1	
ZDQH	自动切换装置	DPT63-CB010-C63-3P		1	ABB
1MCB~12MCB	小开关	iC65N-C16/2P		12	施耐德
13MCB~15MCB	小开关	iC65N-C25/4P		3	施耐德
WSK	温湿度控制器	WNK3D	AC220V	1	陕西和创
JRQ	硅橡胶加热器	NJ50	AC220V,50W	1	陕西和创
COM:1~20;DS1/DS2:1~30 DS3/DS4/ES1/ES2:1~30 ES3/ES4:1~30 BD:1~10	接线端子	UK 5N		270	
JX:1~50	大电流端子	UK 35		50	
JX:51~105	大电流端子	UK 10N		55	
	终端端子			14	

巴基斯坦默蒂亚里—拉合尔±660kV直流输电工程

±660kV HVDC Project from Matiari to Lahore in Pakistan

NATIONAL TRANSMISSION & DESPATCH COMPANY (NTDC) LIMITED PAKISTAN

CONTRACTOR 国家电网 STATE GRID 中国电力技术装备有限公司 CHINA ELECTRIC POWER EQUIPMENT AND TECHNOLOGY CO.,LTD.

SUBCONTRACTOR East China Electric Power Design Institute Co.,Ltd.

拉合尔±660kV换流站

±660kV Lahore Converter Station

设计阶段 PHASE: 施工图 Detail Design

M L H V D C - E N G - E C I - D D - P C - 0 8 3 1 - 1 3 8 A

	姓名 Name	日期 Date
设计 Designed	陈 [illegible]	2020.2.25
校核 Checked	徐 [illegible]	2020.2.25
审核 Reviewed	王 [illegible]	2020.2.25
批准 Approved	李 [illegible]	2020.2.25

极2直流极线区汇控箱端子排图五
Terminal diagram 5 of P2.WP-MK

比例 Scale:

图号 DWG NO.: 30-B003701S-D0831-138

版本 REV.: A

420X594