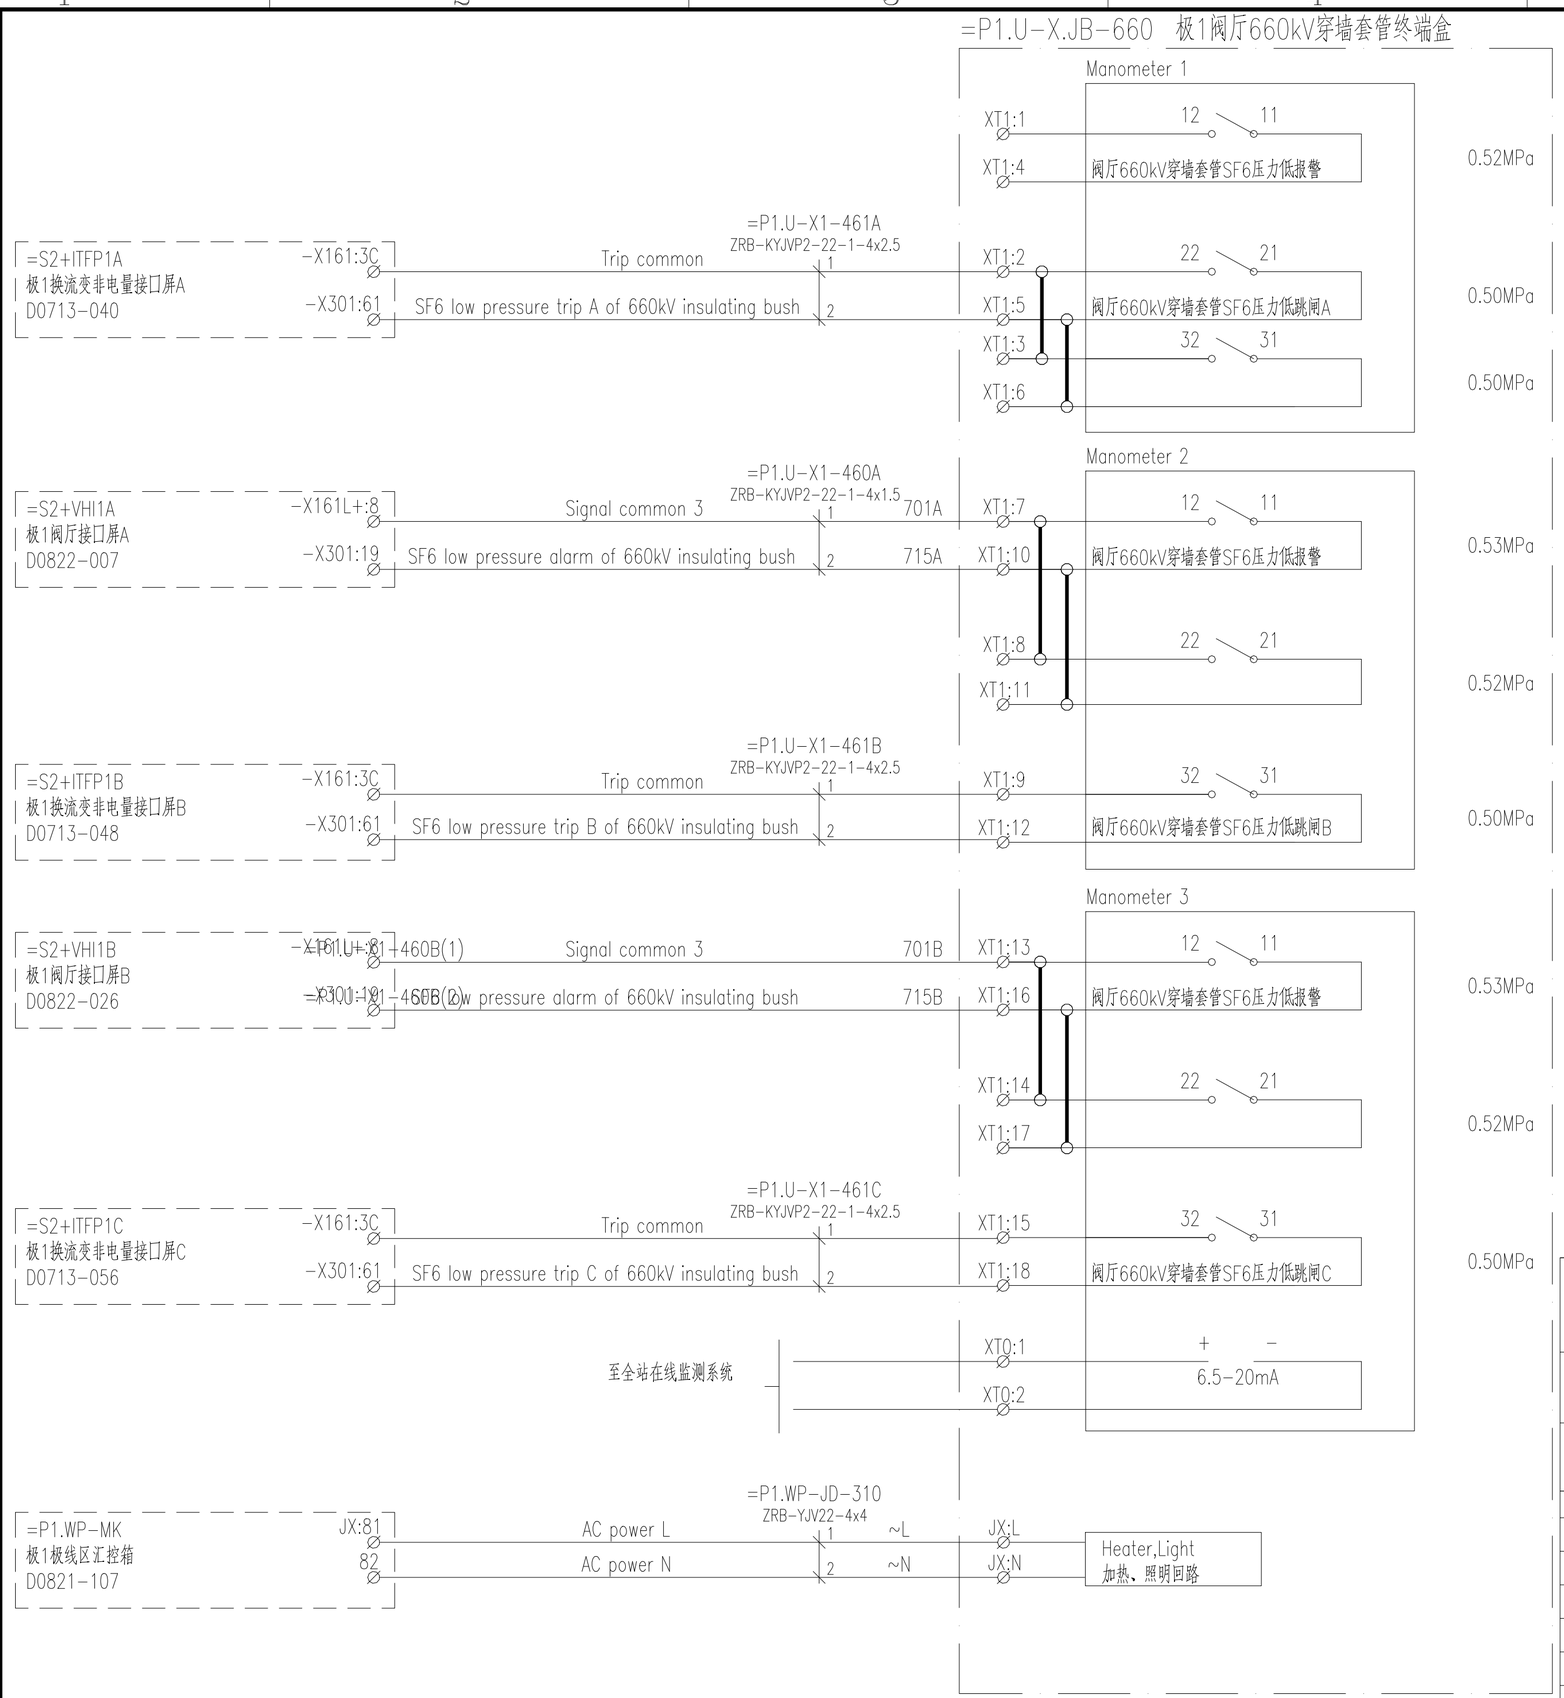


根据现场反馈，修改了穿墙套管终端盒内部接线。

ALARM level 1: 0.530±0.008 MPa at 20℃
ALARM level 2: 0.520±0.008 MPa at 20℃
Trip level: 0.500±0.008 MPa at 20℃

巴基斯坦默蒂亚里—拉合尔±660kV直流输电工程
±660kV HVDC Project from Matiari to Lahore in Pakistan

NATIONAL TRANSMISSION & DESPATCH COMPANY (NTDC) LIMITED PAKISTAN

CONTRACTOR 国家电网 STATE GRID 中国电力技术装备有限公司 CHINA ELECTRIC POWER EQUIPMENT AND TECHNOLOGY CO.,LTD.

SUBCONTRACTOR East China Electric Power Design Institute Co.,Ltd.

拉合尔±660kV换流站
±660kV Lahore Converter Station

设计阶段 PHASE: 施工图 Detail Design

M L H V D C - E N G - E C I - D D - P C - 0 8 2 2 - 0 5 7 A

| | 姓名 Name | 日期 Date |
|---|---|---|
| 设计 Designed | 陈 | 2020.2.25 |
| 校核 Checked | 徐 | 2020.2.25 |
| 审核 Reviewed | 王 | 2020.2.25 |
| 批准 Approved | 李 | 2020.2.25 |
| 比例 Scale | | 图号 DWG NO. |

极1阀厅660kV穿墙套管接线图
Connection diagram of 660kV insulating bush in P1 valve hall

30-B003701S-D0822-057

版本 REV. A

297X420