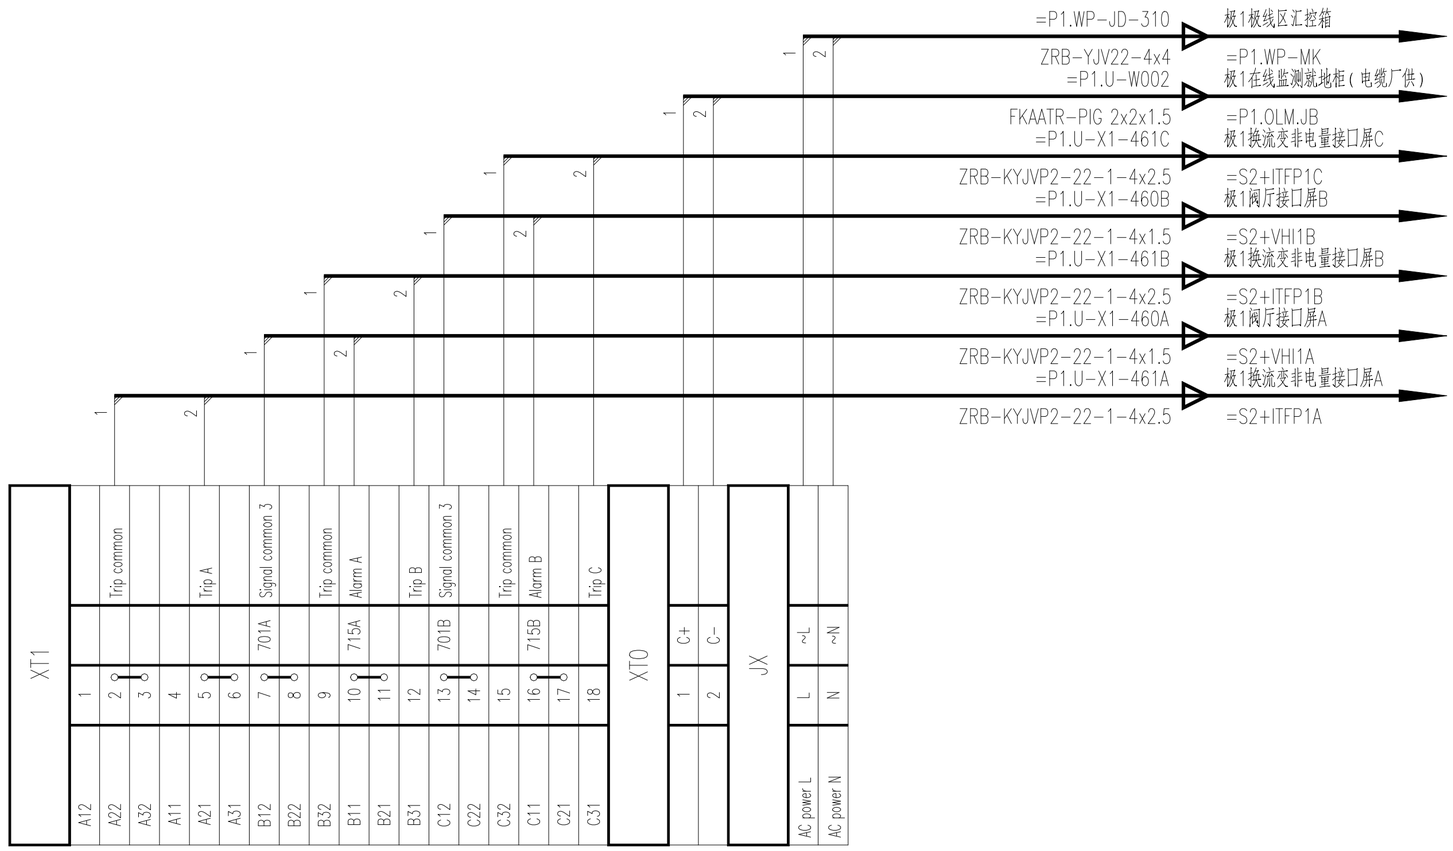

根据现场反馈，修改了穿墙套管终端盒内部接线端子排。

巴基斯坦默蒂亚里—拉合尔±660kV直流输电工程

±660kV HVDC Project from Matiari to Lahore in Pakistan

NATIONAL TRANSMISSION & DESPATCH COMPANY (NTDC) LIMITED PAKISTAN

CONTRACTOR 国家电网 STATE GRID 中国电力技术装备有限公司 CHINA ELECTRIC POWER EQUIPMENT AND TECHNOLOGY CO.,LTD.

SUBCONTRACTOR East China Electric Power Design Institute Co.,Ltd.

拉合尔±660kV换流站

±660kV Lahore Converter Station

设计阶段 PHASE: 施工图 Detail Design

M L H V D C - E N G - E C I - D D - P C - 0 8 2 2 - 0 6 7 A

	姓名 Name	日期 Date
设计 Designed	陈波	2020.2.25
校核 Checked	徐勇	2020.2.25
审核 Reviewed	王建伟	2020.2.25
批准 Approved	李佑雅	2020.2.25

极1阀厅660kV穿墙套管端子排图

Terminal diagram of 660kV insulating bush in P1 valve hall

比例 Scale

图号 DWG NO. 30-B003701S-D0822-067

版本 REV. A

297X420