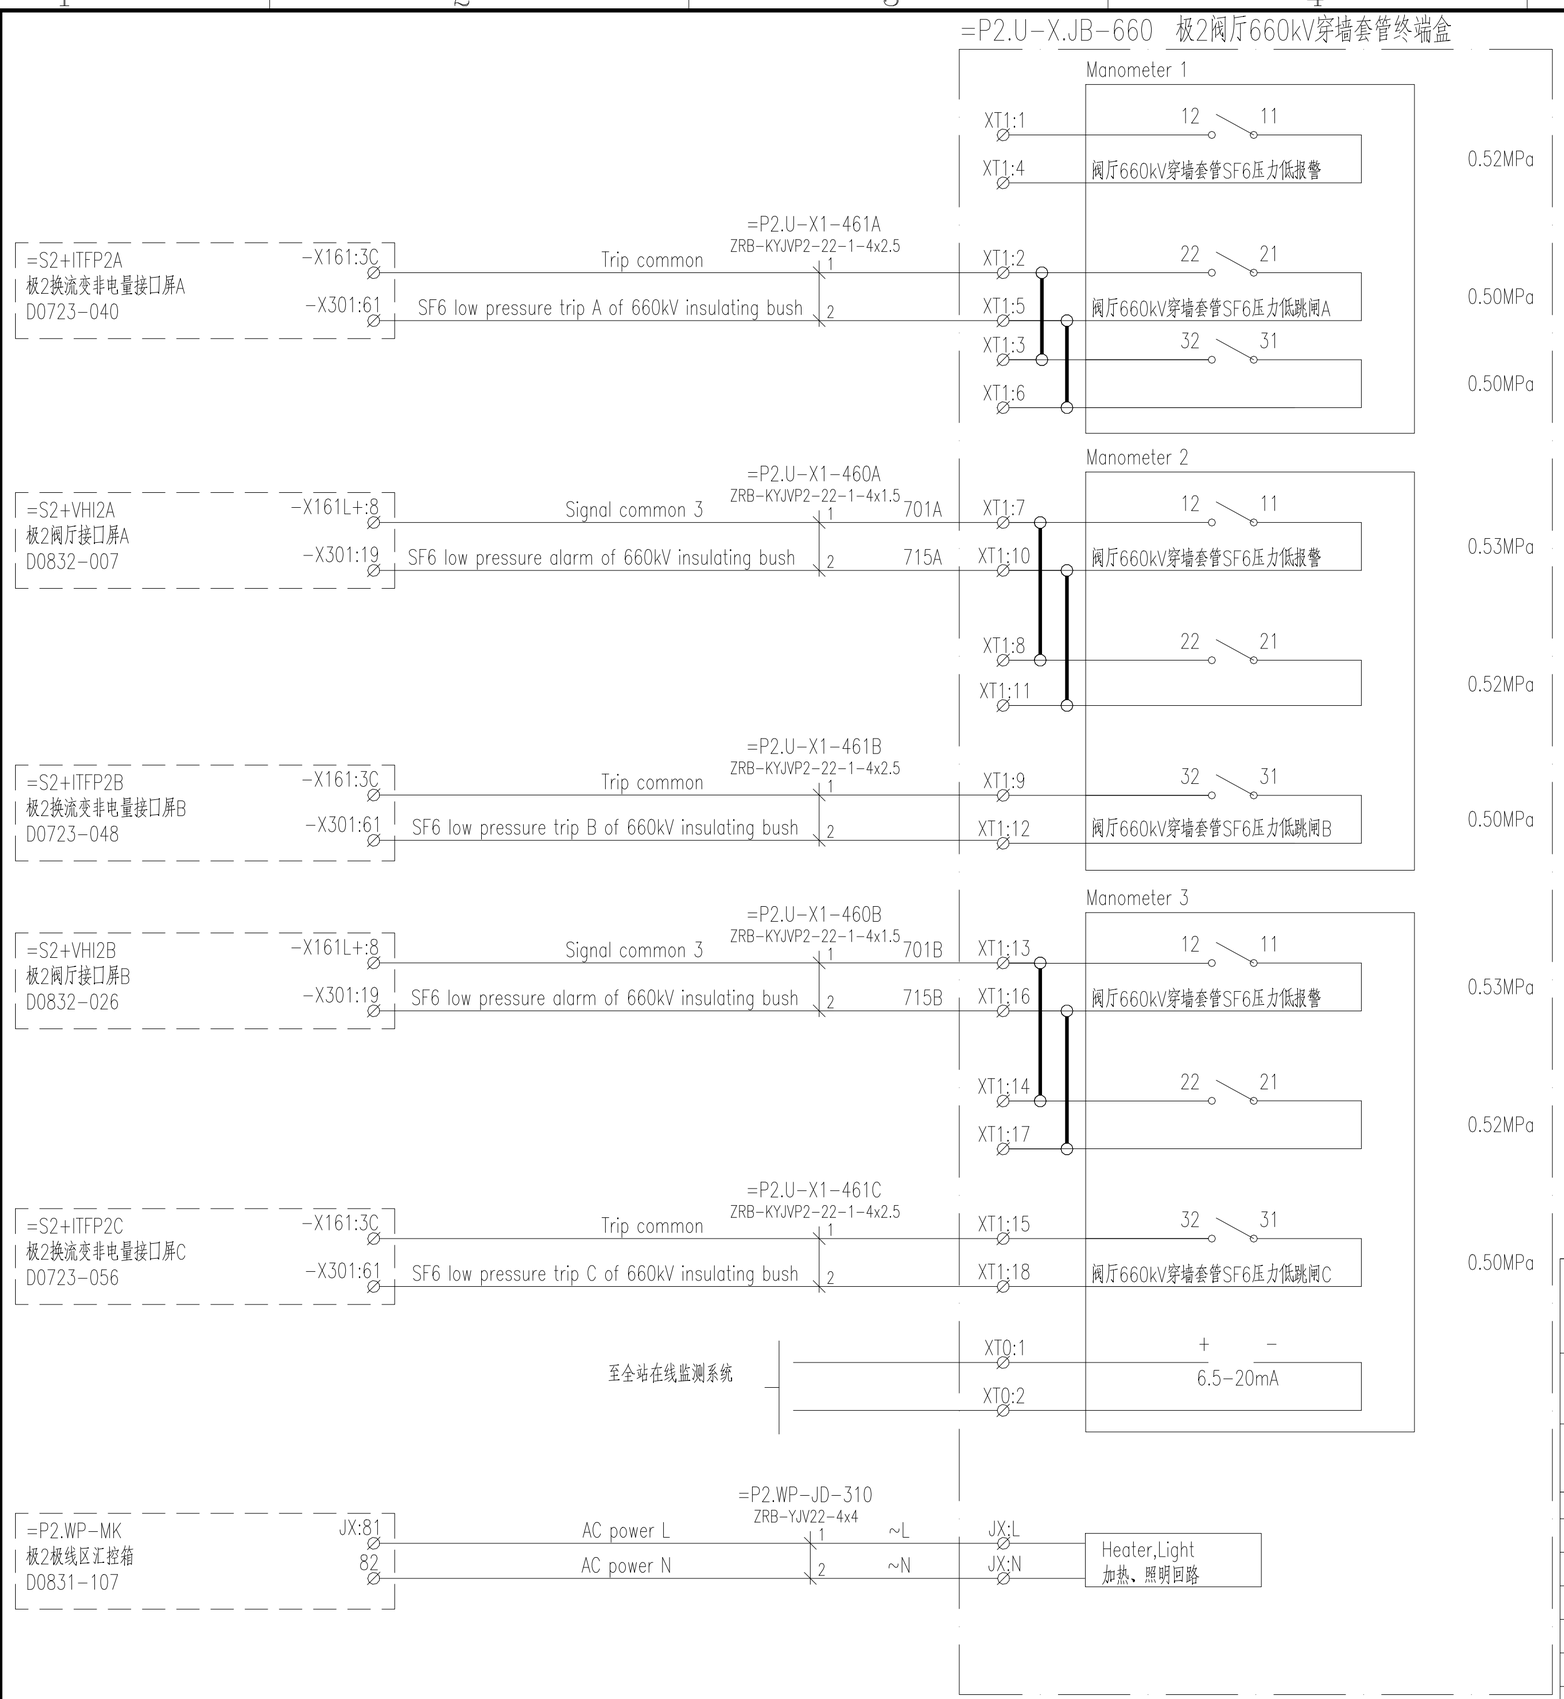

根据现场反馈，修改了穿墙套管终端盒内部接线。

巴基斯坦默蒂亚里—拉合尔±660kV直流输电工程

±660kV HVDC Project from Matiari to Lahore in Pakistan

NATIONAL TRANSMISSION & DESPATCH COMPANY (NTDC) LIMITED PAKISTAN

CONTRACTOR 国家电网 STATE GRID 中国电力技术装备有限公司 CHINA ELECTRIC POWER EQUIPMENT AND TECHNOLOGY CO.,LTD.

SUBCONTRACTOR East China Electric Power Design Institute Co.,Ltd.

拉合尔±660kV换流站

±660kV Lahore Converter Station

设计阶段 PHASE: 施工图 Detail Design

M L H V D C - E N G - E C I - D D - P C - 0 8 2 3 - 0 5 7 A

	姓名 Name	日期 Date
设计 Designed		2020.2.25
校核 Checked		2020.2.25
审核 Reviewed		2020.2.25
批准 Approved		2020.2.25
比例 Scale		图号 DWG NO.

极2阀厅660kV穿墙套管接线图

Connection diagram of 660kV insulating bush in P2 valve hall

30-B003701S-D0832-057

版本 REV. A

297X420