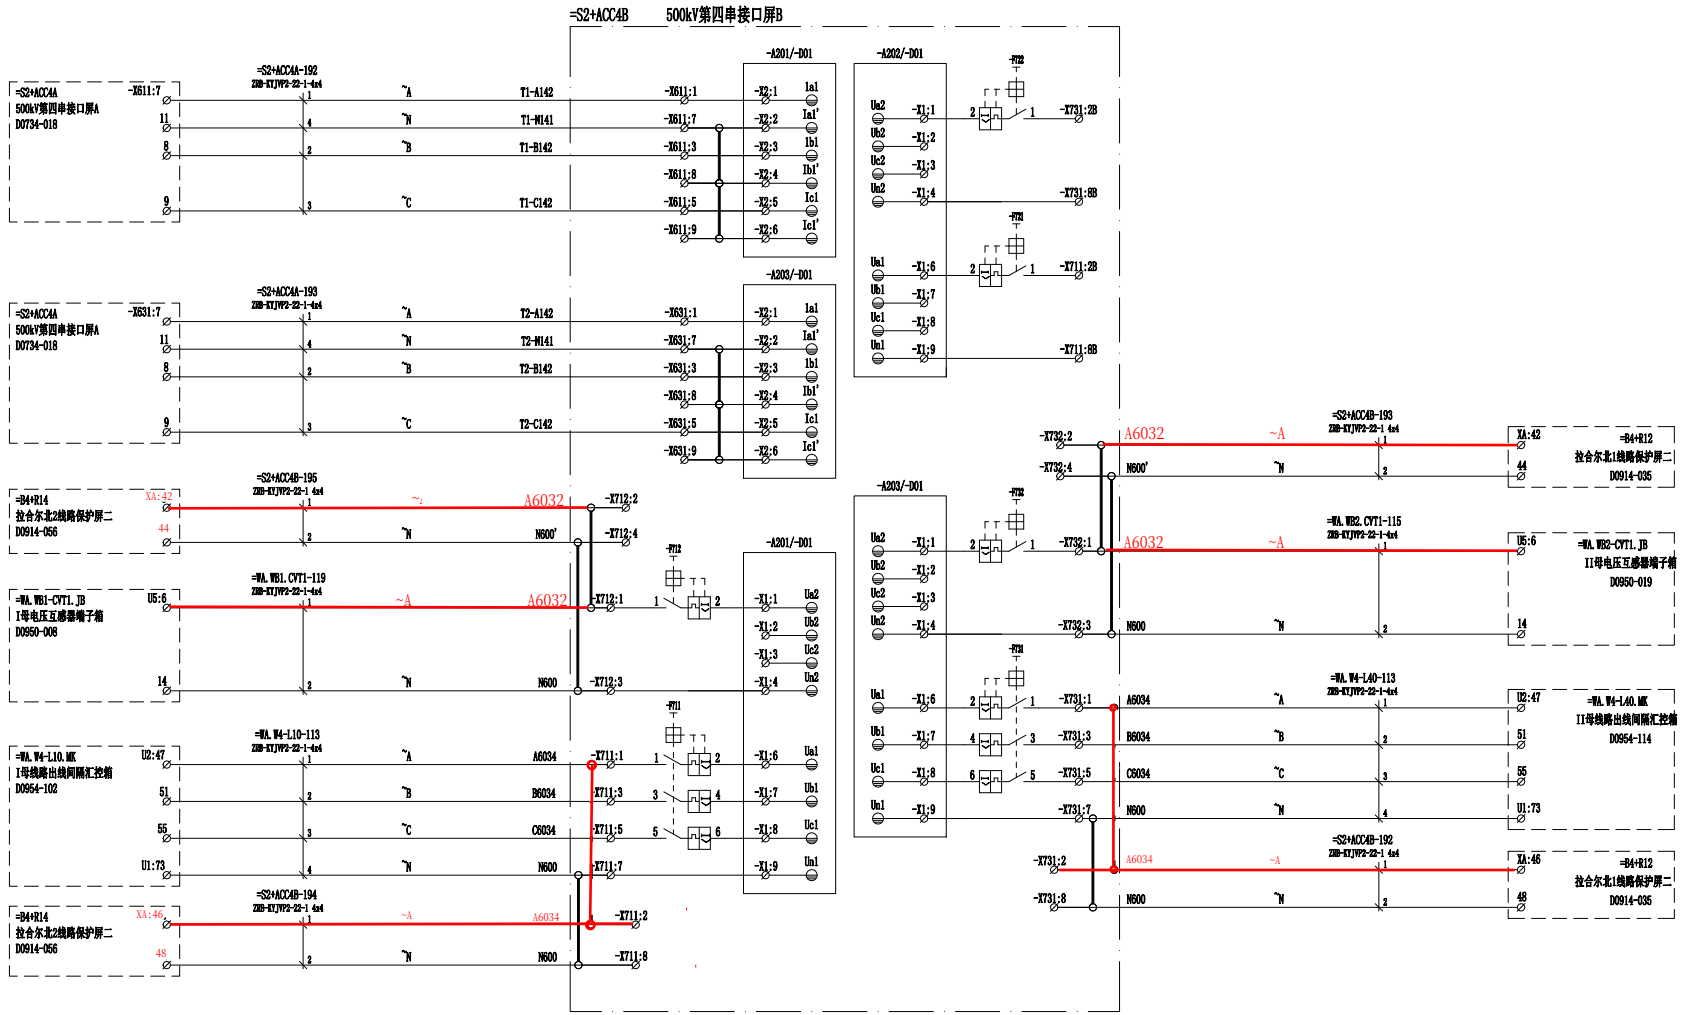

巴基斯坦默蒂亚里—拉合尔±660kV直流输电工程

±660kV HVDC Project from Matiari to Lahore in Pakistan

NATIONAL TRANSMISSION & DESPATCH COMPANY (NTDC) LIMITED PAKISTAN

CONTRACTOR 国家电网 State Grid 中国电力技术装备有限公司

SUBCONTRACTOR East China Electric Power Design Institute Co.,Ltd.

拉合尔±660kV换流站

±660kV Lahore Converter Station

设计阶段 PHASE: 施工图 Detail Design

MLHVDC-ENG-ECI-DD-PC-0734-039A

	姓名 Name	日期 Date
设计 Designed		2018.1.10
校核 Checked		2018.1.10
审核 Reviewed		
批准 Approved		2018.1.10
比例 Scale		图号 DWG NO.

500kV交流场第四串接口屏B电流电压测量回路图

Current Voltage measuring circuit (=S2+ACC4B)

30-B003701S-D0734-039

版本 REV. A

420X594