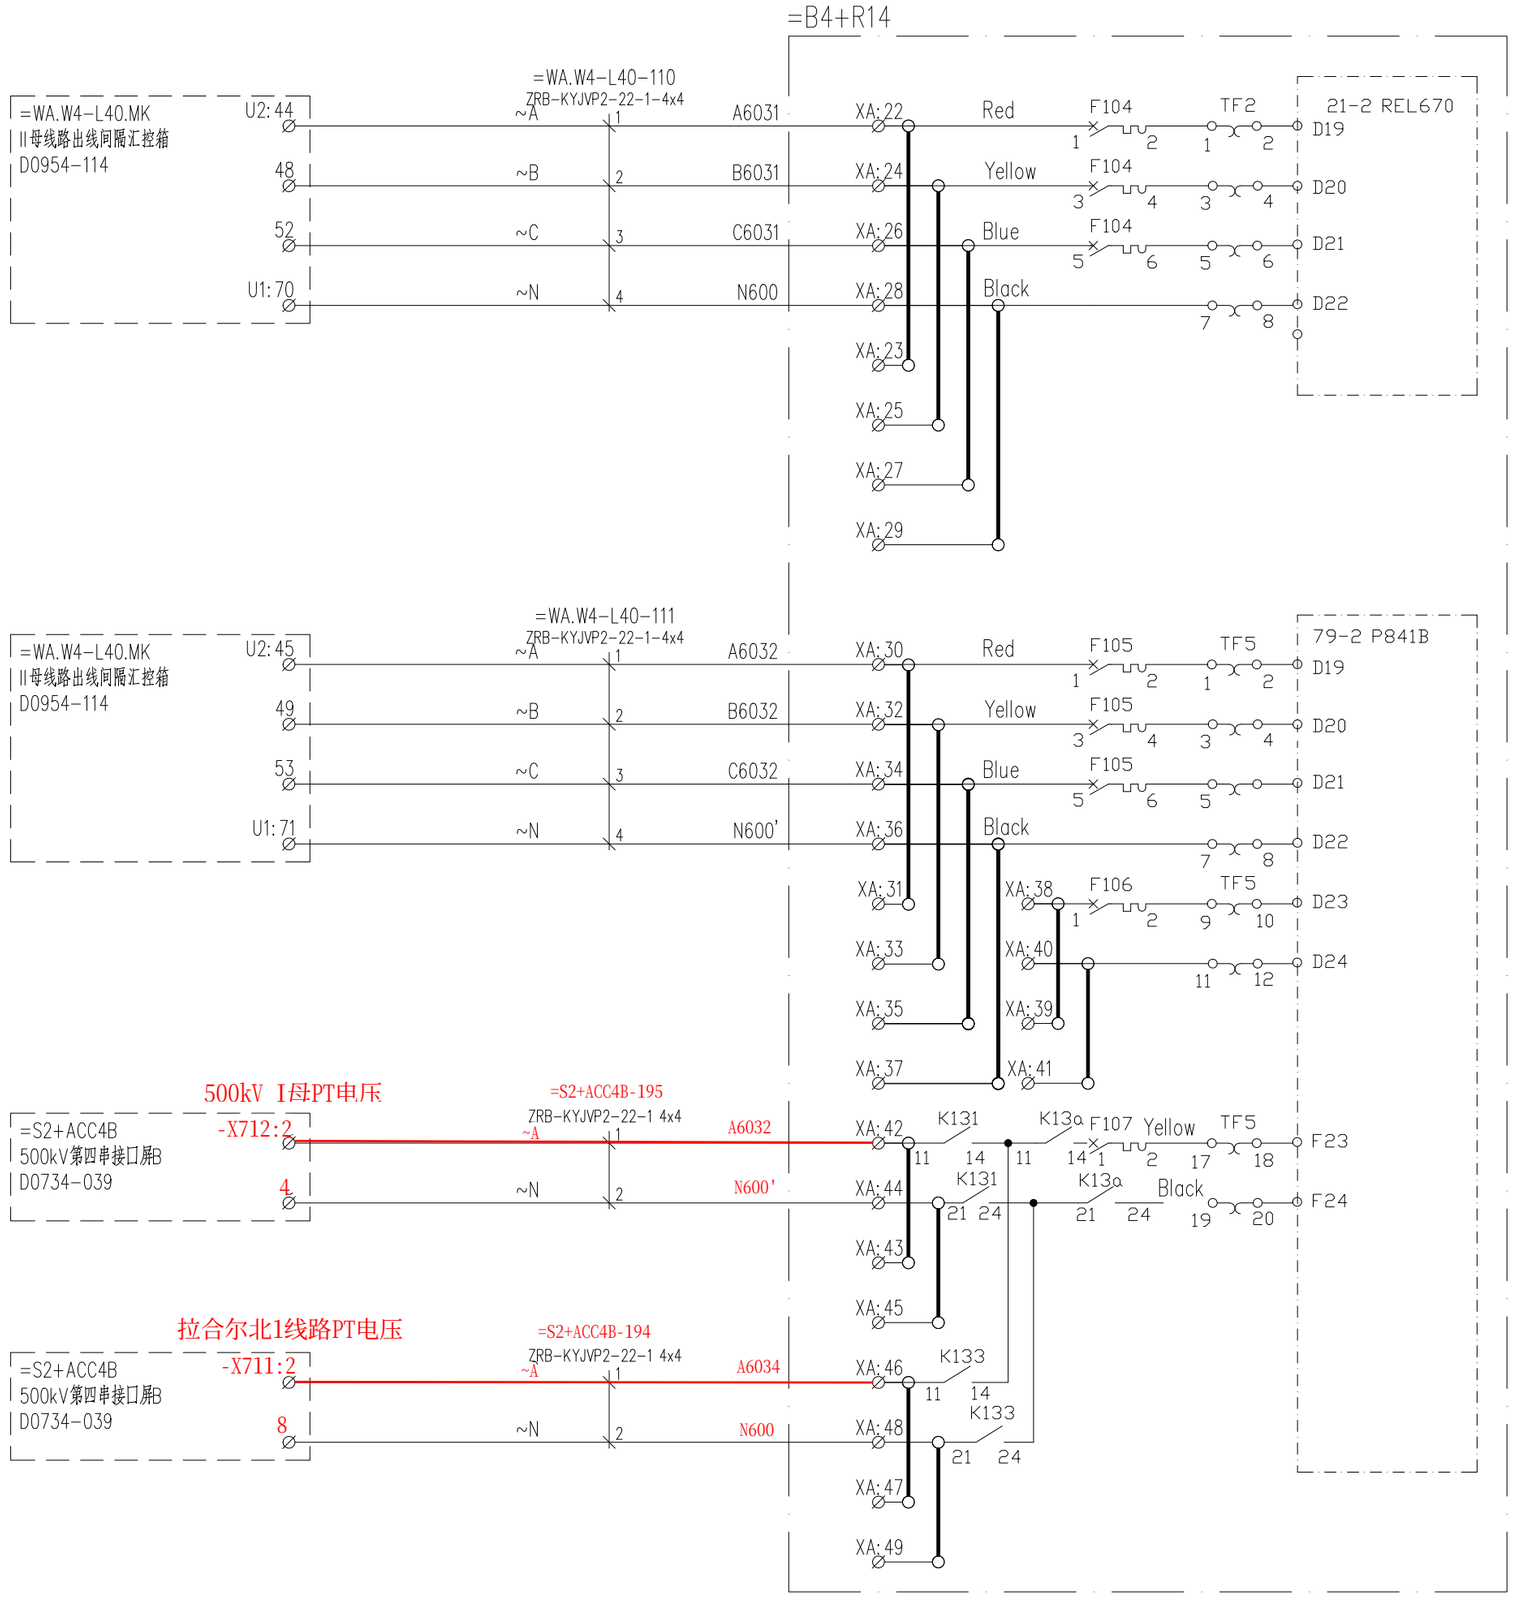

巴基斯坦默蒂亚里—拉合尔±660kV直流输电工程

±660kV HVDC Project from Matiari to Lahore in Pakistan

NATIONAL TRANSMISSION & DESPATCH COMPANY (NTDC) LIMITED PAKISTAN

CONTRACTOR 国家电网 STATE GRID 中国电力技术装备有限公司 CHINA ELECTRIC POWER EQUIPMENT AND TECHNOLOGY CO.,LTD.

SUBCONTRACTOR East China Electric Power Design Institute Co.,Ltd.

拉合尔±660kV换流站

±660kV Lahore Converter Station

设计阶段 PHASE: 施工图 Detail Design

M L H V D C - E N G - E C I - D D - P C - 0 9 4 1 - 0 5 6 A

	姓名 Name	日期 Date
设计 Designed	倪	2020.3.5
校核 Checked	徐勇	2020.3.6
审核 Reviewed	王建华	2020.3.9
批准 Approved	李兆非	2020.3.12
比例 Scale		

500kV线路保护屏(R14) 交流电压回路图1

500kV Line Distance Protection(R14) Cubicle AC Voltage Circuit Diagram 1

图号 DWG NO.: 30-B003701S-D0914-056

版本 REV.: A

297X420