卷册检索号 SEARCH NO. OF THE VOLUME
MLHVDC-LCS-ECI-DD-CA-0246 30-B003701S-T0246

第 1 页 共 1 页
PAGE OF

图纸文件目录（首页）

CATALOG OF DRAWING DOCUMENTS (HEAD PAGE)

拉合尔±660kV换流站 工程 施工图 阶段
±660kV Lahore Converter Station PROJECT Detail Design DESIGN STAGE

建筑 专业 第 02 卷 第 46 册
Architecture SPECIALITY VOLUME BOOK

卷册名称 篮球场地坪图
Volume name Basketball court

批 准 APPROVED BY	
审 核 REVIEWED BY	
设计/勘测 DESIGNED BY/ SURVEYED BY	
图 纸 1 张 DRAWING NOS.	打印件 0 本 PRINTED COPIES NOS.

序号 No.	图 号 DRAWING NO.	文件名称 DOCUMENT TITLE	版本 EDITION	张 NOS.	本 NOS.	备注 REMARKS
1	30-B003701S-T0246-001	篮球场地坪图 Basketball court	A	1		

注:

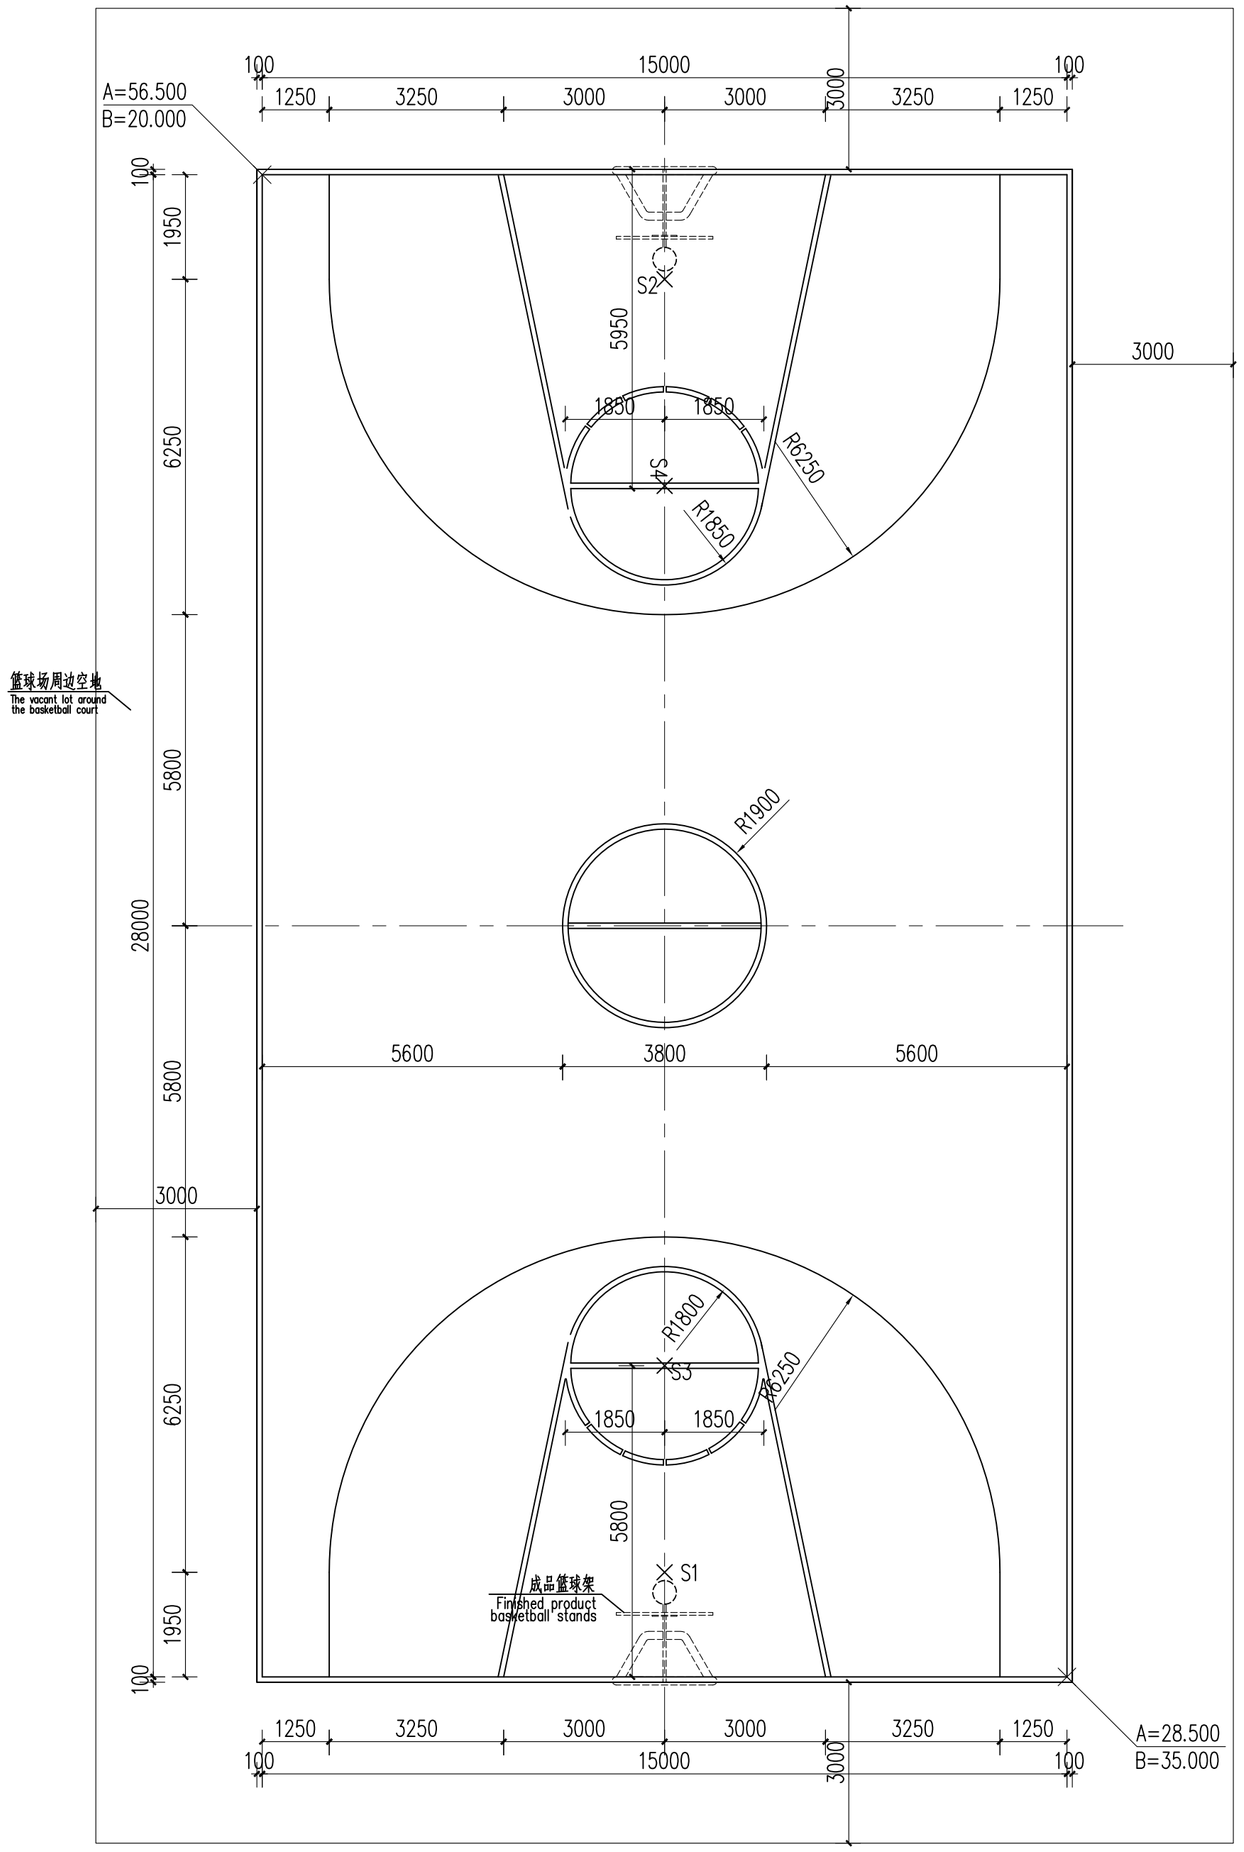

篮球场地
3 厚丙烯酸树脂面层
200 厚混凝土垫层 fc`=28MPa，分仓跳格浇注,表面拍浆抹平
200 厚级配碎石分两步夯实
素土夯实

Basketball court
3mm thick acrylic Resin surface layer
200mm thick concrete cushion layer fc`=28MPa, Compartment Jump casting, surface slurry leveling
200mm thick graded crushed stone divided into two-step tamping
Compacted soil

Reference Drawings

Drwg. No.	Title
30-B003701S-T0248	建筑通用详图 General details of the building

Revisions	Name	Date	Notes

巴基斯坦默蒂亚里—拉合尔±660kV直流输电工程
±660kV HVDC Project from Matiari to Lahore in Pakistan

NATIONAL TRANSMISSION & DESPATCH COMPANY (NTDC) LIMITED PAKISTAN

CONTRACTOR 国家电网 STATE GRID 中国电力技术装备有限公司 CHINA ELECTRIC POWER EQUIPMENT AND TECHNOLOGY CO.,LTD.

SUBCONTRACTOR East China Electric Power Design Institute Co.,Ltd.

拉合尔±660kV换流站
±660kV Lahore Converter Station

设计阶段 PHASE: 施工图 Construction Drawing

M L H V D C - L C S - E C I - D D - C A - 0 2 4 6 - 0 0 1 A

	姓名 Name	日期 Date
设计 Designed		2018.03.14
校核 Checked		2018.03.14
审核 Reviewed		2018.03.14
批准 Approved		2018.03.14

篮球场地坪图

Basketball court

比例 Scale: 1:100
图号 DWG NO.: 30-B003701S-T0246-001
版本 REV.: A

420X594