卷册检索号 SEARCH NO. OF THE VOLUME
MLHVDC-LCS-ECI-DD-EC-0413 30-B003701S-D0413

第 1 页 共 1 页
PAGE OF

图纸文件目录（首页）

CATALOG OF DRAWING DOCUMENTS (HEAD PAGE)

拉合尔±660kV换流站 工程 施工图 阶段
±660kV Lahore Converter Station PROJECT Detail Design DESIGN STAGE

电气 专业 第 04 卷 第 13 册
Electrical SPECIALITY VOLUME BOOK

卷册名称 阀厅电缆埋管
Volume name Cable buried pipe of Valve Hall

批 准 APPROVED BY	2018.01.16
审 核 REVIEWED BY	
设计/勘测 DESIGNED BY/ SURVEYED BY	2018.01.16
图 纸 2 张 DRAWING NOS.	打印件 0 本 PRINTED COPIES NOS.

序号 No.	图 号 DRAWING NO.	文 件 名 称 DOCUMENT TITLE	版本 EDITION	张 NOS.	本 NOS.	备注 REMARKS
1	30-B003701S-D0413-001	极1阀厅电缆埋管图 Calbe buried pipe of P1VH	A	1		
2	30-B003701S-D0413-002	极2阀厅电缆埋管图 Calbe buried pipe of P2VH	A	1		

注：

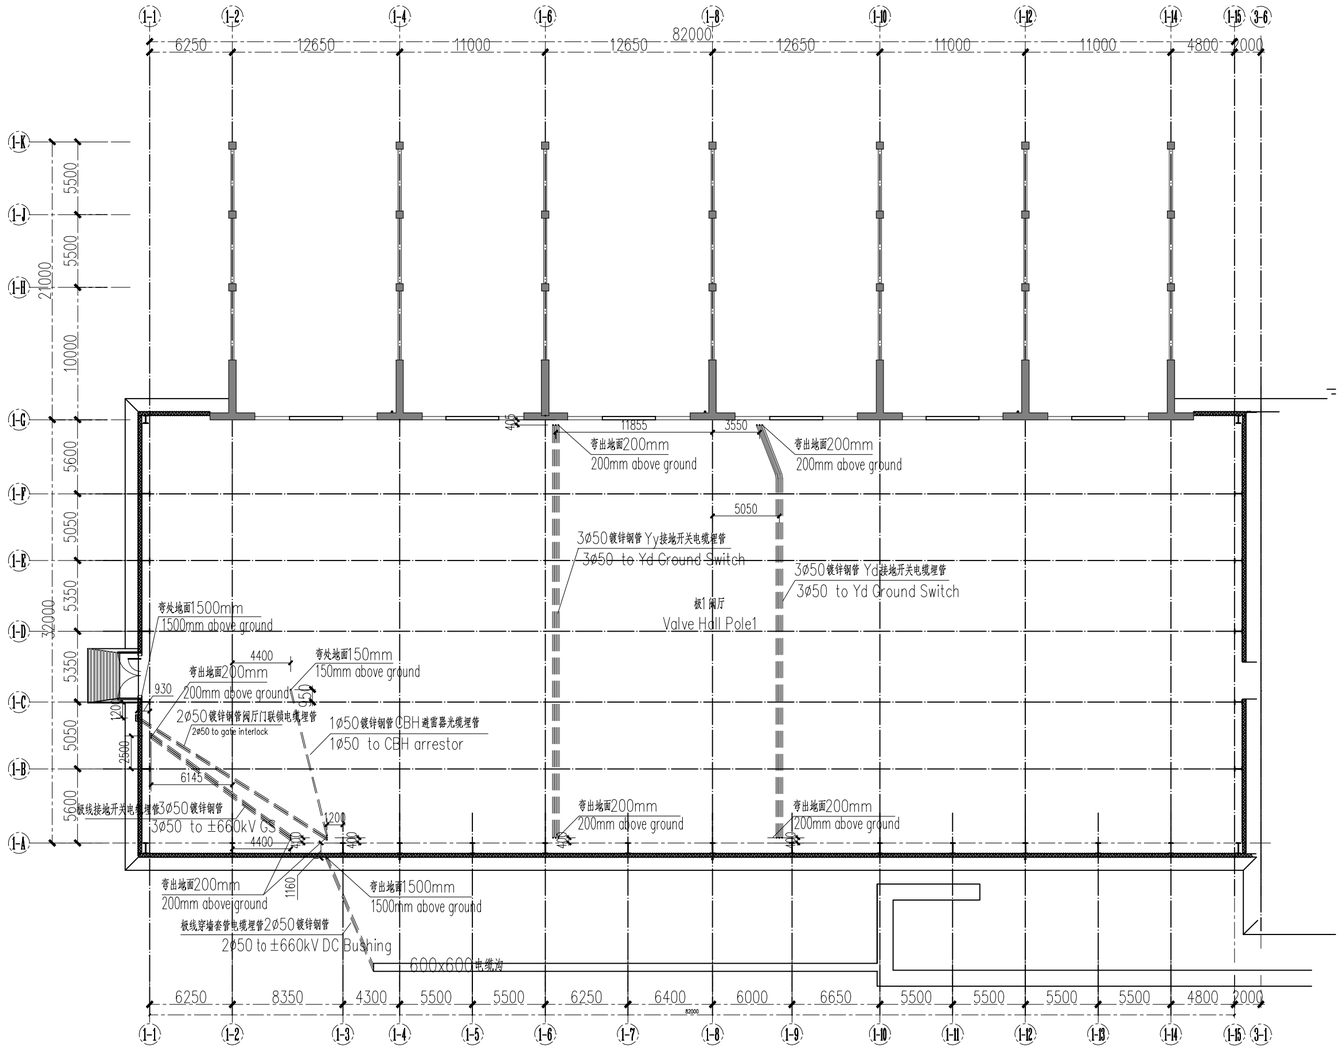

注:

1. Yy、Yd接地开关埋管埋深为-1.60m（阀厅地面标高为±0.00m），施工时注意与暖通地面风管图纸相结合，避免碰撞.
2. 其余埋管埋深为-0.60m（阀厅地面标高为±0.00m）. 所有埋管材料均为热镀锌钢管.
3. 所有埋管敷设时应与阀厅基础图相结合，避免与基础碰撞. 埋管的转弯半径应大于埋管直径的10倍.
4. 所有埋管一端应采用-50x5镀锌扁钢与水平接地体两点连接. 水平接地体的布置图、埋管接地的材料量均开列在D0411卷册.

Notes:

1. The depth of the cable buried pipe of Yy/Yd ground switch is -1.60m (The Valve Hall ground is ±0.00m). Construct with the drawing of air tunnel to avoid collision.
2. The depth of other cable buried pipe is -0.60m. All the buried pipes are galvanized steel pipes.
3. Construct with the foundation drawings to avoid collision. The turning radius of the buried pipe should be at least 10 times the diameter of the buried pipe.
4. One end of the buried pipe should be connected by two points of 50x5 galvanized steel strap with earthing electrode. The earthing matericals are listed in volumn D0411.

阀厅设备埋管材料表

序号 No.	名称 Designation	规范 Specification	单位 Unit	数量 Quan	备注 Remark
1	镀锌钢管 galvanized steel pipe	Ø50	米(m)	300	

Reference Drawings

Drwg. No.	Title

Revisions

	Name	Date	Notes

巴基斯坦默蒂亚里—拉合尔±660kV直流输电工程

±660kV HVDC Project from Matiari to Lahore in Pakistan

NATIONAL TRANSMISSION & DESPATCH COMPANY (NTDC) LIMITED PAKISTAN

CONTRACTOR 国家电网 STATE GRID 士阳电力技术设备有限公司

SUBCONTRACTOR East China Electric Power Design Institute Co.,Ltd.

拉合尔±660kV换流站

±660kV Lahore Converter Station

设计阶段 PHASE: 施工图 Detail Design

M L H V D C - L C S - E C I - D D - E C - 0 4 1 3 - 0 0 1 A

	姓名 Name	日期 Date
设计 Designed	武映卿	2018.01.16
校核 Checked	张谢平	2018.01.16
审核 Reviewed		
批准 Approved	郑煜	2018.01.16
比例 Scale	1:300	

极1阀厅电缆埋管图

Cable buried pipe of P1VH

图号 DWG NO.: 30-B003701S-D0413-001

版本 REV.: A

A2(594x420)

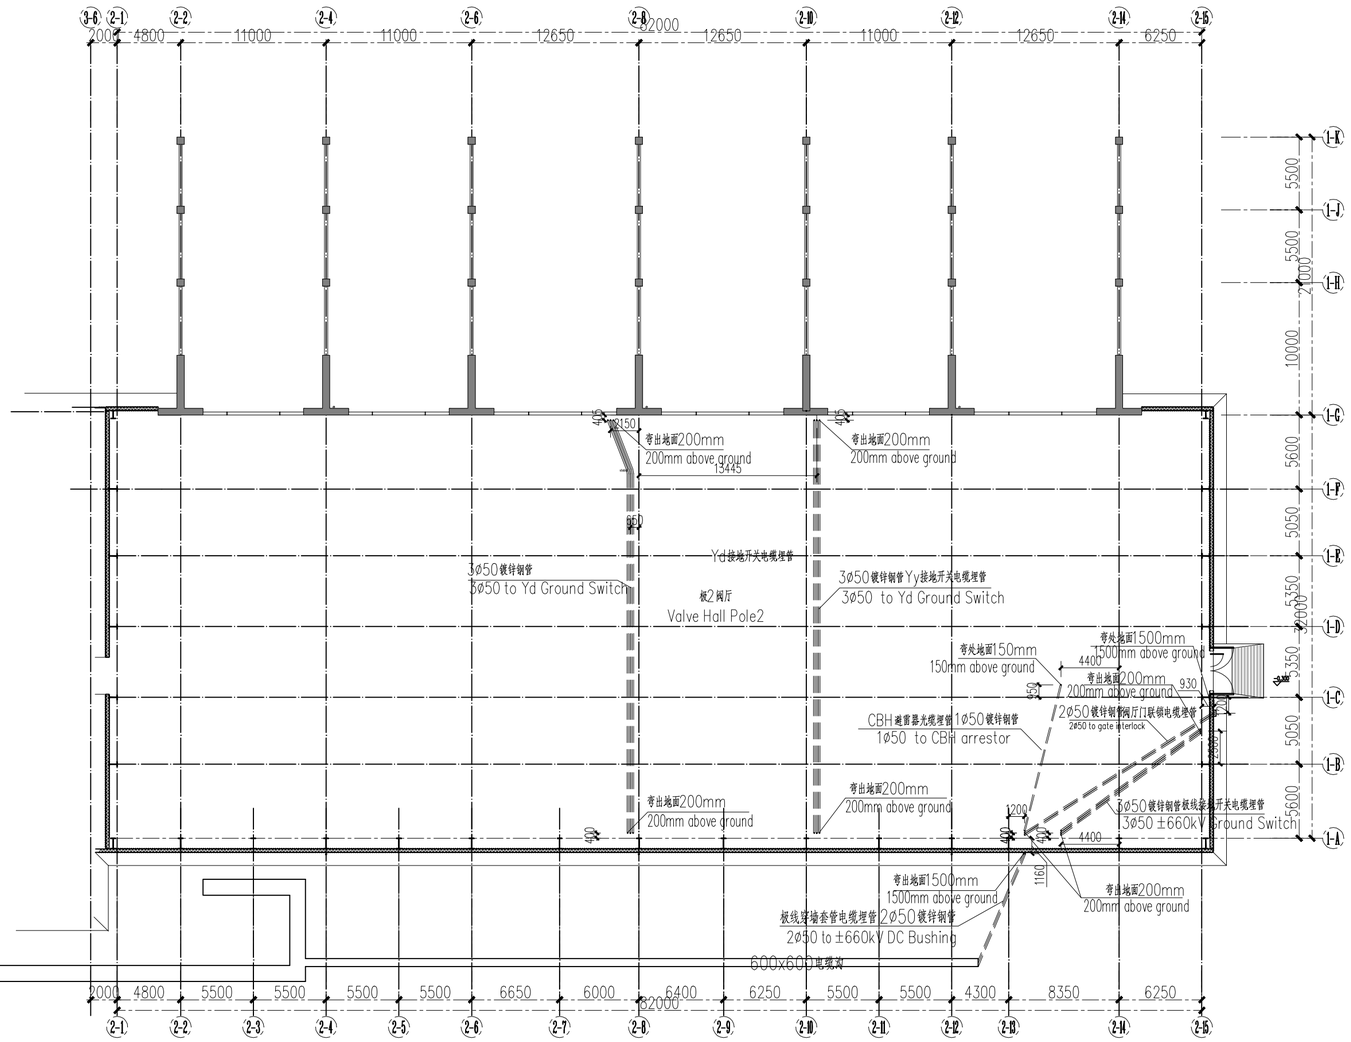

注:

1. Yy、Yd接地开关埋管埋深为-1.60m（阀厅地面标高为±0.00m），施工时注意与暖通地面风管图纸相结合，避免碰撞.
2. 其余埋管埋深为-0.60m（阀厅地面标高为±0.00m）. 所有埋管材料均为热镀锌钢管.
3. 所有埋管敷设时应与阀厅基础图相结合，避免与基础碰撞. 埋管的转弯半径应大于埋管直径的10倍.
4. 所有埋管一端应采用-50x5镀锌扁钢与水平接地体两点连接. 水平接地体的布置图、埋管接地的材料量均开列在D0411卷册.

Notes:

1. The depth of the cable buried pipe of Yy/Yd ground switch is -1.60m (The Valve Hall ground is ±0.00m). Construct with the drawing of air tunnel to avoid collision.
2. The depth of other cable buried pipe is -0.60m. All the buried pipes are galvanized steel pipes.
3. Construct with the foundation drawings to avoid collision. The turning radius of the buried pipe should be at least 10 times the diameter of the buried pipe.
4. One end of the buried pipe should be connected by two points of 50x5 galvanized steel strap with earthing electrode. The earthing matericals are listed in volumn D0411.

阀厅设备埋管材料表

序号 No.	名称 Designation	规范 Specification	单位 Unit	数量 Quan	备注 Remark
1	镀锌钢管 galvanized steel pipe	Ø50	米(m)	300	

Reference Drawings

Drwg. No.	Title

Revisions

Name	Date	Notes

巴基斯坦默蒂亚里—拉合尔±660kV直流输电工程

±660kV HVDC Project from Matiari to Lahore in Pakistan

NATIONAL TRANSMISSION & DESPATCH COMPANY (NTDC) LIMITED PAKISTAN

CONTRACTOR 国家电网 STATE GRID 中国电力技术装备有限公司

SUBCONTRACTOR East China Electric Power Design Institute Co.,Ltd.

拉合尔±660kV换流站

±660kV Lahore Converter Station

设计阶段 PHASE: 施工图 Detail Design

MLHVDC-LCS-ECI-DD-EC-0413-002A

	姓名 Name	日期 Date
设计 Designed	王晓坤	2018.01.16
校核 Checked	张谢平	2018.01.16
审核 Reviewed		
批准 Approved	郑煜	2018.01.16
比例 Scale	1:300	

极2阀厅电缆埋管图

Cable buried pipe of P2VH

图号 DWG NO.: 30-B003701S-D0413-002

版本 REV.: A

A2(594x420)