卷册检索号 SEARCH NO. OF THE VOLUME
MLHVDC-ENG-ECI-DD-PC-1053 30-B003701S-D1053

图纸文件目录（首页）

CATALOG OF DRAWING DOCUMENTS (HEAD PAGE)

拉合尔±660kV换流站 工程 施工图 阶段
±660kV Lahore Converter Station PROJECT Detail Design DESIGN STAGE

电气 专业 第 10 卷 第 53 册
Electrical SPECIALITY VOLUME BOOK

卷册名称 35kV/11kV站用变压器二次线
Volume name Schematic of 35/11kV Auxiliary Transformer

批 准 APPROVED BY	
审 核 REVIEWED BY	
设计/勘测 DESIGNED BY/ SURVEYED BY	董利宇
图 纸 6 张 DRAWING NOS.	打印件 1 本 PRINTED COPIES NOS.

序号 No.	图 号 DRAWING NO.	文件名称 DOCUMENT TITLE	版本 EDITION	张 NOS.	本 NOS.	备注 REMARKS
1	30-B003701S-D1053-001	1号35/10kV站用变本体接线图一 Wiring diagram 1 of =WC1-31B.J	A	1		
2	30-B003701S-D1053-002	1号35/10kV站用变本体接线图二 Wiring diagram 2 of =WC1-31B.J	A	1		
3	30-B003701S-D1053-003	2号35/10kV站用变本体接线图一 Wiring diagram 1 of =WC2-32B.J	A	1		
4	30-B003701S-D1053-004	2号35/10kV站用变本体接线图二 Wiring diagram 2 of =WC2-32B.J	A	1		
5	30-B003701S-D1053-005	1号35/10kV站用变本体端子箱端子排图 Terminal Diagram of =WC1-31B.J	A	1		
6	30-B003701S-D1053-006	2号35/10kV站用变本体端子箱端子排图 Terminal Diagram of =WC2-32B.J	A	1		

注:

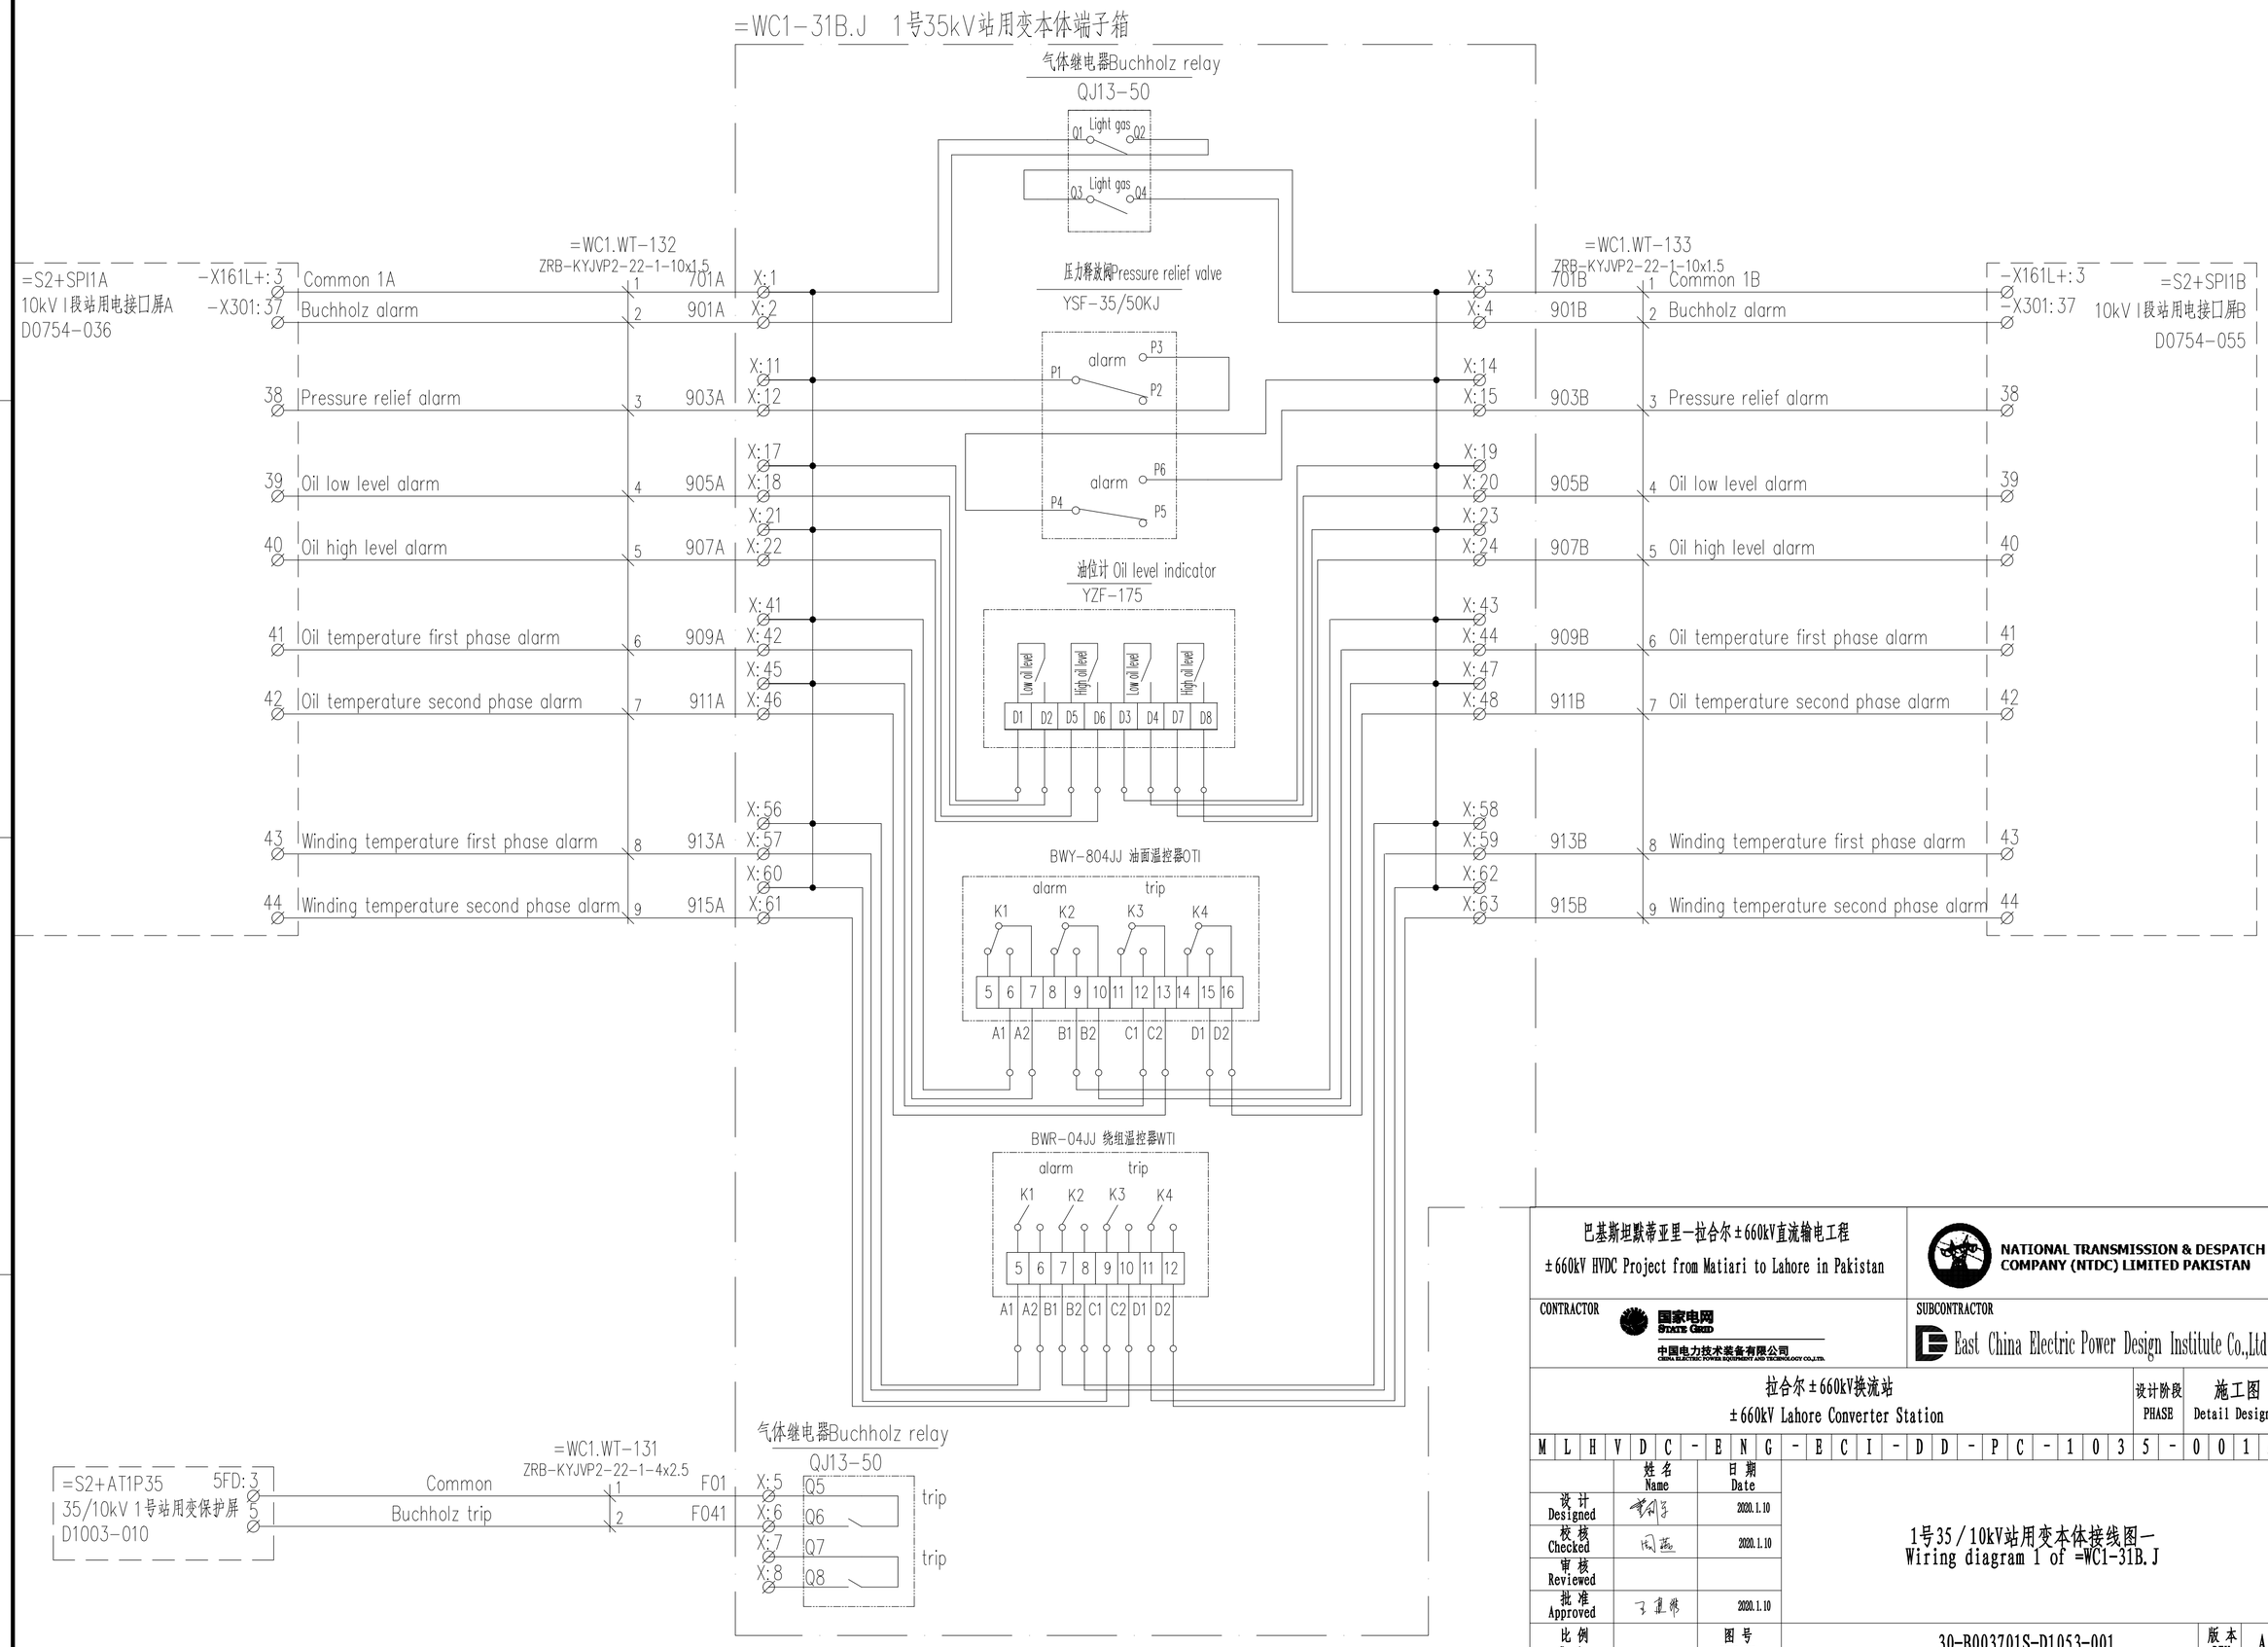

巴基斯坦默蒂亚里—拉合尔±660kV直流输电工程

±660kV HVDC Project from Matiari to Lahore in Pakistan

NATIONAL TRANSMISSION & DESPATCH COMPANY (NTDC) LIMITED PAKISTAN

CONTRACTOR 国家电网 STATE GRID 中国电力技术装备有限公司 CHINA ELECTRIC POWER EQUIPMENT AND TECHNOLOGY CO.,LTD.

SUBCONTRACTOR East China Electric Power Design Institute Co.,Ltd.

拉合尔±660kV换流站

±660kV Lahore Converter Station

设计阶段 PHASE: 施工图 Detail Design

M L H V D C - E N G - E C I - D D - P C - 1 0 3 5 - 0 0 1 A

	姓名 Name	日期 Date
设计 Designed		2020.1.10
校核 Checked		2020.1.10
审核 Reviewed		
批准 Approved		2020.1.10

1号35/10kV站用变本体接线图一

Wiring diagram 1 of =WC1-31B.J

比例 Scale

图号 DWG NO. 30-B003701S-D1053-001

版本 REV. A

297X420

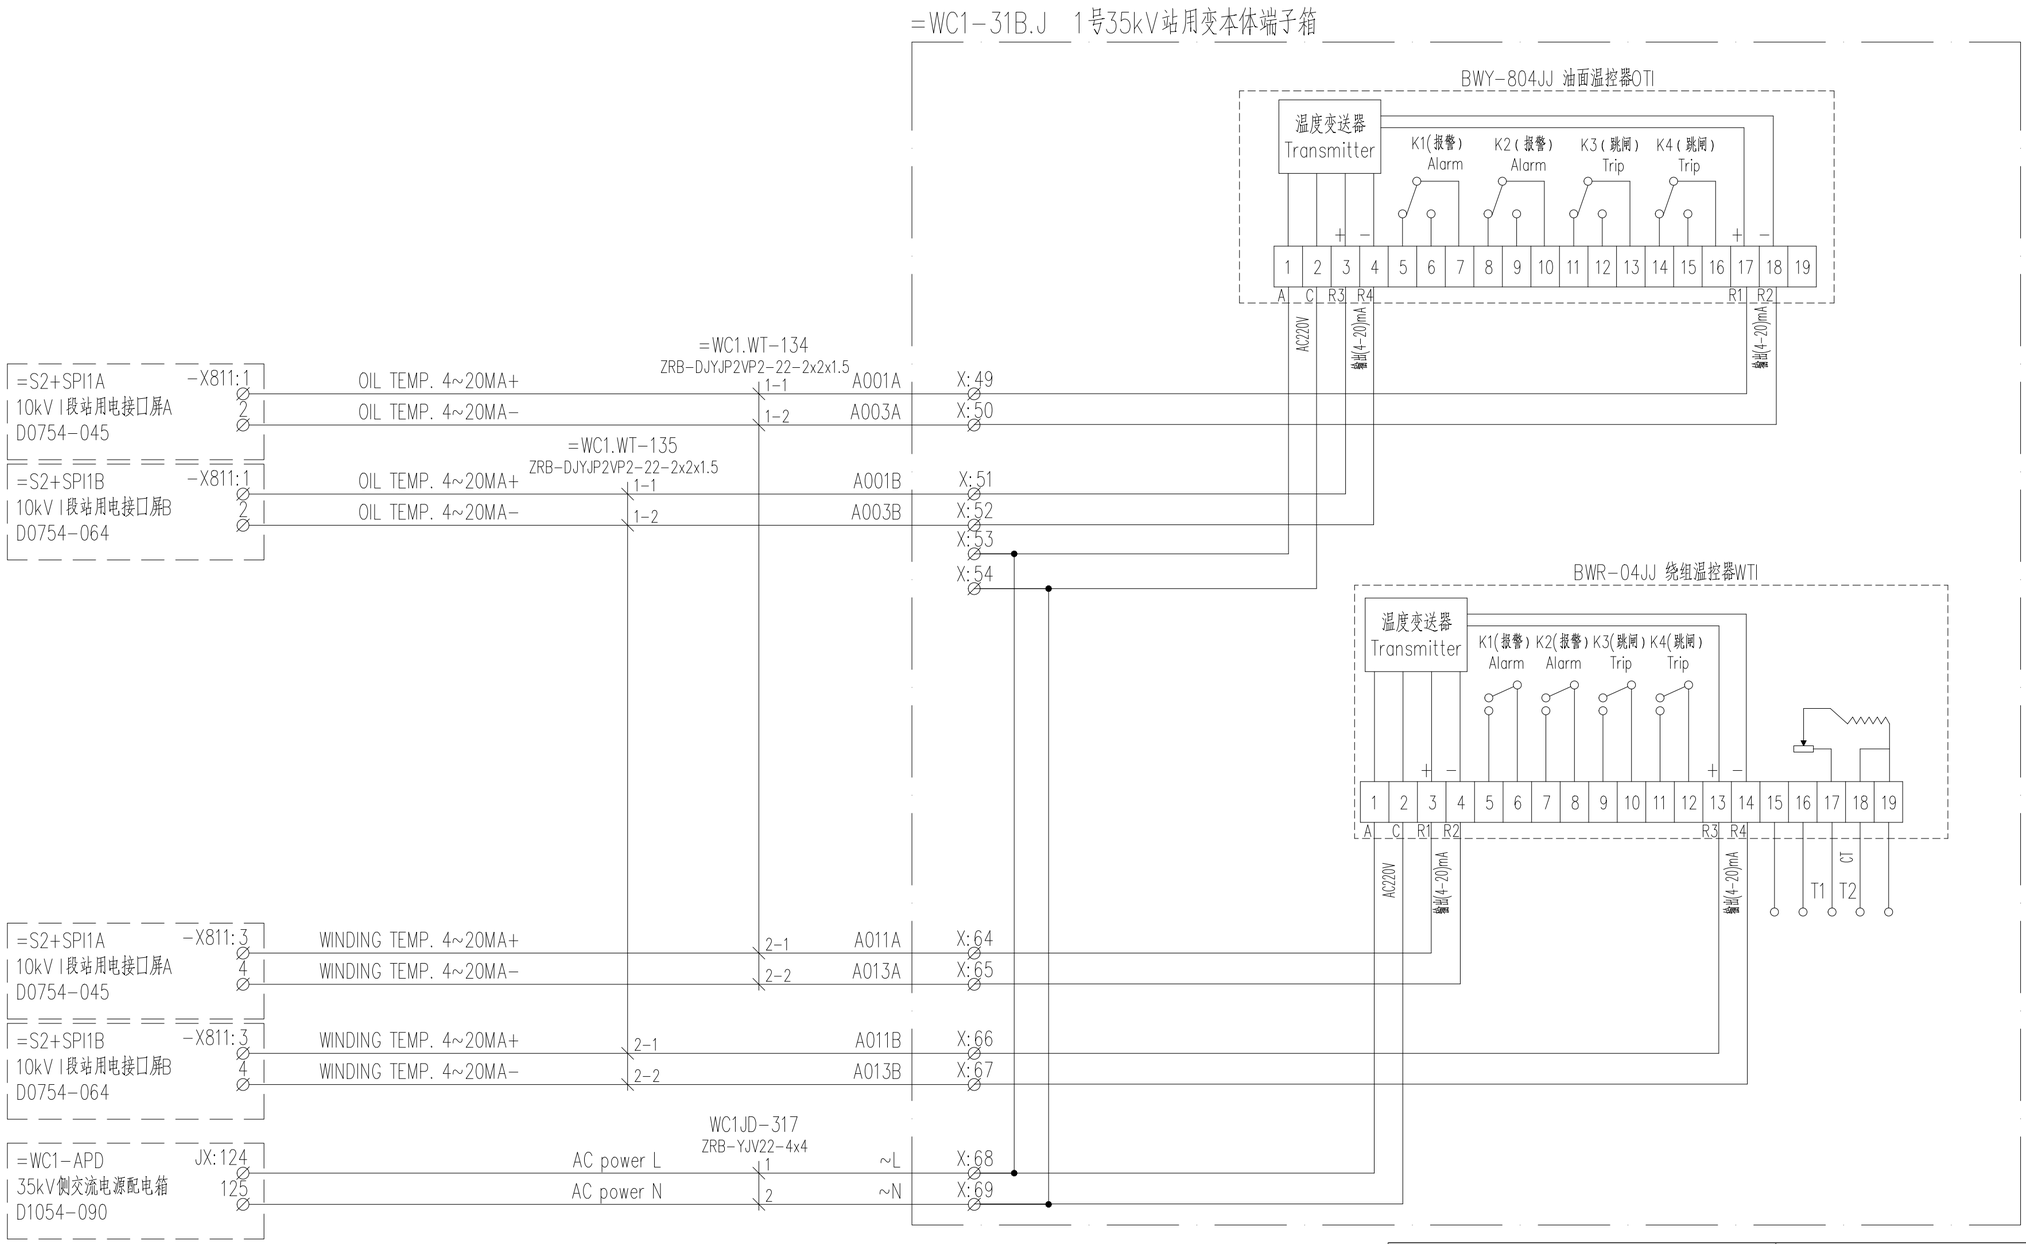

巴基斯坦默蒂亚里—拉合尔±660kV直流输电工程

±660kV HVDC Project from Matiari to Lahore in Pakistan

NATIONAL TRANSMISSION & DESPATCH COMPANY (NTDC) LIMITED PAKISTAN

CONTRACTOR 国家电网 STATE GRID 中国电力技术装备有限公司 CHINA ELECTRIC POWER EQUIPMENT AND TECHNOLOGY CO.,LTD.

SUBCONTRACTOR East China Electric Power Design Institute Co.,Ltd.

拉合尔±660kV换流站

±660kV Lahore Converter Station

设计阶段 PHASE: 施工图 Detail Design

M L H V D C - E N G - E C I - D D - P C - 1 0 3 5 - 0 0 2 A

	姓名 Name	日期 Date
设计 Designed		2020.1.10
校核 Checked		2020.1.10
审核 Reviewed		
批准 Approved		2020.1.10
比例 Scale		图号 DWG NO.

1号35/10kV站用变本体接线图二

Wiring diagram 2 of =WC1-31B.J

30-B003701S-D1053-002

版本 REV. A

297X420

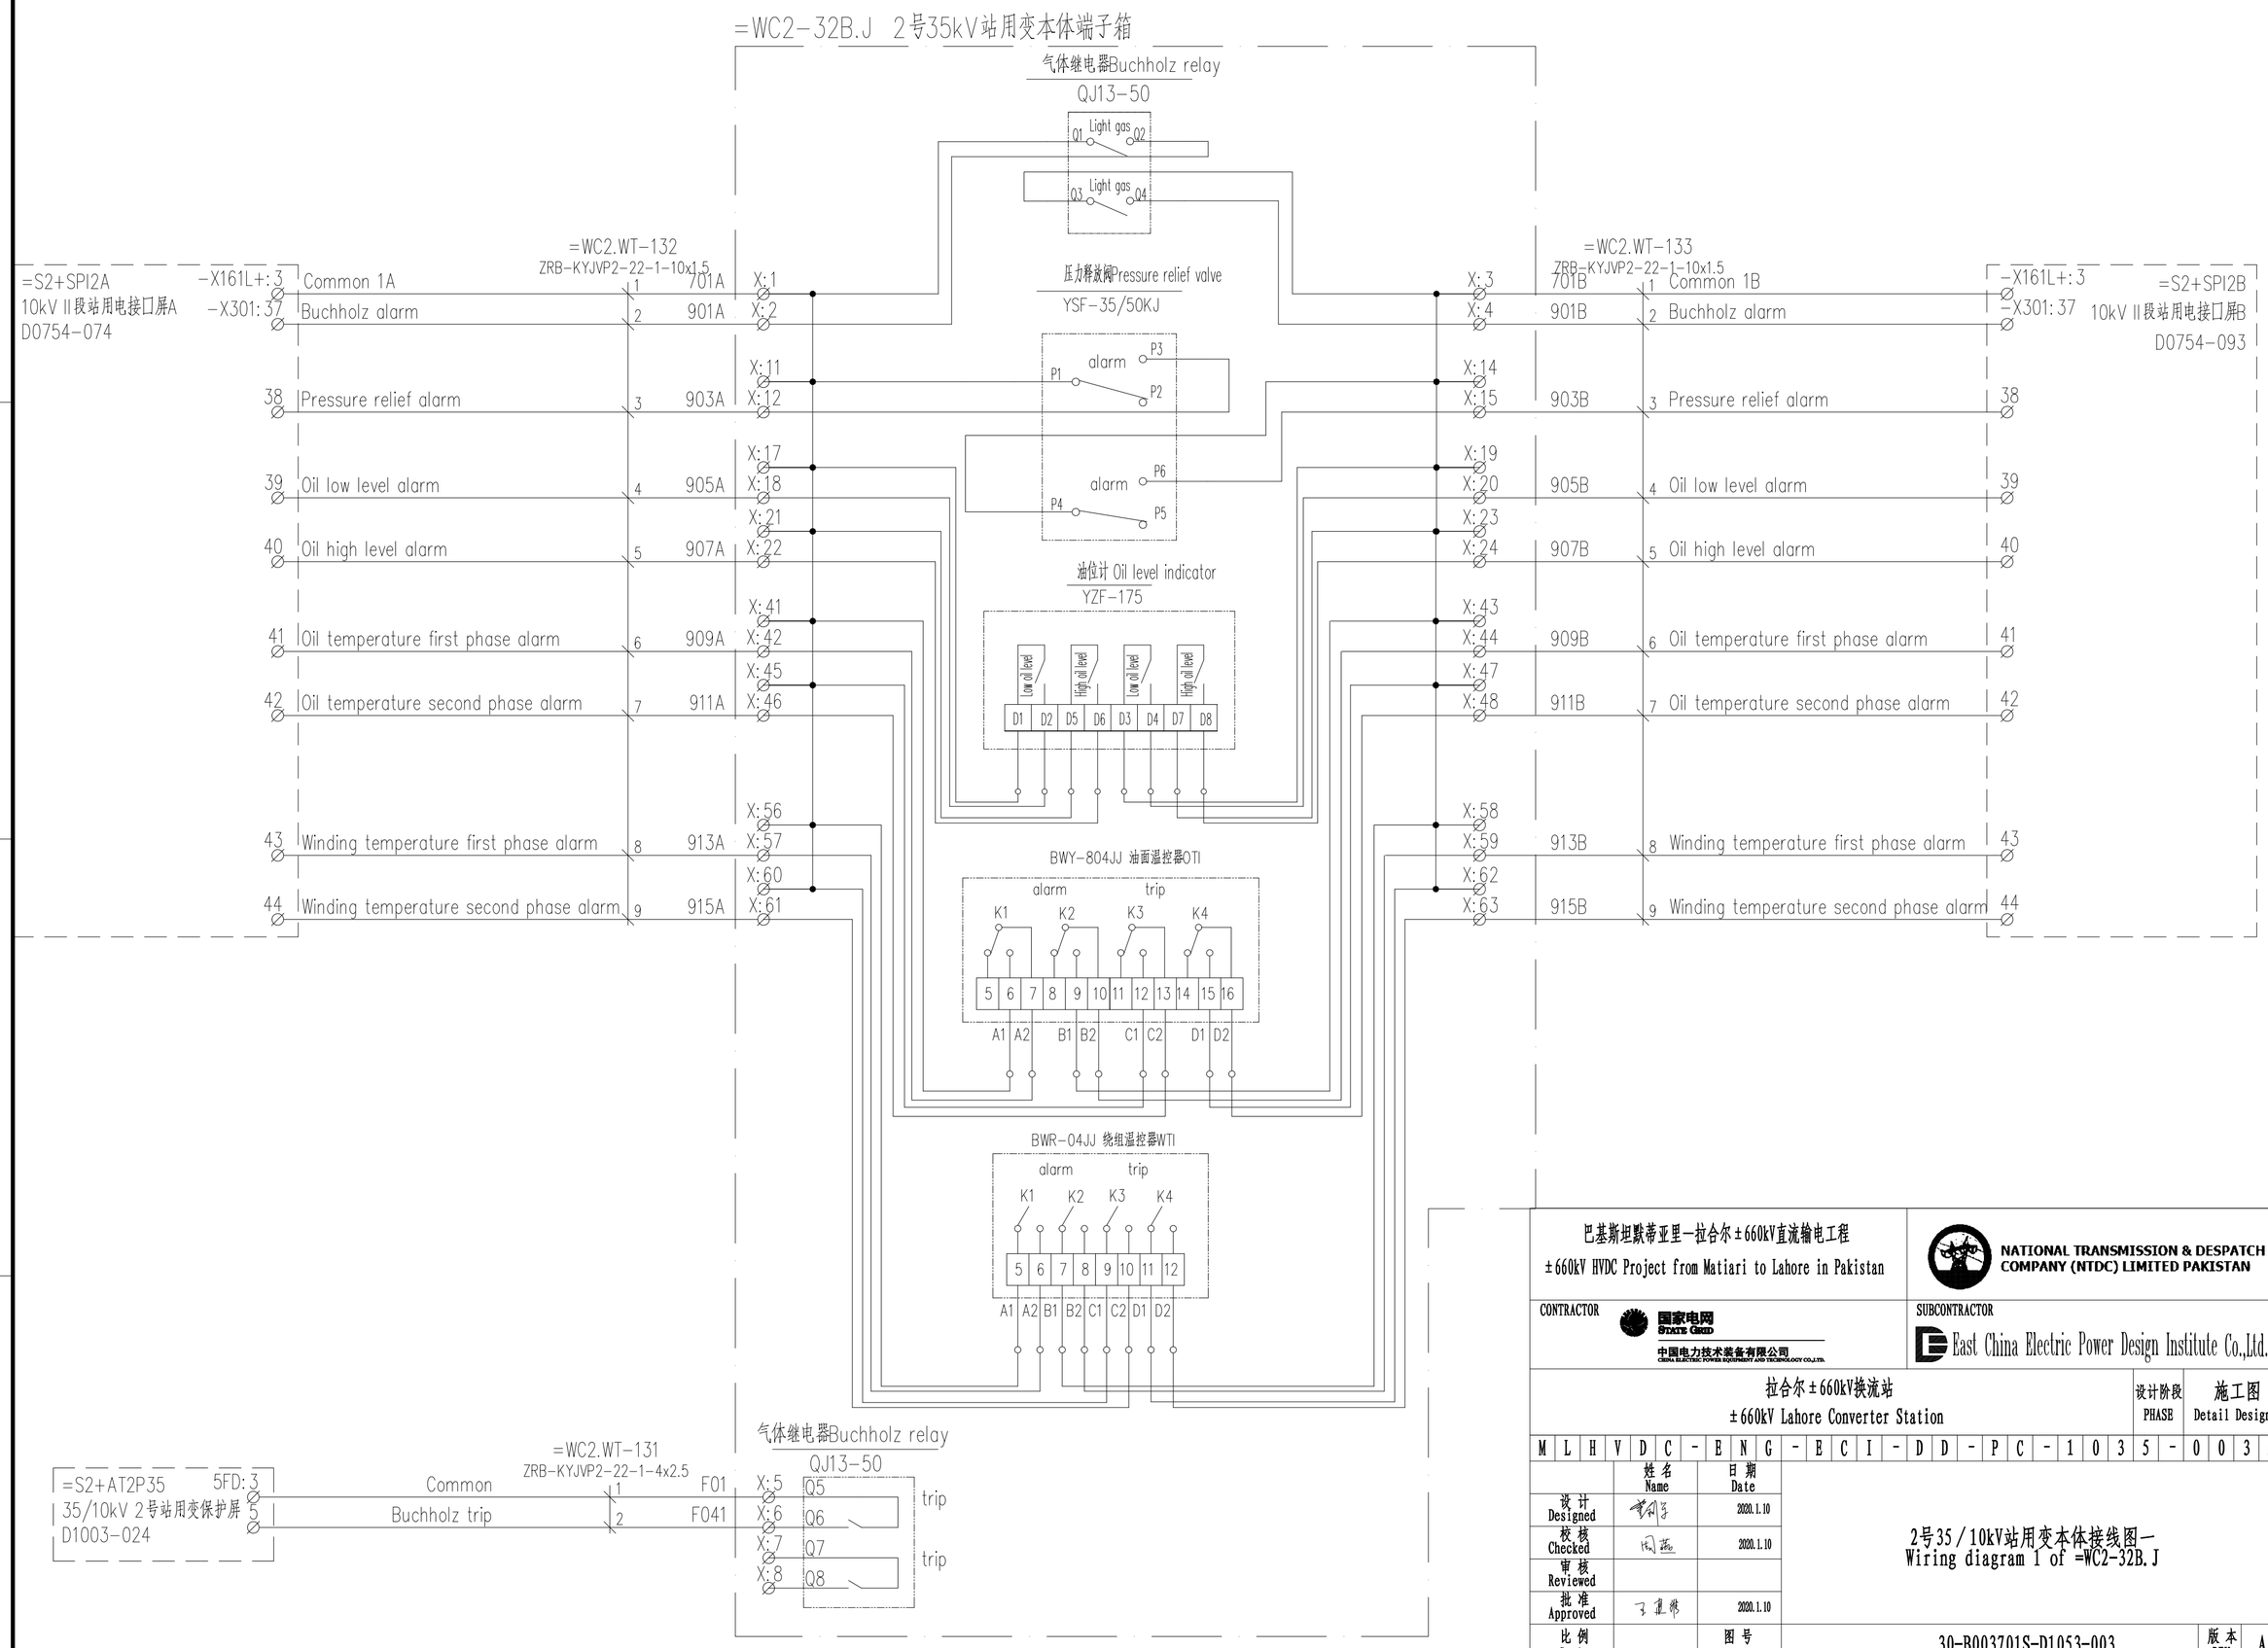
=WC2-32B.J 2号35kV站用变本体端子箱
气体继电器Buchholz relay
QJ13-50
Light gas
Q1
Q2
Q3
Q4
=WC2.WT-132
ZRB-KYJVP2-22-1-10x1.5
=WC2.WT-133
ZRB-KYJVP2-22-1-10x1.5
=S2+SPI2A
10kV II段站用电接口屏A
D0754-074
=S2+SPI2B
10kV II段站用电接口屏B
D0754-093
-X161L+:3
-X301:37
Common 1A
Buchholz alarm
Pressure relief alarm
Oil low level alarm
Oil high level alarm
Oil temperature first phase alarm
Oil temperature second phase alarm
Winding temperature first phase alarm
Winding temperature second phase alarm
Common 1B
701A
901A
903A
905A
907A
909A
911A
913A
915A
701B
901B
903B
905B
907B
909B
911B
913B
915B
压力释放阀Pressure relief valve
YSF-35/50KJ
alarm
P1
P2
P3
P4
P5
P6
油位计 Oil level indicator
YZF-175
Low oil level
High oil level
D1 D2 D5 D6 D3 D4 D7 D8
BWY-804JJ 油面温控器OTI
alarm
trip
K1 K2 K3 K4
5 6 7 8 9 10 11 12 13 14 15 16
A1 A2 B1 B2 C1 C2 D1 D2
BWR-04JJ 绕组温控器WTI
5 6 7 8 9 10 11 12
=WC2.WT-131
ZRB-KYJVP2-22-1-4x2.5
=S2+AT2P35
35/10kV 2号站用变保护屏
D1003-024
5FD:3
5
Common
Buchholz trip
F01
F041
Q5
Q6
Q7
Q8
trip
巴基斯坦默蒂亚里—拉合尔±660kV直流输电工程
±660kV HVDC Project from Matiari to Lahore in Pakistan
NATIONAL TRANSMISSION & DESPATCH COMPANY (NTDC) LIMITED PAKISTAN
CONTRACTOR
国家电网 STATE GRID
中国电力技术装备有限公司
SUBCONTRACTOR
East China Electric Power Design Institute Co.,Ltd.
拉合尔±660kV换流站
±660kV Lahore Converter Station
设计阶段 PHASE
施工图 Detail Design
M L H V D C - E N G - E C I - D D - P C - 1 0 3 5 - 0 0 3 A
姓名 Name
日期 Date
设计 Designed
2020.1.10
校核 Checked
2020.1.10
审核 Reviewed
批准 Approved
2020.1.10
2号35/10kV站用变本体接线图一
Wiring diagram 1 of =WC2-32B.J
比例 Scale
图号 DWG NO.
30-B003701S-D1053-003
版本 REV.
A

297X420

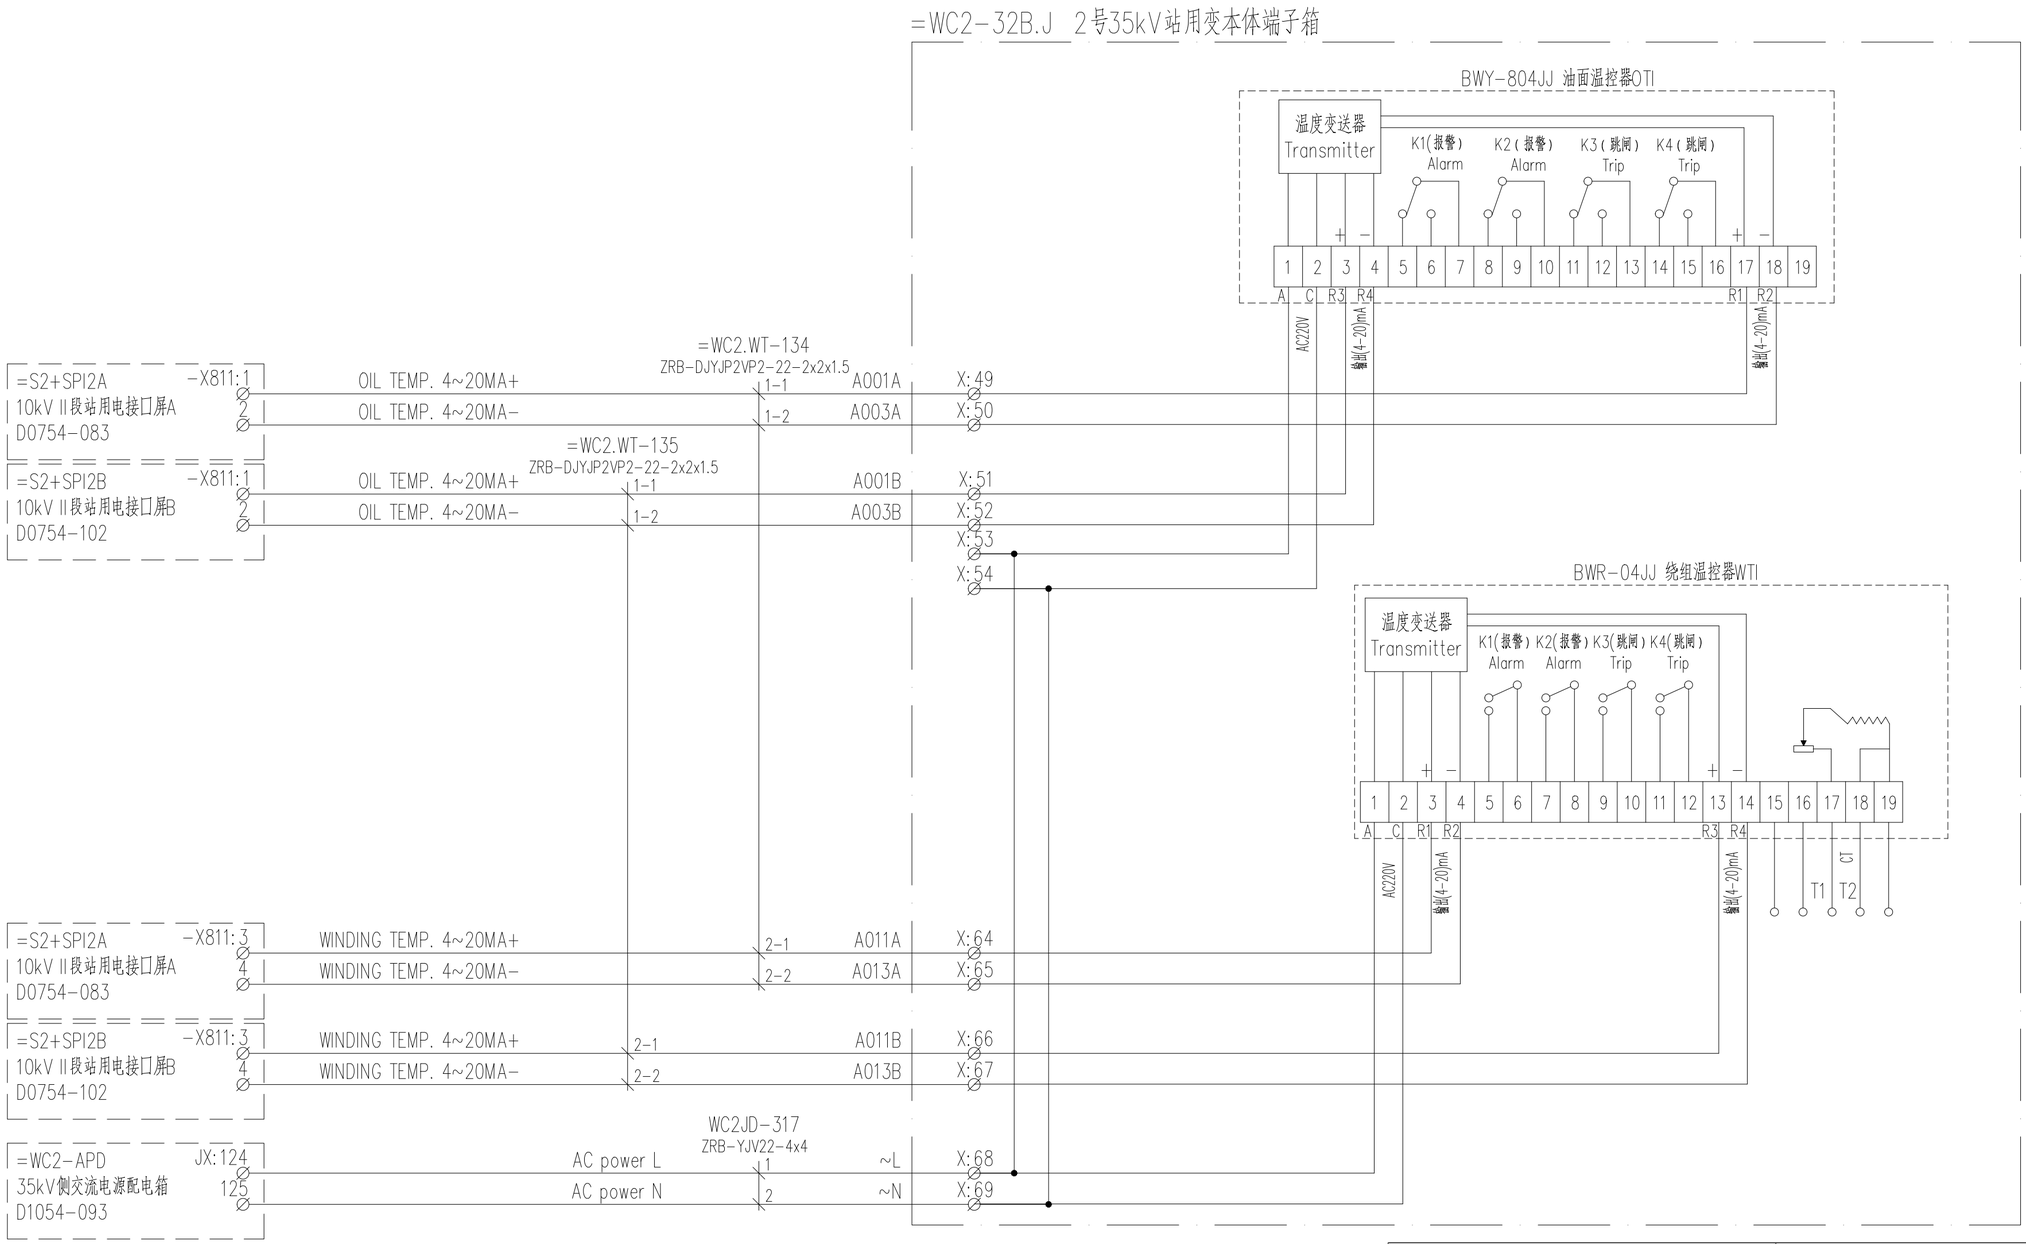

巴基斯坦默蒂亚里—拉合尔±660kV直流输电工程

±660kV HVDC Project from Matiari to Lahore in Pakistan

NATIONAL TRANSMISSION & DESPATCH COMPANY (NTDC) LIMITED PAKISTAN

CONTRACTOR 国家电网 STATE GRID 中国电力技术装备有限公司 CHINA ELECTRIC POWER EQUIPMENT AND TECHNOLOGY CO.,LTD.

SUBCONTRACTOR East China Electric Power Design Institute Co.,Ltd.

拉合尔±660kV换流站

±660kV Lahore Converter Station

设计阶段 PHASE: 施工图 Detail Design

M L H V D C - E N G - E C I - D D - P C - 1 0 3 5 - 0 0 4 A

	姓名 Name	日期 Date
设计 Designed		2020.1.10
校核 Checked		2020.1.10
审核 Reviewed		
批准 Approved		2020.1.10
比例 Scale		图号 DWG NO.

2号35/10kV站用变本体接线图二

Wiring diagram 2 of =WC2-32B.J

30-B003701S-D1053-004

版本 REV. A

297X420

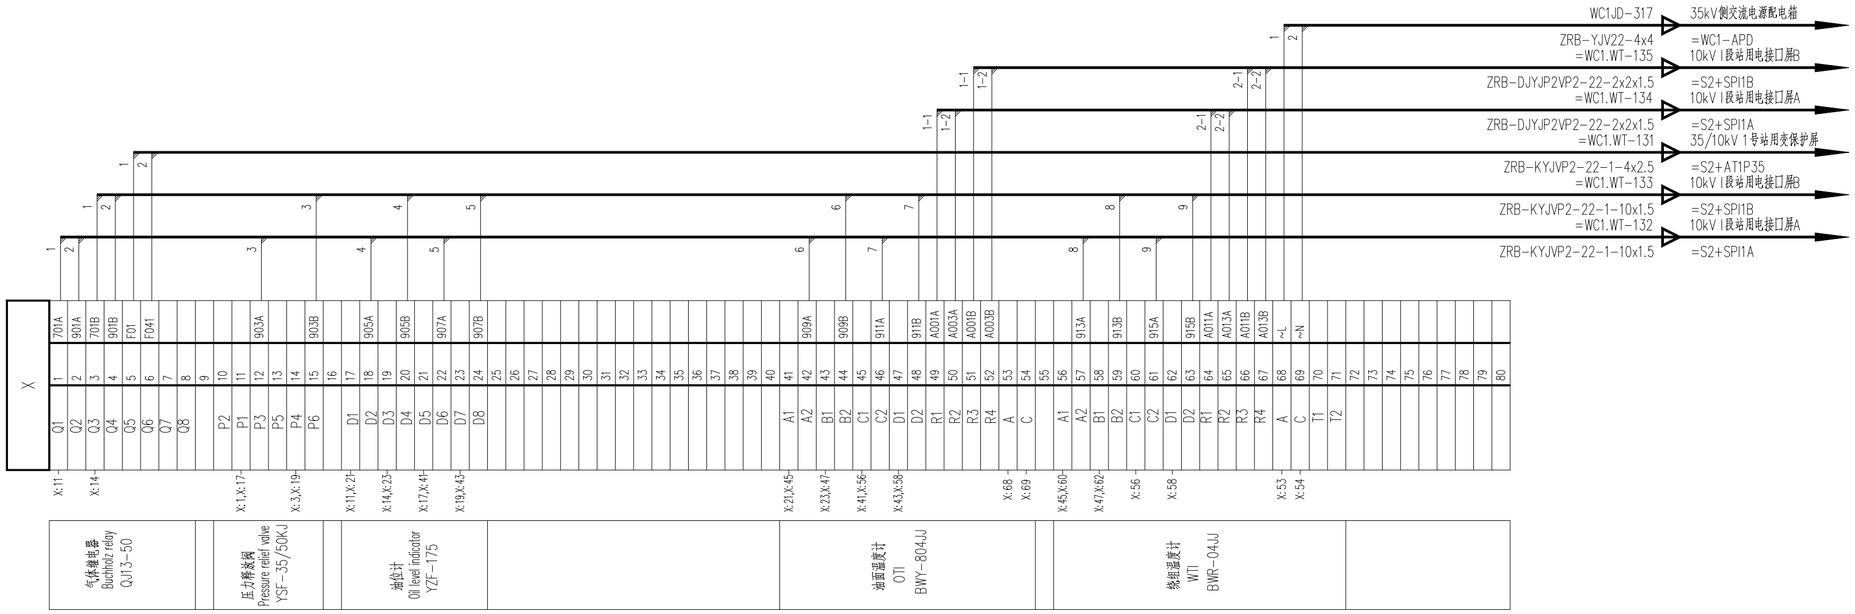

巴基斯坦默蒂亚里—拉合尔±660kV直流输电工程

±660kV HVDC Project from Matiari to Lahore in Pakistan

NATIONAL TRANSMISSION & DESPATCH COMPANY (NTDC) LIMITED PAKISTAN

CONTRACTOR 国家电网 STATE GRID 中国电力技术装备有限公司 CHINA ELECTRIC POWER EQUIPMENT AND TECHNOLOGY CO.,LTD.

SUBCONTRACTOR East China Electric Power Design Institute Co.,Ltd.

拉合尔±660kV换流站

±660kV Lahore Converter Station

设计阶段 PHASE: 施工图 Detail Design

M L H V D C - E N G - E C I - D D - P C - 1 0 5 3 - 0 0 5 A

	姓名 Name	日期 Date
设计 Designed		2020.1.10
校核 Checked		2020.1.10
审核 Reviewed		
批准 Approved		2020.1.10

1号35/10kV站用变本体端子箱端子排图
Terminal Diagram of =WC1-31B.J

比例 Scale:

图号 DWG NO.: 30-B003701S-D1053-005

版本 REV.: A

420X594

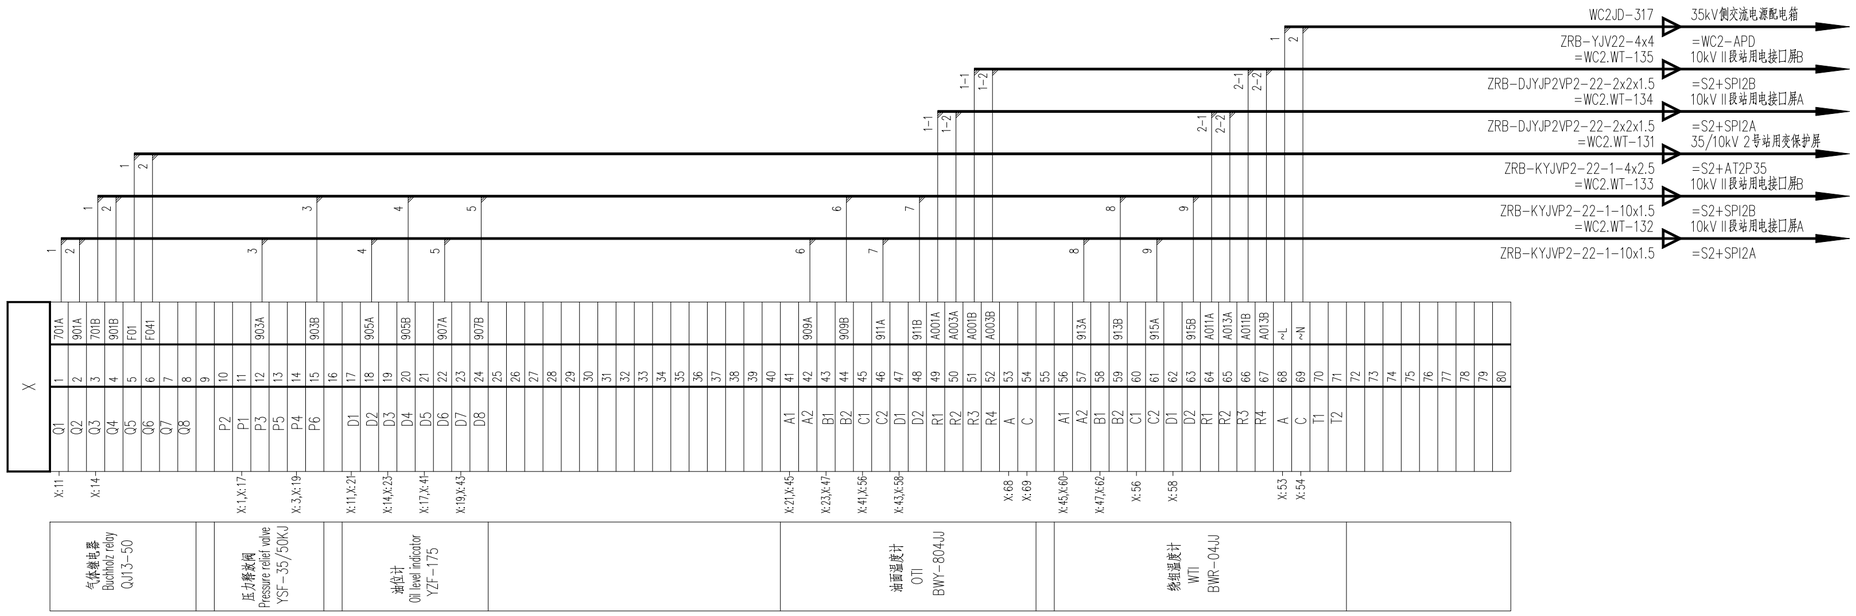

巴基斯坦默蒂亚里—拉合尔±660kV直流输电工程

±660kV HVDC Project from Matiari to Lahore in Pakistan

NATIONAL TRANSMISSION & DESPATCH COMPANY (NTDC) LIMITED PAKISTAN

CONTRACTOR 国家电网 STATE GRID 中国电力技术装备有限公司 CHINA ELECTRIC POWER EQUIPMENT AND TECHNOLOGY CO.,LTD.

SUBCONTRACTOR East China Electric Power Design Institute Co.,Ltd.

拉合尔±660kV换流站

±660kV Lahore Converter Station

设计阶段 PHASE: 施工图 Detail Design

M L H V D C - E N G - E C I - D D - P C - 1 0 5 3 - 0 0 6 A

	姓名 Name	日期 Date
设计 Designed	[illegible]	2020.1.10
校核 Checked	[illegible]	2020.1.10
审核 Reviewed		
批准 Approved	[illegible]	2020.1.10
比例 Scale		图号 DWG NO.

2号35/10kV站用变本体端子箱端子排图
Terminal Diagram of =WC2-32B.J

30-B003701S-D1053-006

版本 REV. A

420X594