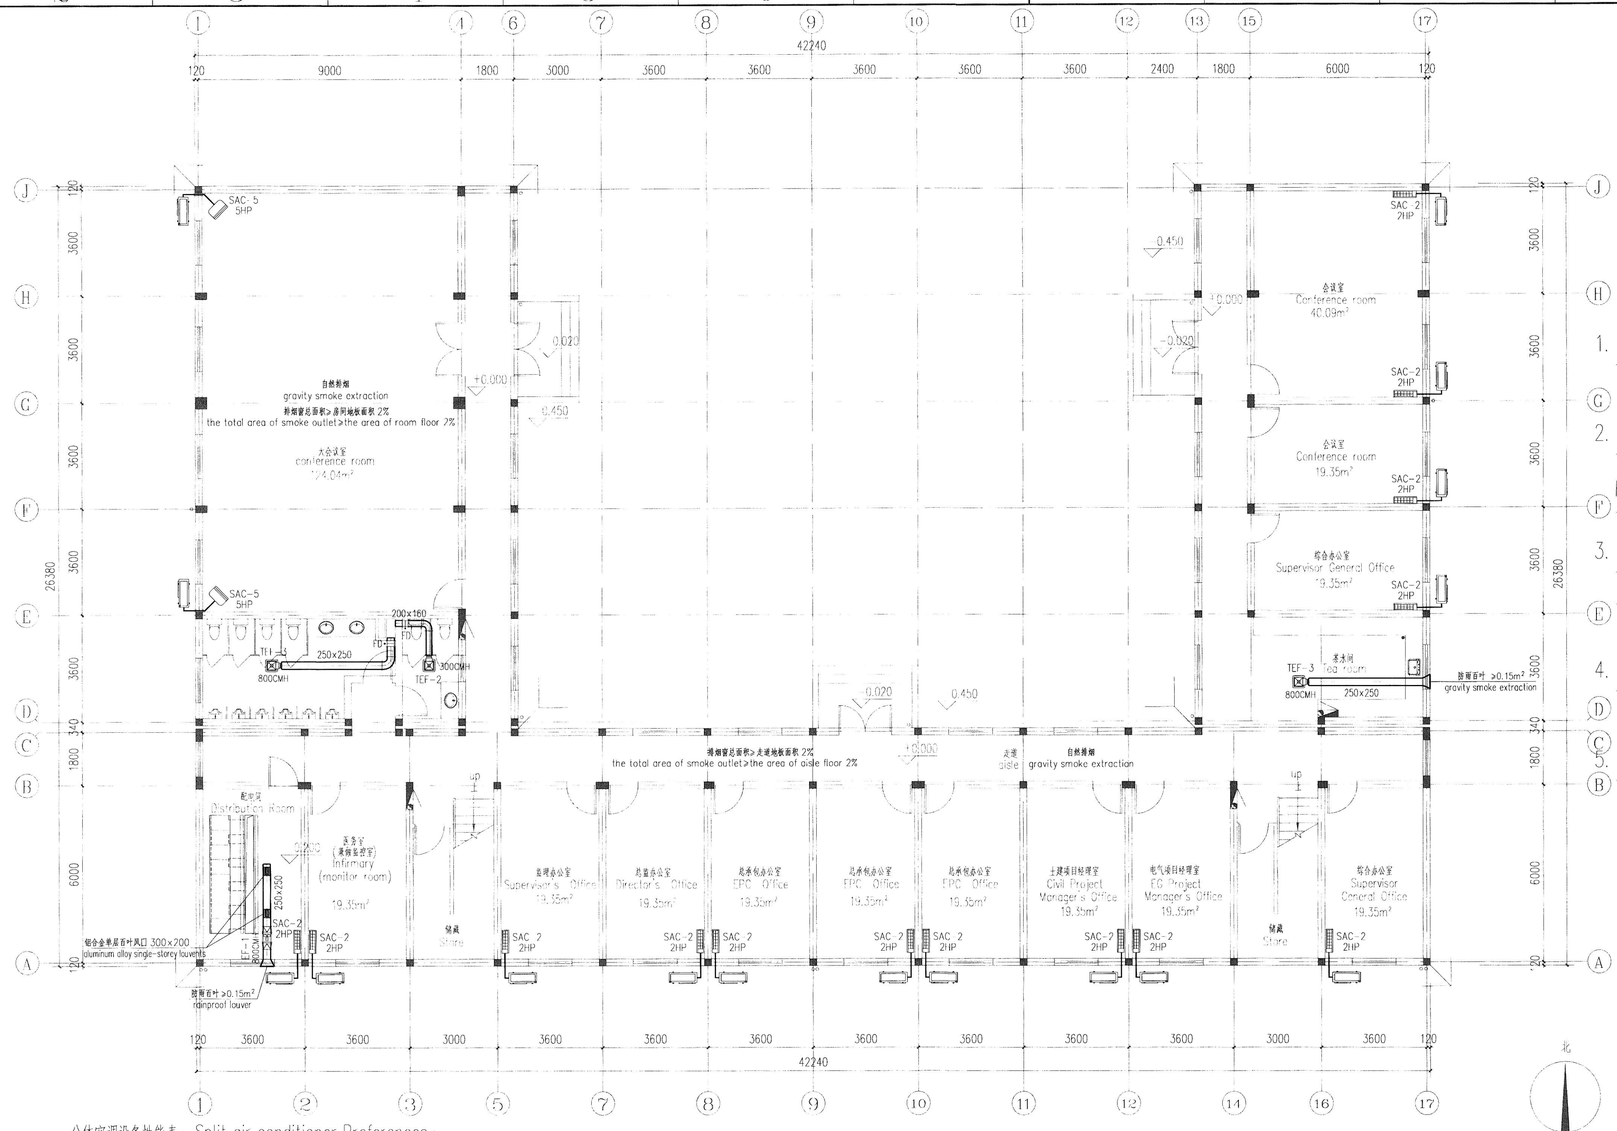

一层通风空调平面图 1:100

Ventilation and Air-Conditioning plan on the First floor

S=697.41m²

配件表：Parts Preferences：

防烟防火阀（70℃ 熔断）	fire damper（70℃ fusing）	250×250	个数 amount	2
防烟防火阀（70℃ 熔断）	fire damper（70℃ fusing）	200×160	个数 amount	2
铝合金单层百叶风口	aluminum alloy single-storey louvents	300×200	个数 amount	2
镀锌钢板	galvanized steel sheet	δ=0.5mm	平方米 m²	50
不锈钢丝网	stainless steel wire	Ø1x10x10	平方米 m²	1
冷凝水管（UPVC）	condensate pipe (UPVC)	De25	米 m	40
橡塑保温管壳	rubber and plastic insulation shell	δ=15mm	立方米 m³	0.05
金属软管	flexible metal tubing	Ø280	米 m	0.2

备注： Note:

1. 挡烟垂壁、排烟窗的设置、防雨百叶、无动力风帽（卫生间排风竖井）的规格及数量见建筑专业图纸
   The setting of smoke curtain and smoke outlet, the specification and quantity of rainproof louver and power hood are shown in the architectural drawings
2. 排气扇的面板标高同房间吊顶高度，风机、风管均贴梁底敷设；
   The panel elevation of the hide in ceiling fan is high with the ceiling height of the room, and the axial fan and air duct are all laid on the bottom of the beam；
3. 壁挂式室内机中心距地 2.1m，室外机底高于当层地坪（设备平台）100mm以上；
   The wall hanging type indoor unit center is 2.1 m from the room floor, the bottom of the outdoor unit is higher than the currentfloor (the equipment platform) 100mm above；
4. 空调冷凝水顺坡排至就近地漏或散水；
   The air-conditioner condenses water down the slope to the nearest floor drain or aproll；
5. 设计说明见图纸 B003701S-N0220-001。
   The design description is shown in the drawing B003701S-N0220-001.

图例 legend

SAC		分体空调室外机（侧出风） outdoor unit（sideward）
SAC		分体空调室内机（壁挂式） indoor unit（wall type）
SAC		分体空调室内机（柜式） indoor unit（cabinet type）
TEF		天花板管道式换气扇 hide in ceiling fan
FD		防烟防火阀（70℃ 熔断）就地手动开、关，输出信号 fire damper（70℃ fusing）Manually open, close in place, output signal
EF		轴流风机 axial fan

分体空调设备性能表：Split air conditioner Preferences：

设备编号 serial number	设备名称 device name	制冷量 capacity	制热量 capacity	制冷剂 media	室内机 indoor unit		电源要求 electrical source			套数 amount	备注 note
					重量 weight	循环风量 air volume	输入功率 input power	电源 electrical source	备注 note		
		kW	kW		kg	m³/h	kW	ø-V-Hz			
SAC-2	热泵型壁挂式（家用）Heat pump wall type (household)	5.0	5.6	R22	13.0	800	1.82	1-220-50	配电至内机 power to indoor unit	29	T3 工况 T3 working condition
SAC-3	热泵型壁挂式（家用）Heat pump wall type (household)	7.0	7.75	R22	17.0	1100	2.56	1-220-50	配电至内机 power to indoor unit	4	T3 工况 T3 working condition
SAC-5	热泵型柜式（家用）Heat pump cabinet type (household)	12.0	13.0	R22	51.0	1800	4.13	3-380-50	配电至内机 power to indoor unit	2	T3 工况 T3 working condition

风机性能表：Draught fan Preferences:

设备编号 serial number	服务区域 service area	风机形式 device form	参考型号 mode	驱动形式 Drive form	风量 flow	全压/静压 Total/Static pressure	最低效率 lowest efficiency	转速 rotate speed	电机功率 power	电源 electrical source	运行重量 Weight	机组噪声 noise	应急电源 emergency electricity	减振方式 vibration isolation	台数 amount	备注 note
					m³/h	Pa	%	rpm	kW	ø-V-Hz	kg	dB(A)				
EF-1	配电间 distribution room	轴流风机 axial fan	2.8#F	直接传动 Direct drive	800	38	>55	1450	0.025	3-380-50	14	≤55	无 N	S	1	

注：1.减振方式中，R表示橡胶类隔振方式，S表示弹簧隔振方式。 note：Vibration mode S：Spring vibration isolation. Vibration mode R：Rubber vibration isolation

排气扇性能表：hide in ceiling fan Preferences：

设备编号 serial number	服务区域 service area	风机形式 device form	参考型号 mode	驱动形式 drive form	风量 flow	全压/静压 Total/Static pressure	最低效率 lowest efficiency	转速 rotate speed	电机功率 power	单位风量耗功率 power consumption of unit flow	电源 electrical source	运行重量 weight	机组噪声 noise	应急电源 emergency electricity	台数 amount	备注 note
					m³/h	Pa	%	rpm	kW	W/(m³/h)	ø-V-Hz	kg	dB(A)			
TEF-2	卫生间 toilet	排风扇 hide in ceiling fan		直接传动 Direct drive	300	--/30	≥52	--	0.06	--	1-220-50	6.5	≤46	--	2	自带止回阀 With check valve
TEF-3	卫生间、茶水间 toilet、tea room	排风扇 hide in ceiling fan		直接传动 Direct drive	800	--/50	≥52	--	0.15	--	1-220-50	10.0	≤58	--	3	自带止回阀 With check valve

专业 Speciality	会签 Sign	日期 Date
建筑 Architecture		
结构 Structure		
电气 Electrical		
给排水 Water supply and drainage		

Reference Drawings

Drwg. No.	Title

Revisions

	Name	Date	Notes

巴基斯坦默蒂亚里—拉合尔±660kV直流输电工程
±660kV HVDC Project from Matiari to Lahore in Pakistan

NATIONAL TRANSMISSION & DESPATCH COMPANY (NTDC) LIMITED PAKISTAN

CONTRACTOR 国家电网 STATE GRID 中国电力技术装备有限公司 CHINA ELECTRIC POWER TECHNOLOGY EQUIPMENT CO.,LTD.

SUBCONTRACTOR East China Electric Power Design Institute Co.,Ltd.

拉合尔±660kV换流站
±660kV Lahore Converter Station

设计阶段 PHASE：施工图 Detail Design

M L H V D C - L C S - E C I - D D - H A - 0 2 2 0 - 0 0 2 A

	姓名 Name	日期 Date
设计 Designed	张交芳	2017.10.30
校核 Checked	王新林	2017.10.30
审核 Reviewed	和翠翠	2017.10.30
批准 Approved	和翠翠	2017.10.30

一层通风空调平面图
Ventilation and Air-Conditioning plan on the First floor

比例 Scale 1:100 | 图号 DWG NO. 30-B003701S-N0220-002 | 版本 REV. A

594X841